Simon's Bathroom

Hall bath renovation · 5'-0" × 8'-11" with walk-in shower



Design rendering from the doorway (Blender / Cycles). Finishes are representative.

DESIGN INTENT

Classic bath with a traditional brown-ash vanity (Carrara marble top, undermount oval basin), marble Calacatta Verde 2×2 mosaic floor and a walk-in shower in glossy grey handmade-look subway tile, 6×12 below a pencil liner 2" below the shower handle and 3×8 above to the ceiling, behind clear frameless glass. All plumbing trim and hardware satin / brushed nickel.

GENERAL NOTES

1. Dimensions come from the design model (built from the owner's SketchUp file). Field-verify every dimension before ordering or cutting; the room has not been field-measured for this set.
2. Plan dimensions are to finished wall faces. Heights are above finished floor (AFF).
3. Fixture sizes are the specified products' published dimensions; confirm rough-ins against the manufacturer spec sheets on site.
4. Toilet: 12" rough-in, centered 15⅞" from the vanity and from the shower jog wall (code min. 15" to centerline, 21" clear in front).
5. Shower: provide waterproof membrane on all wet walls and the pan, sloped to the drain. Niche is recessed into the window-side wall, lined in 3×8 with a marble sill.
6. Shower tile set-out: running bond; lay out each wall so both end cuts are equal size and no cut is under 2½". Liner 37¾–38½" AFF, 2" below the shower handle; 6×12 below it with equal 3⅝" cuts at the pan and under the liner; full 3×8 rows up from the liner, cut row at the ceiling.
7. Exhaust fan and GFCI receptacle are required by code but not modeled — locate with the electrician.
8. Owner direction: no plant or vase on the vanity; vanity hardware and faucet satin nickel.

SHEET INDEX

A-001	Cover, notes & index
A-101	Floor plan — dimensioned
A-201	Elevations — vanity / toilet wall & door wall
A-202	Elevations — window wall & shower
A-401	Reflected ceiling & lighting plan
A-501	Fixture & finish schedule

BATHROOM REMODEL

Simon's Bathroom

Layout, fixtures & finishes

Issued 2026-11-01

For coordination — not for construction


NOTES

Dimensions from the design model, built from the owner's SketchUp.
Verify all dimensions in field.
Do not scale drawings.
Heights are above finished floor.
Plan dims to finished wall faces.

COVER, NOTES & INDEX

Design intent, general notes and sheet index

A-001

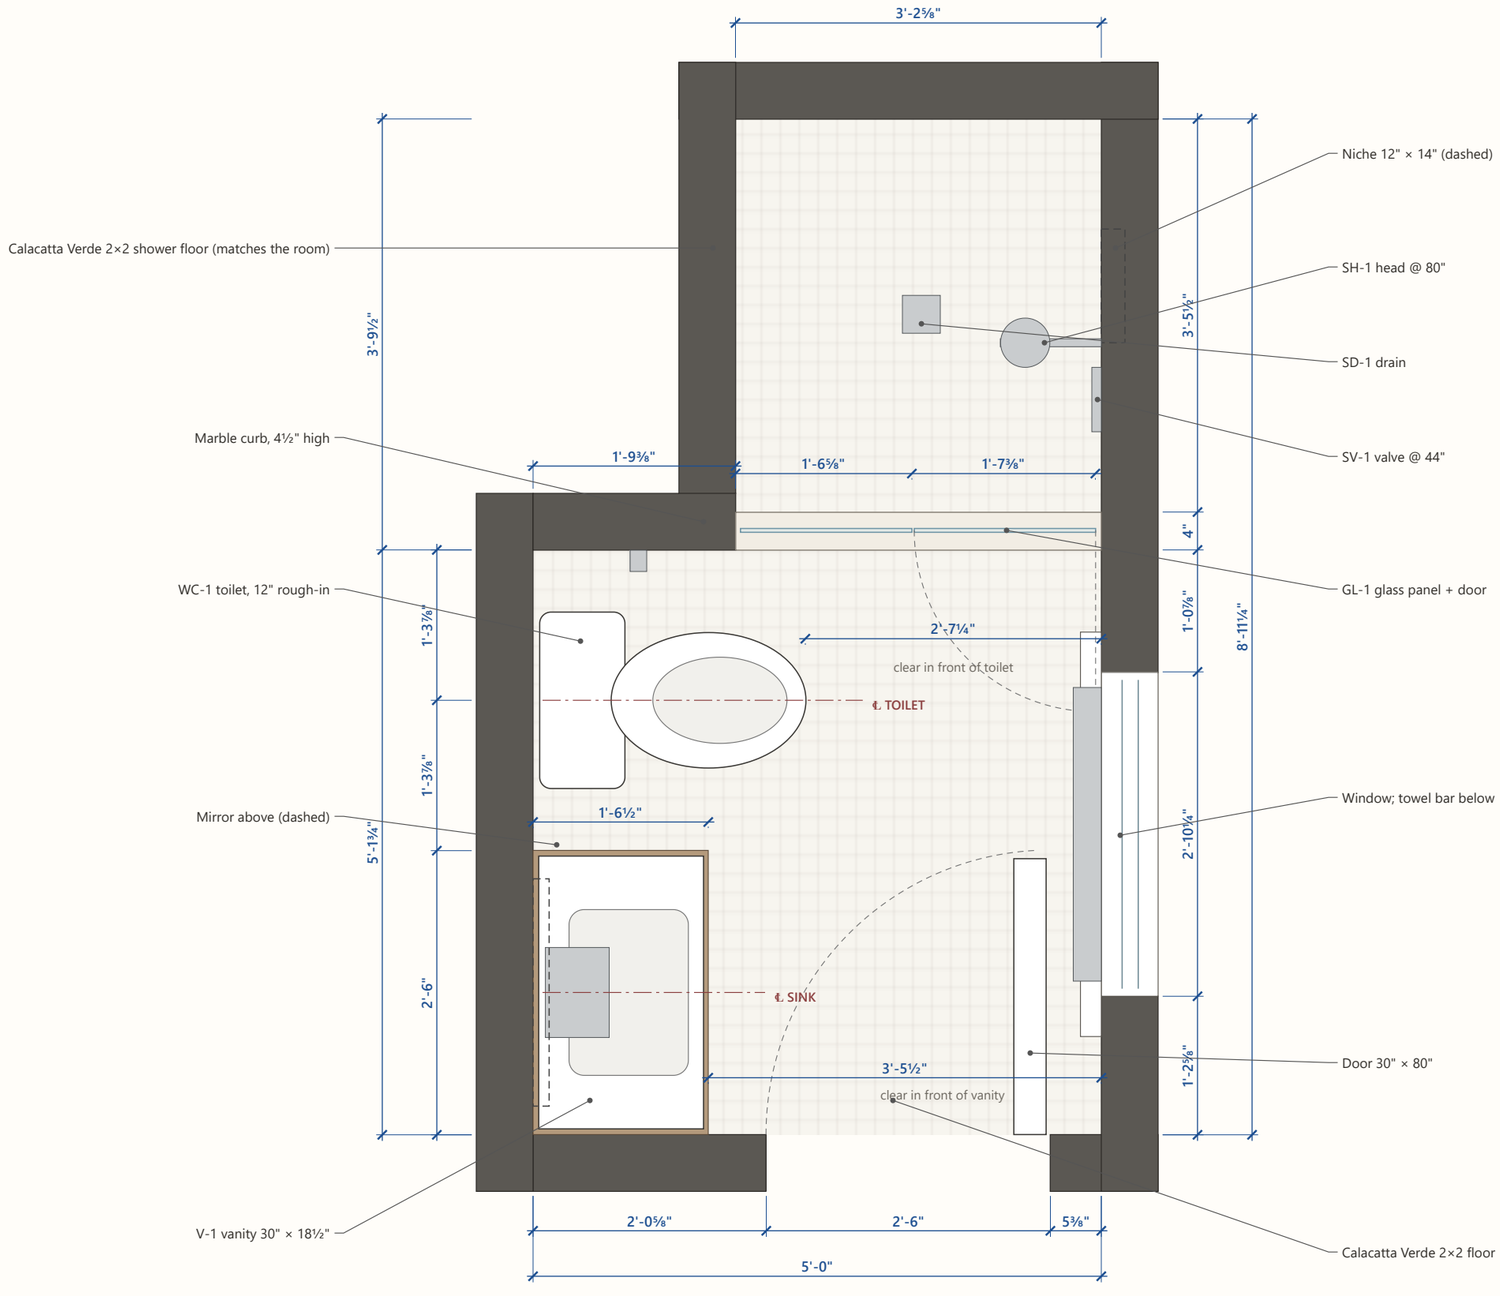

PLAN NOTES

Toilet centerline 1'-3⅜" from the vanity side and 1'-3⅜" from the jog wall (code min. 15"). 2'-7¼" clear in front (min. 21").

Sink centerline 1'-3" from the door wall.

Shower inside 3'-2⅝" × 3'-5½" beyond a 4" curb; glass 5'-11½" tall on the curb, door 1'-7⅛" hinged off the window-side wall.

Window rough opening 2'-10¼" wide, sill 4'-6⅝" AFF.

Door hinged on the window side; it opens flat against the window-side wall.

Floor tile runs under the vanity and to the curb; the same 2×2 mosaic carries on across the curb into the shower, sloped to the drain.

LEGEND

- Wall (existing / new, 6")
- Above / recessed (mirror, niche)
- Door swing
- Centerline

1 FLOOR PLAN

3/4" = 1'-0" on 11×17 · north = toward the shower

BATHROOM REMODEL

Simon's Bathroom

Layout, fixtures & finishes

Issued 2026-11-01

For coordination — not for construction


NOTES

Dimensions from the design model, built from the owner's SketchUp.
Verify all dimensions in field.
Do not scale drawings.
Heights are above finished floor.
Plan dims to finished wall faces.

FLOOR PLAN — DIMENSIONED


Room, fixture locations, clearances and rough-in centerlines

A-101

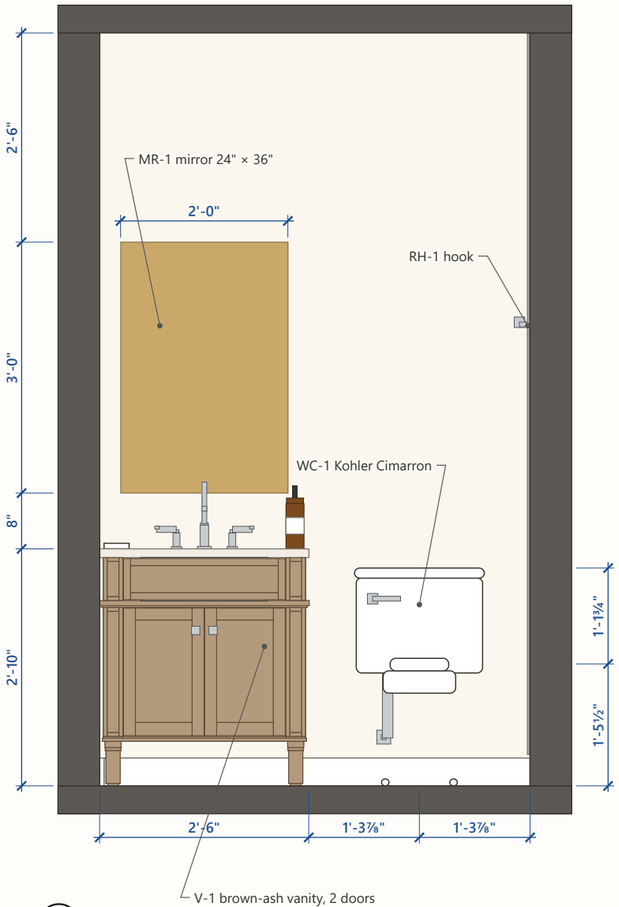

1 **VANITY & TOILET WALL**

1/2" = 1'-0" on 11×17 · looking west

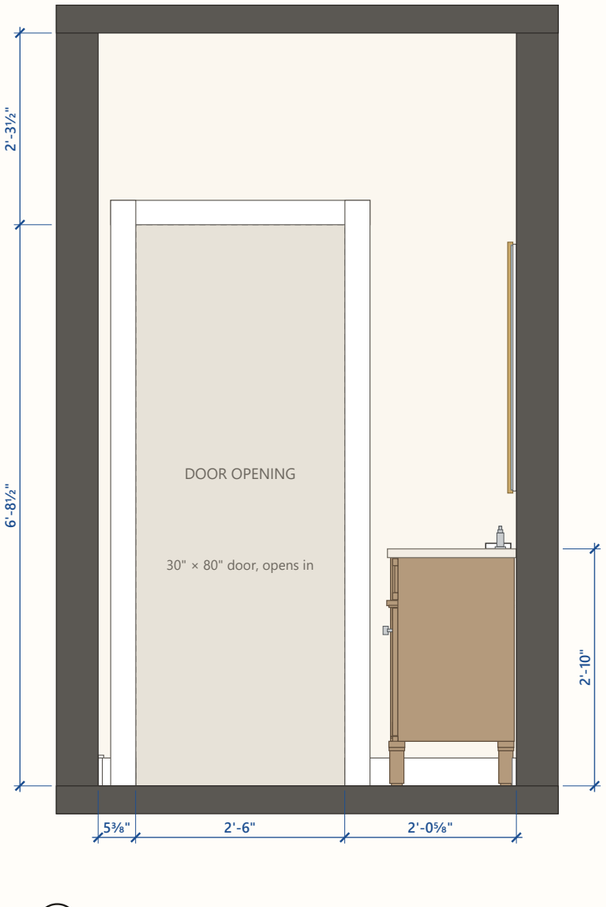

2 **DOOR WALL**

1/2" = 1'-0" on 11×17 · looking south

BATHROOM REMODEL

Simon's Bathroom

Layout, fixtures & finishes

Issued 2026-11-01

For coordination — not for construction


NOTES

Dimensions from the design model, built from the owner's SketchUp.
Verify all dimensions in field.
Do not scale drawings.
Heights are above finished floor.
Plan dims to finished wall faces.

INTERIOR ELEVATIONS


Vanity & toilet wall and door wall

A-201

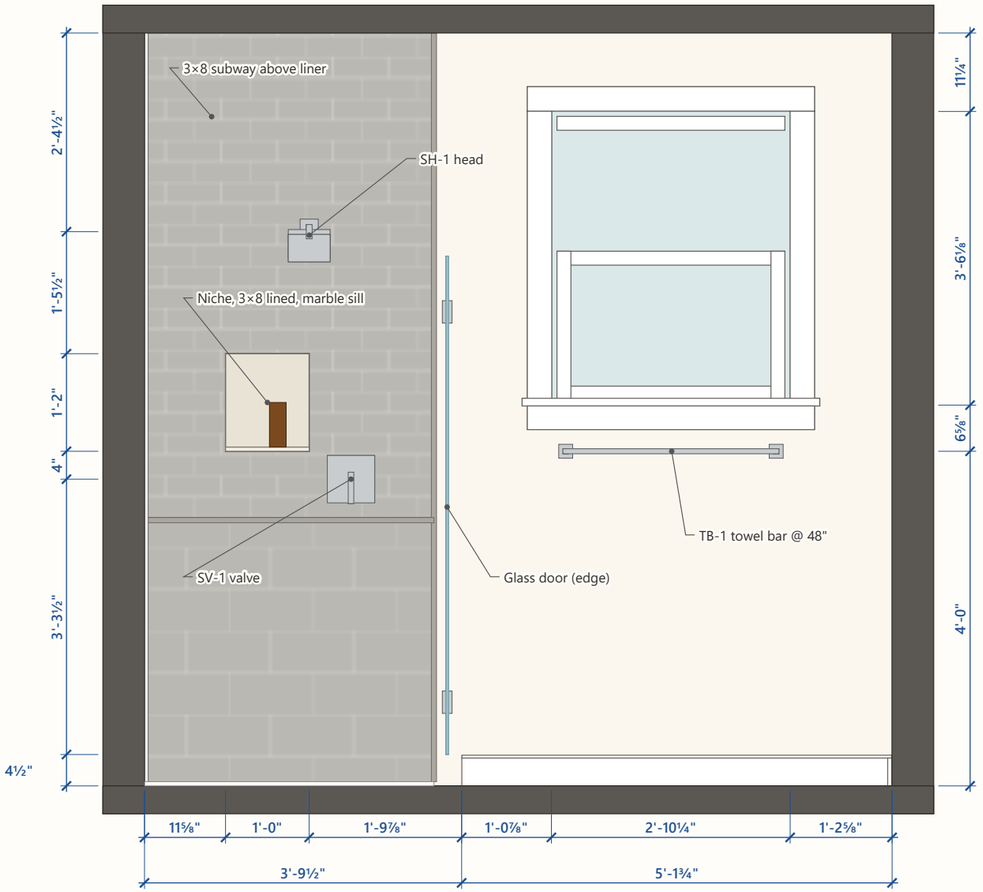

3 **WINDOW WALL**

1/2" = 1'-0" on 11×17 · looking east

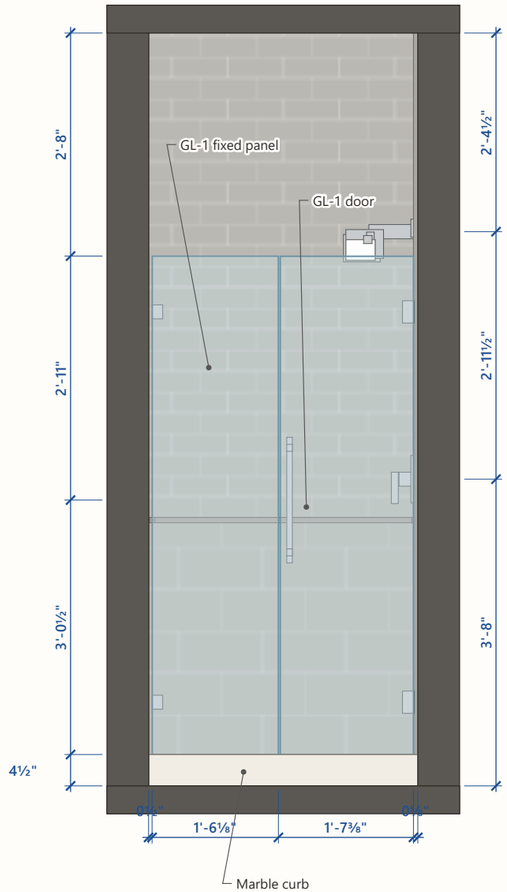

4 **SHOWER**

1/2" = 1'-0" on 11×17 · looking north, through the glass

BATHROOM REMODEL

Simon's Bathroom

Layout, fixtures & finishes

Issued 2026-11-01

For coordination — not for construction


NOTES

Dimensions from the design model, built from the owner's SketchUp.
Verify all dimensions in field.
Do not scale drawings.
Heights are above finished floor.
Plan dims to finished wall faces.

INTERIOR ELEVATIONS

Window wall (with shower side wall) and shower back wall

A-202

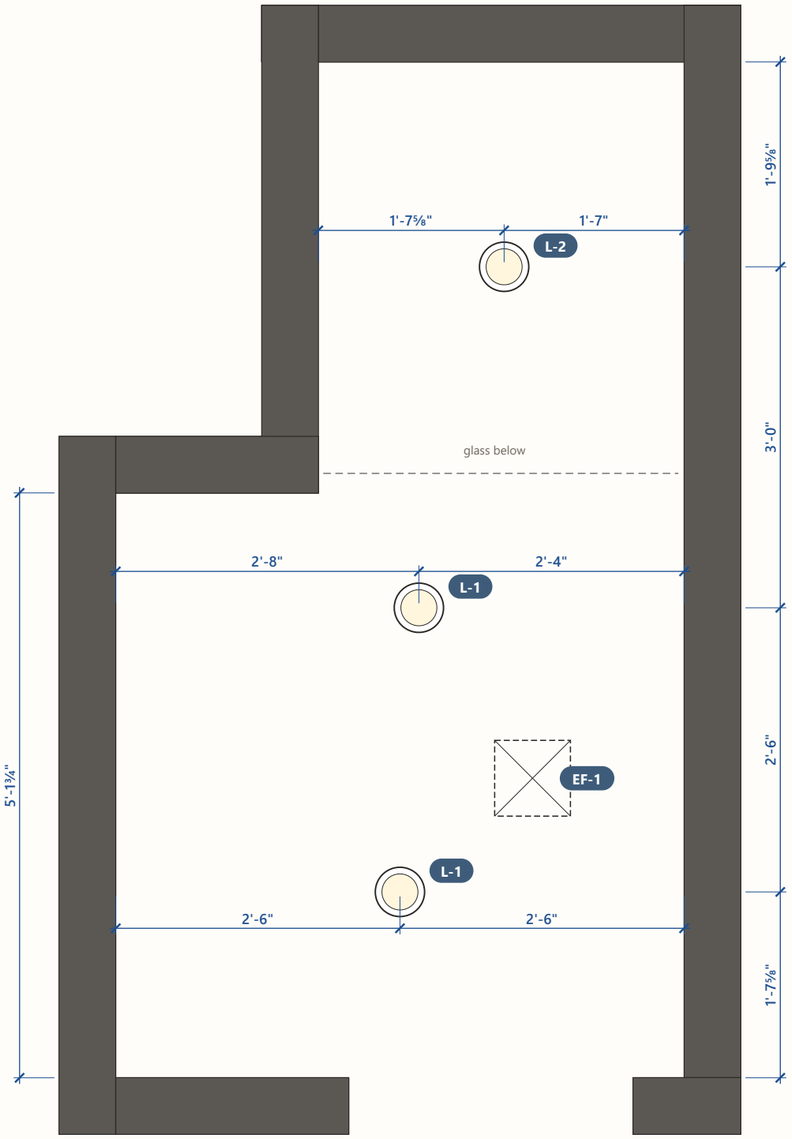

1 **REFLECTED CEILING PLAN**

3/4" = 1'-0" on 11×17 · ceiling 9'-0" AFF

LIGHTING SCHEDULE

L-1	× 2	4" recessed downlight, white trim, 2700–3000 K, dimmable
L-2	× 1	4" recessed downlight, wet-location rated (shower), 3000 K
EF-1	× 1	Exhaust fan (code required, not in model) — location TBD, ducted to exterior

NOTES

Switch at the door, latch side (window wall), 48" AFF: L-1/L-2 on a dimmer; EF-1 separate. No wall sconce (owner).

Shower downlight must be rated for wet locations; GFCI protection per code.

Dashed square = suggested fan location, clear of joists to be confirmed in field.

BATHROOM REMODEL

Simon's Bathroom

Layout, fixtures & finishes

Issued 2026-11-01

For coordination — not for construction

NOTES

Dimensions from the design model, built from the owner's SketchUp.
Verify all dimensions in field.
Do not scale drawings.
Heights are above finished floor.
Plan dims to finished wall faces.

REFLECTED CEILING & LIGHTING PLAN

Fixture locations from the design model

A-401

FIXTURES & EQUIPMENT

Tag	Item	Product	Size / finish / location
V-1	Vanity	30" traditional freestanding vanity, weathered brown ash, per owner's product photo	30" W × 18½" D × 34" H; Carrara marble top, undermount oval basin; recessed-panel corner pilasters, false drawer front, belt moulding, 2 shaker doors; turned tapered legs; satin nickel round knobs (owner choice over the stock bronze)
F-1	Lavatory faucet	Kohler-style 3-piece widespread, arched spout, lever handles	Brushed nickel (owner: not the photo's bronze); 8" spread; verify with top's 3 holes
WC-1	Toilet	Kohler Cimarron Comfort Height elongated, 2-piece	12" rough-in; 28-13/16" D, 18-5/8" W tank, 16½" rim, 31¼" H; left-hand lever
SV-1	Shower valve & trim	Pressure-balance valve, single lever trim	Brushed nickel; valve center 44" AFF on the window-side wall
SH-1	Shower head & arm	Wall-mount head on straight arm	Brushed nickel; arm 80" AFF
SD-1	Shower drain	4" square tile-in drain cover	Brushed nickel; at shower center
GL-1	Shower glass	Frameless ⅜" clear (low-iron) fixed panel + hinged door with pull bar	Panel 1'-6⅛", door 1'-7⅛"; 5'-11½" tall on the curb; nickel clamps & hinges
MR-1	Mirror	Rejuvenation Rounded Rectangle Metal Mirror (solid brass frame, French cleat)	24" W × 36" H, centered over the vanity, bottom 42" AFF; aged brass
TB-1	Towel bar	30" towel bar	Satin nickel; under the window at 48" AFF
RH-1	Robe hook	Single hook	Satin nickel; jog wall at 66" AFF

FINISHES

Surface	Material	Where / notes
Floor	Surfaces Galore Calacatta Verde Royale marble 2"×2" mosaic, honed (SG999), 12" sheets, ⅜" thick	Main room, under the vanity, and the shower floor; straight lay, 1/16" grout; grout line on the vanity wall, 30 full tiles across
Shower walls	Glossy warm-grey handmade-look subway, running bond: 6" × 12" below a ¾" pencil liner 2" below the shower handle (37¾" AFF), 3" × 8" above	All three shower walls to the ceiling; pencil trim on exposed edges; niche lined in 3×8; light grey grout
Shower floor	Same Calacatta Verde 2×2 mosaic as the room	Grid continuous with the main floor; sloped to the drain
Curb & niche sill	Polished Carrara-type marble	Curb 4" × 4½" high
Walls	Warm cream paint, matte / eggshell (bath rated)	All non-tiled walls
Ceiling	Flat white paint, bath rated	9'-0" AFF
Trim	Semi-gloss white; 4" baseboard, door & window casings	Match existing profiles
Hardware	Satin / brushed nickel throughout	Vanity knobs, faucet, accessories, shower trim

BATHROOM REMODEL

Simon's Bathroom

Layout, fixtures & finishes

Issued 2026-11-01

For coordination — not for construction

NOTES

Dimensions from the design model, built from the owner's SketchUp.
Verify all dimensions in field.
Do not scale drawings.
Heights are above finished floor.
Plan dims to finished wall faces.

FIXTURE & FINISH SCHEDULE

Products and finishes as designed — confirm availability and lead times

A-501