KITCHEN REMODEL

Dimensioned cabinet & layout drawings for the contractor



Design render — looking at the cabinet wall from the living room



Design render — island, range wall and fridge / pantry

GENERAL NOTES

1. All dimensions come from the 3D design model (SketchUp → Blender), not from field measurement. Verify every dimension on site before ordering cabinets, stone or appliances.
2. Do not scale drawings — use the written dimensions. Sheets are laid out for 11×17 (tabloid); stated scales apply only at 100% print size.
3. Plan dimensions run from the finished inside face of the Breakfast (left) wall and the cabinet (back) wall. Heights are above finished floor (AFF).
4. Cabinet sizes are box widths. Fronts are inset shaker with 3" stiles/rails. Toe kick 4" high; countertops 1⅜" thick (model), 1" front overhang.
5. Appliance openings were sized to the UAKC spec package (invoice 255075, v2.2) — see A-502 for every requirement, utility and panel size. Confirm against the installation guide in each box.
6. The model has no outlets, switches or plumbing rough-in. Only fixture locations (A-401) and appliance/sink centerlines are given.
7. Wall thickness is drawn nominal (3"). Hood, hutch, fridge surround and island furniture details are design intent — shop drawings to follow from the cabinetmaker.

SHEET INDEX

A-001	Cover, notes & index
A-101	Overall floor plan
A-102	Kitchen plan — dimensioned
A-201	Cabinet wall elevation
A-202	Island elevations
A-203	Side wall elevations
A-301	Sections through range and sink
A-401	Lighting / reflected ceiling plan
A-501	Cabinet & appliance schedules
A-502	Appliance requirements (spec check)

KEY DIMENSIONS

Room, wall to wall (cabinet wall)	21'-1"
Ceiling height	9'-0"
Counter height	36"
Upper cabinets, bottom AFF	54⅛"
Upper cabinets, top AFF	8'-⅛"
Island top	8'-6"
Aisle, counter edge to island	49"

KITCHEN REMODEL

Jane's Kitchen

Cabinet & layout dimensions

Issued 2026-10-21

For coordination — not for construction


NOTES

Dimensions from the design model.
Verify all dimensions in field.
Do not scale drawings.
Heights are above finished floor.
Plan dims from inside face of
left wall / back wall.

COVER, NOTES & INDEX

General notes · sheet index · design intent

A-001

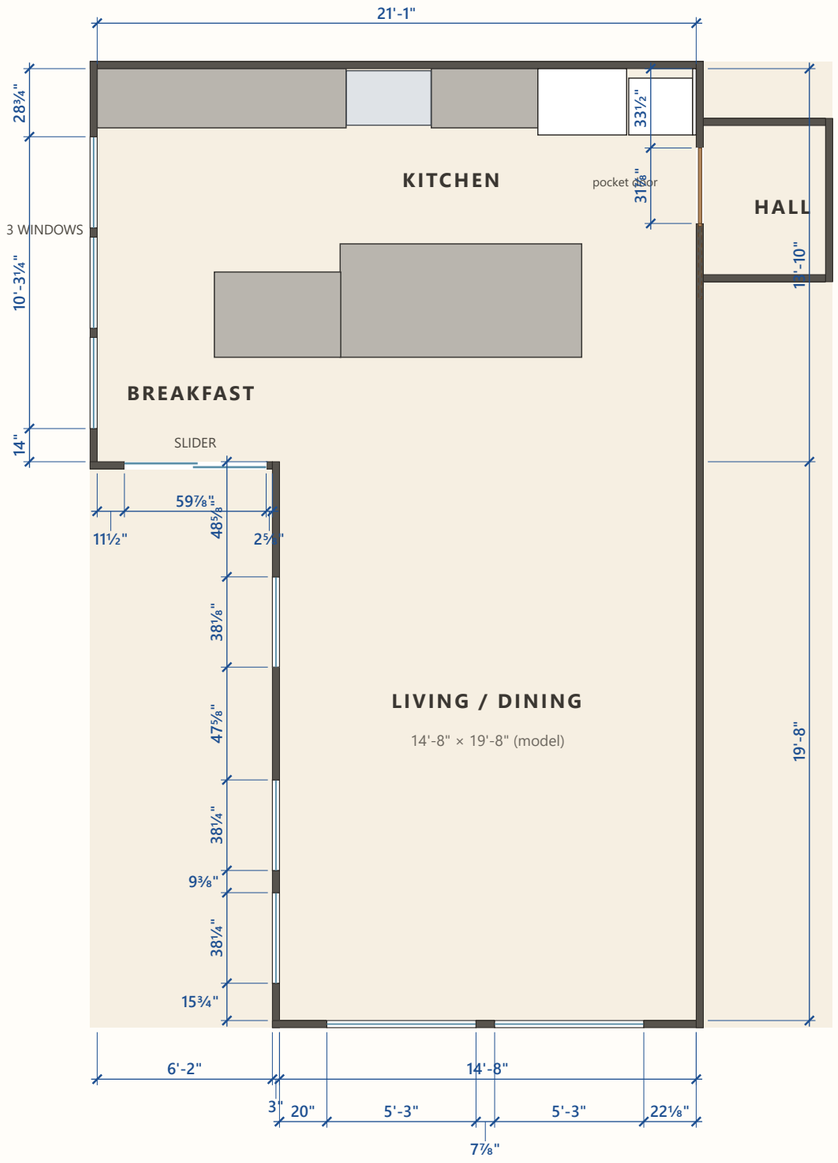

1 **OVERALL FLOOR PLAN**

3/16" = 1'-0" at 11×17 · window sizes approximate (from floor plan)

LEGEND

- Wall (nominal 3")
- Window
- Countertop / stone
- Tall cabinet / appliance panel
- Pocket door pocket

Room names follow the floor plan supplied by the owner. Living / Dining walls and windows are approximate — verify on site.

KITCHEN REMODEL

Jane's Kitchen

Cabinet & layout dimensions

Issued 2026-10-21

For coordination — not for construction


NOTES

Dimensions from the design model.
Verify all dimensions in field.
Do not scale drawings.
Heights are above finished floor.
Plan dims from inside face of
left wall / back wall.

OVERALL FLOOR PLAN

Kitchen, Breakfast and Living / Dining

A-101

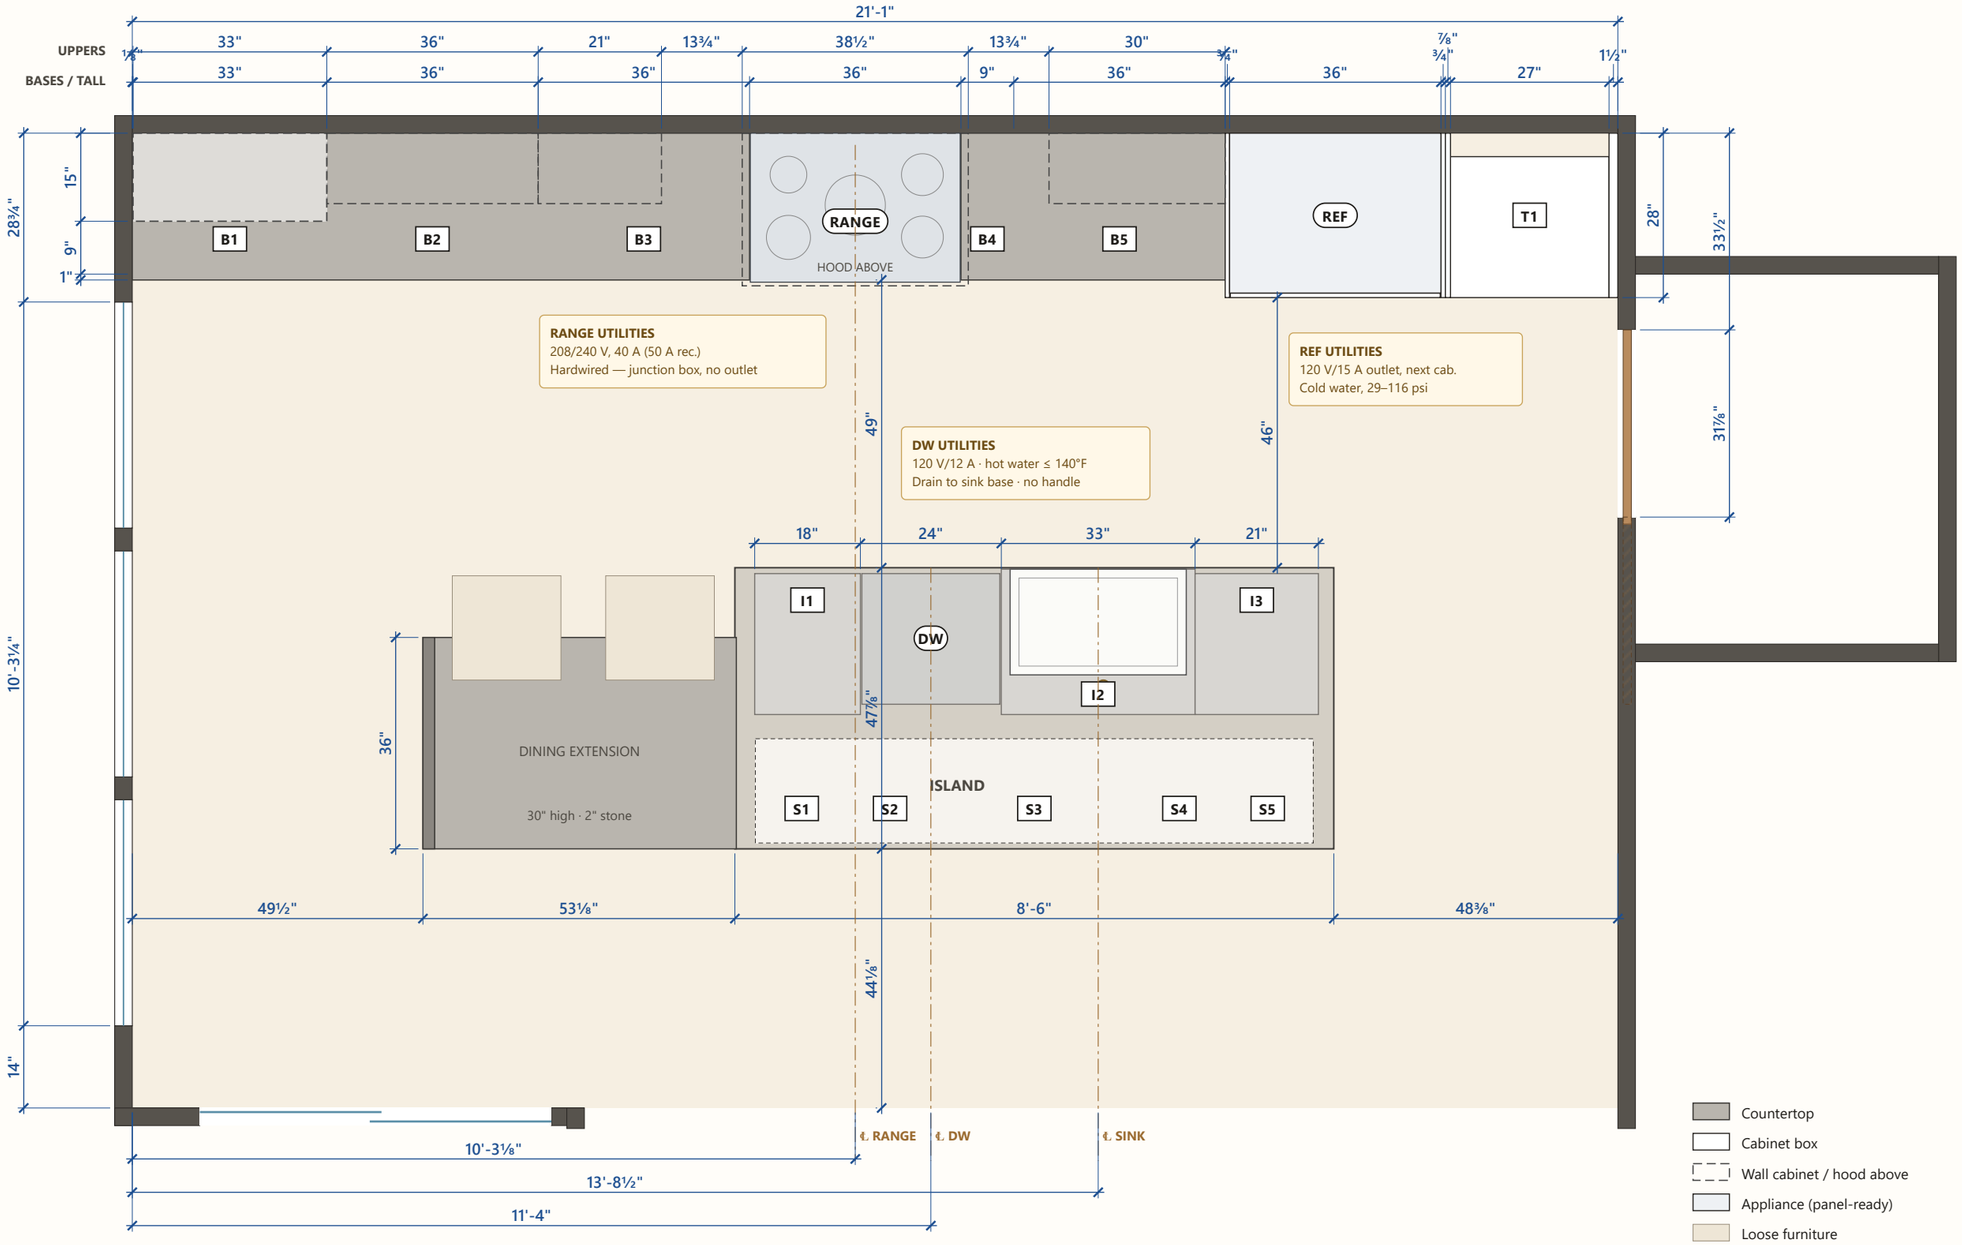

Countertop
Cabinet box
Wall cabinet / hood above
Appliance (panel-ready)
Loose furniture

1 **KITCHEN PLAN**

≈ 1/2" = 1'-0" at 11×17 (reduced to fit) — use dimensions · dashed = cabinets/hood above

KITCHEN REMODEL

Jane's Kitchen

Cabinet & layout dimensions

Issued 2026-10-21

For coordination — not for construction


NOTES

Dimensions from the design model.
Verify all dimensions in field.
Do not scale drawings.
Heights are above finished floor.
Plan dims from inside face of
left wall / back wall.

KITCHEN PLAN — DIMENSIONED

Cabinet runs, island location,
clearances and rough-in centerlines

A-102

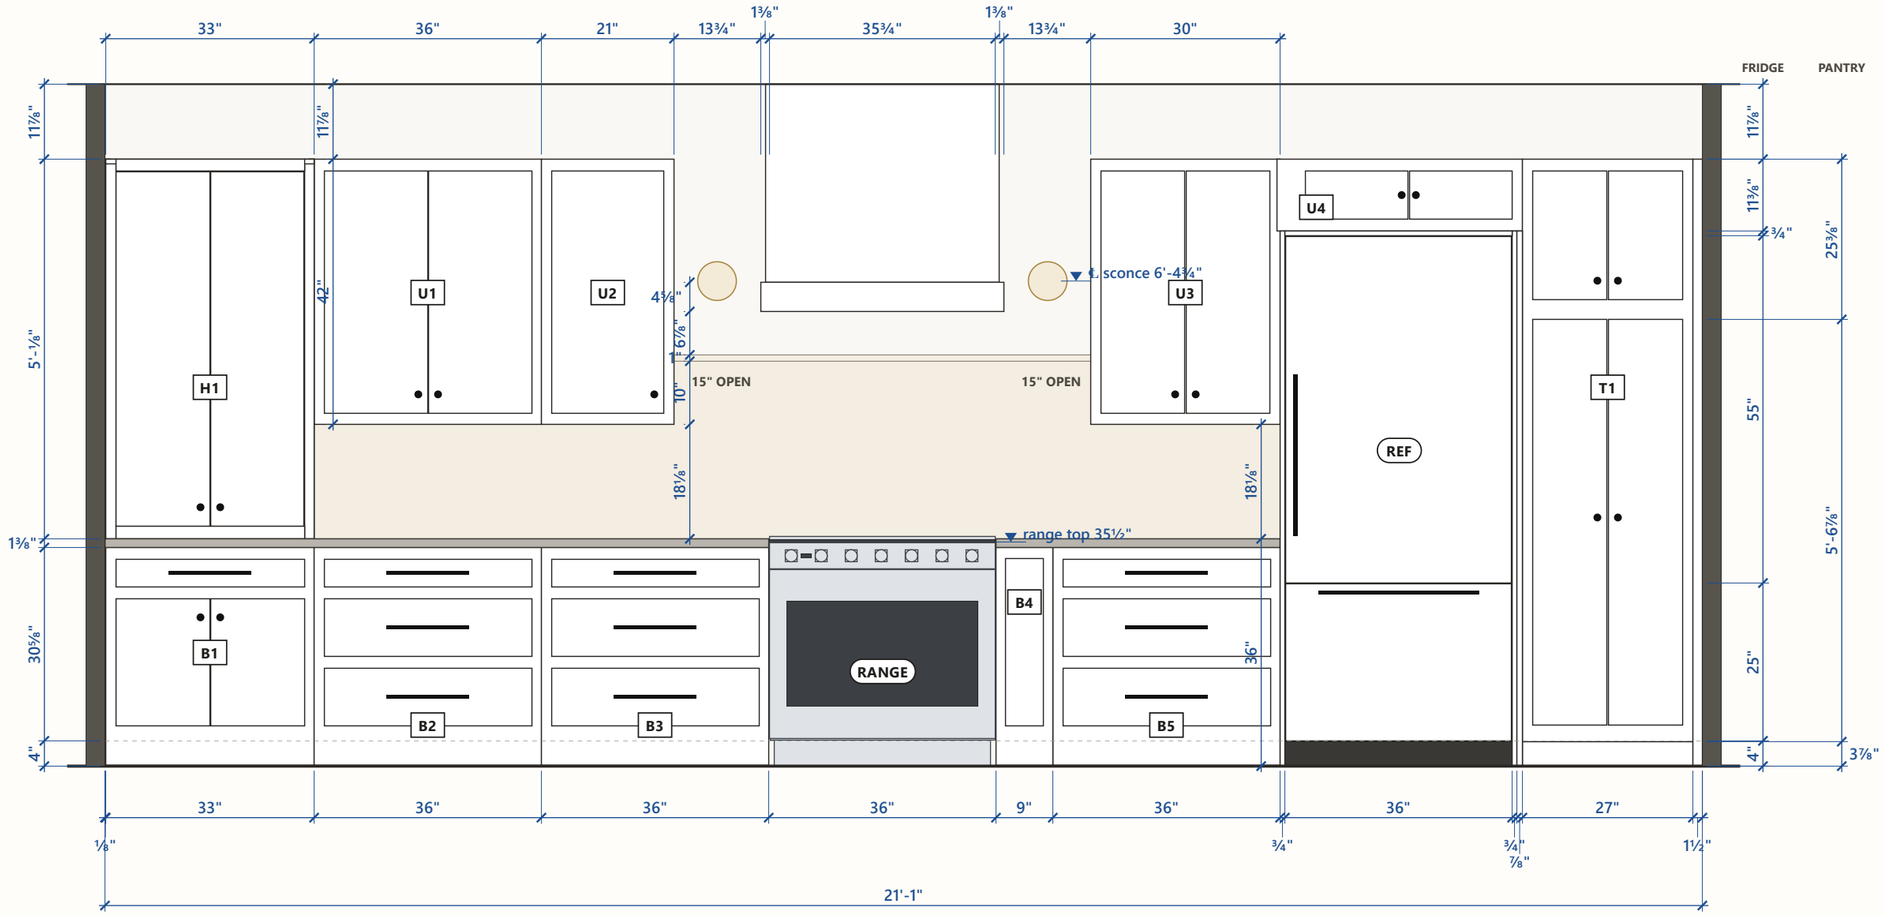

Backsplash: one marble slab, counter to underside of uppers (18⅛"); rises 10" in the range bay and is capped by a 3½"-deep marble ledge. Painted wall above the ledge with two sconces.

Hood: plaster, 37" body to ceiling over a 38½" × 26"-deep mantle band; stainless insert, 3 baffle filters, 2 lights. Bottom of hood 72" AFF = 36" above the cooktop.

Hutch H1 sits on the counter, 15" deep (3" proud of the 12" uppers), top flush with uppers.

Hardware: matte black 1¼" knobs, 12" bar pulls on drawers, 24" appliance pulls on fridge.

1 **CABINET WALL ELEVATION**

1/2" = 1'-0" at 11×17 · looking at the back wall from the room

KITCHEN REMODEL

Jane's Kitchen

Cabinet & layout dimensions

Issued 2026-10-21

For coordination — not for construction


NOTES

Dimensions from the design model.
Verify all dimensions in field.
Do not scale drawings.
Heights are above finished floor.
Plan dims from inside face of
left wall / back wall.

CABINET WALL ELEVATION


Back wall: hutch, range & hood, fridge, pantry

A-201

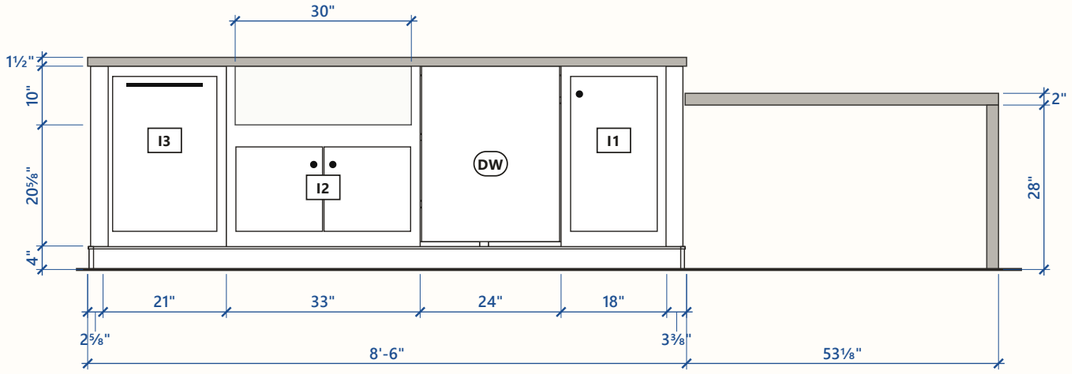


1 ISLAND — WORKING SIDE (SINK / DISHWASHER)

≈ 1/2" = 1'-0" (reduced) · seen from the range

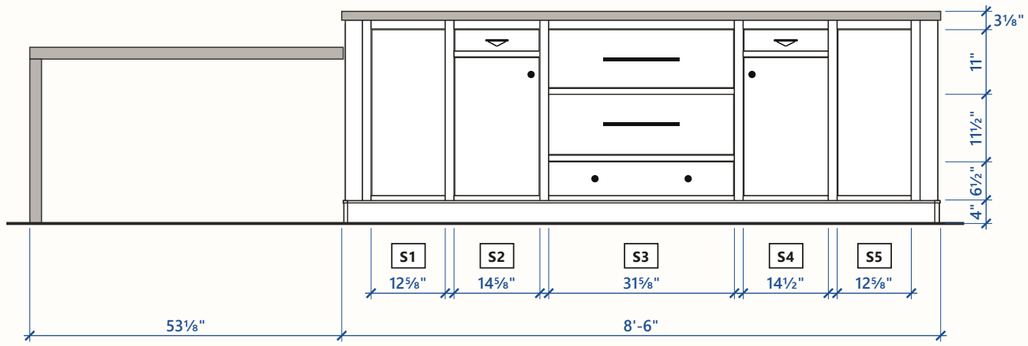


2 ISLAND — SEATING SIDE (STORAGE)

≈ 1/2" = 1'-0" (reduced) · seen from the living room · opening widths, 1½" stiles

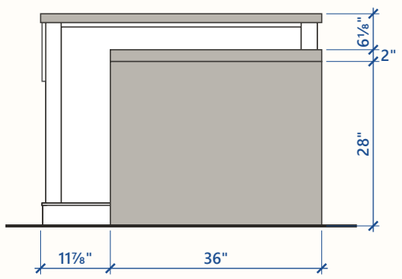

3 ISLAND — LEFT END WITH DINING EXTENSION

≈ 1/2" = 1'-0" (reduced) · seen from the Breakfast end

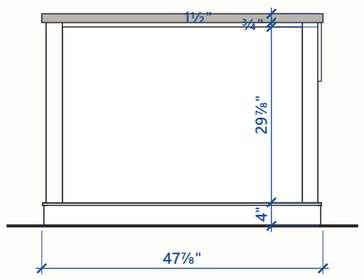

4 ISLAND — RIGHT END (HALL SIDE)

≈ 1/2" = 1'-0" (reduced)

Island body: painted furniture piece, square corner posts, 4" plinth wrapping all four sides, paneled ends. Top overhangs the body ½"–⅞" on all sides (model).

Working side (faces the range): 18" door base, 24" dishwasher with custom panel, 33" sink base with 30" apron-front sink, 21" double trash pull-out.

Dining extension butts the left end: 2" stone slab, 30" high, waterfall leg at the free end, flush with the island's seating (living-room) side.

KITCHEN REMODEL

Jane's Kitchen

Cabinet & layout dimensions

Issued 2026-10-21

For coordination — not for construction


NOTES

Dimensions from the design model.
Verify all dimensions in field.
Do not scale drawings.
Heights are above finished floor.
Plan dims from inside face of
left wall / back wall.

ISLAND ELEVATIONS

Working side, seating side and both ends


A-202

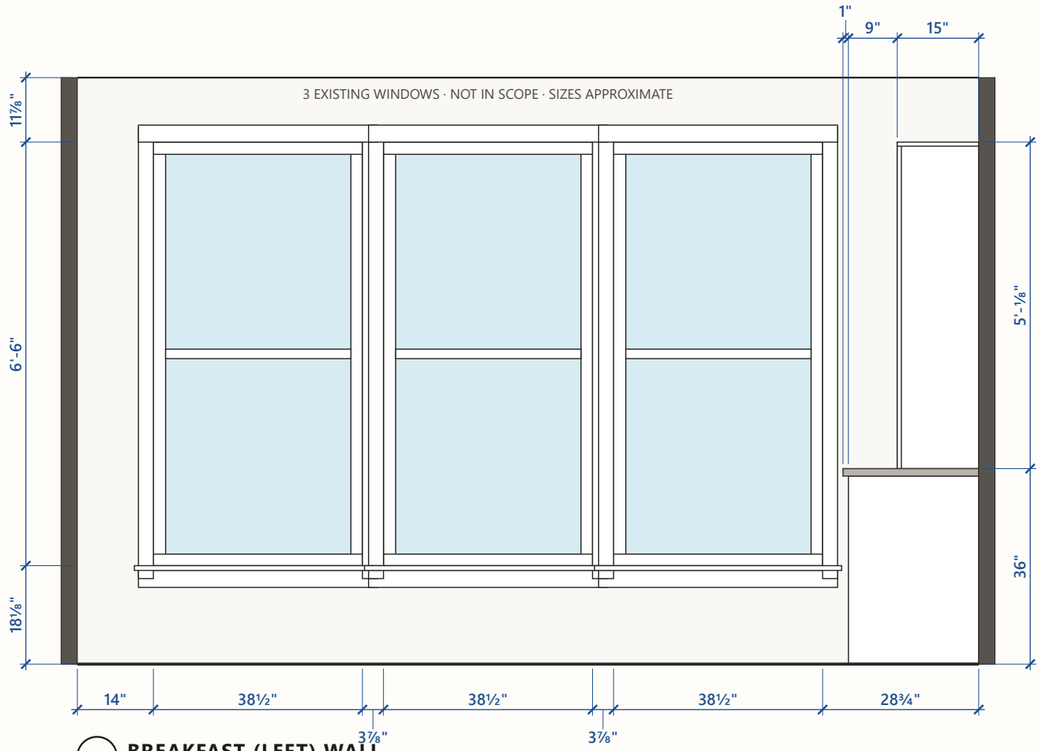

1 BREAKFAST (LEFT) WALL

≈ 1/2" = 1'-0" (reduced) · seen from the room · cabinet wall at right

Three existing windows on this wall stay as they are — sizes are approximate. The 2-panel sliding door is around the corner on the porch wall (see A-101). Hutch H1 and base B1 return against this wall — scribe to the wall.

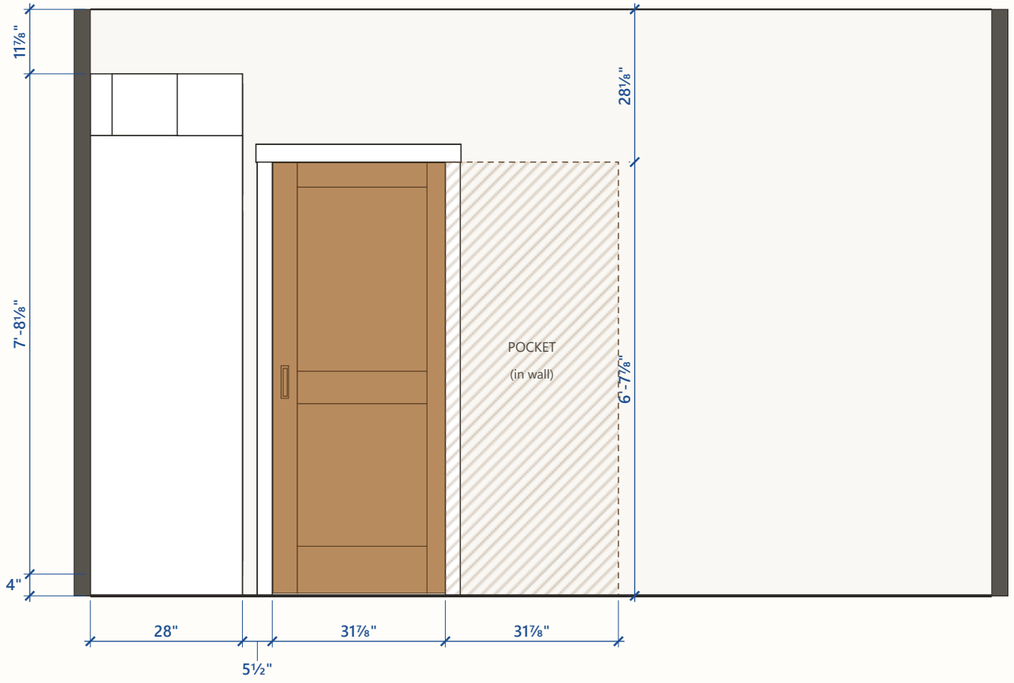

2 HALL (RIGHT) WALL

≈ 1/2" = 1'-0" (reduced) · seen from the room · cabinet wall at left

Pocket door replaces the existing swing door. The pocket needs a clear stretch of wall about one door width (shown hatched) on the living-room side — check that wall for plumbing, ducts and wiring before ordering the frame.

Pantry side is closed with a 1½" filler to the wall (model). Tall cabinets and fridge panels stand 4" proud of the base cabinet faces (28" deep).

KITCHEN REMODEL

Jane's Kitchen

Cabinet & layout dimensions

Issued 2026-10-21

For coordination — not for construction


NOTES

Dimensions from the design model.
Verify all dimensions in field.
Do not scale drawings.
Heights are above finished floor.
Plan dims from inside face of
left wall / back wall.

SIDE WALL ELEVATIONS


Breakfast wall (3 windows) and hall wall (pantry end, pocket door)

A-203

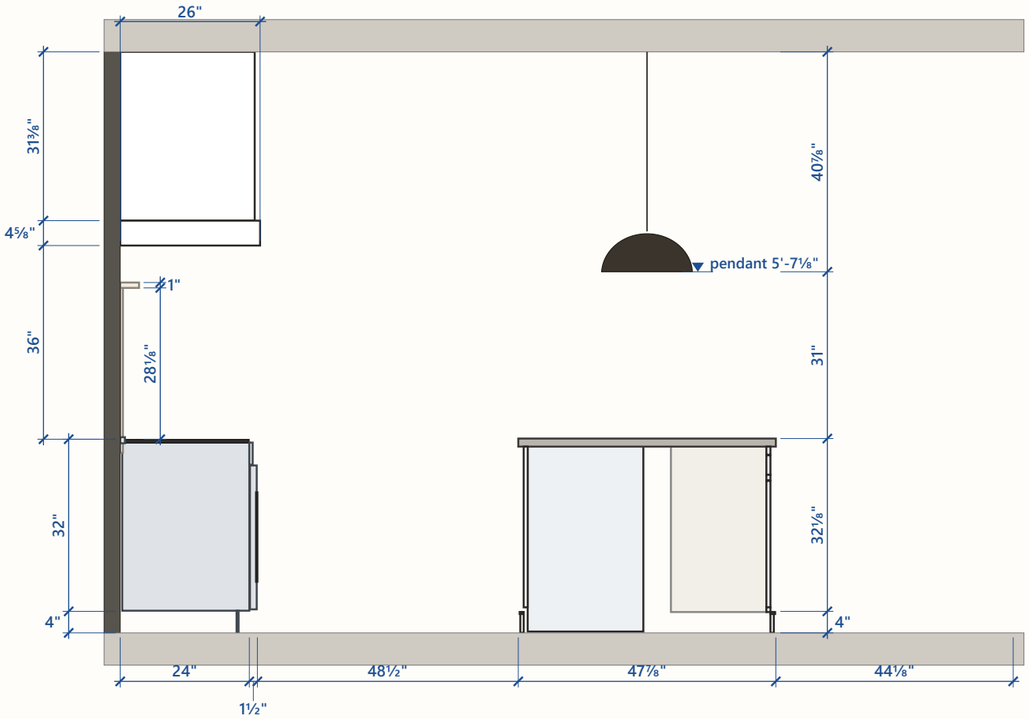

A SECTION A — THROUGH RANGE, HOOD & DISHWASHER

≈ 3/8" = 1'-0" · cut elements only

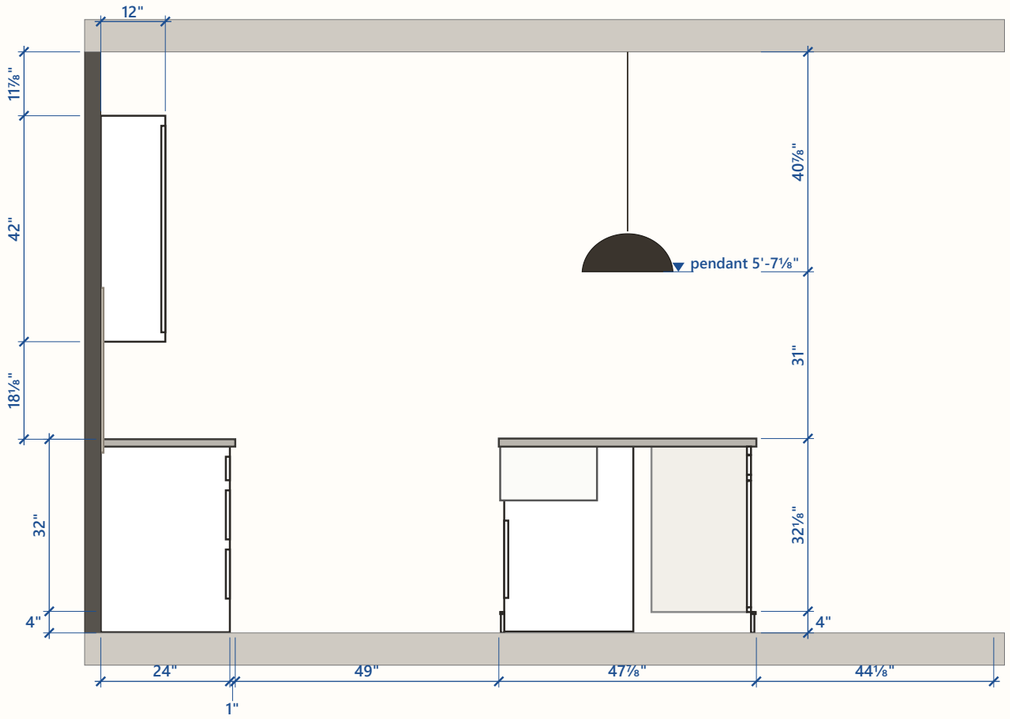

B SECTION B — THROUGH SINK BASE & 30" UPPER

≈ 3/8" = 1'-0" · cut 13" right of sink ℄, through pendant 2

Clearances (model):

- Aisle between back counter edge and island top: 49".
- Fridge panels to island top: 46" (fridge door swings into this aisle).
- Island seating side to Breakfast/porch wall: 44⅛" (Breakfast end).
- Island right end to hall wall: 48¼".

Pendants: 17" domes, bottom 67⅛" AFF = 31" above the island top.
Range hood: bottom 72" AFF, 36" above the cooktop; confirm the hood insert maker's required mounting height and duct route.

KITCHEN REMODEL

Jane's Kitchen

Cabinet & layout dimensions

Issued 2026-10-21

For coordination — not for construction


NOTES

Dimensions from the design model.
Verify all dimensions in field.
Do not scale drawings.
Heights are above finished floor.
Plan dims from inside face of
left wall / back wall.

SECTIONS

Depths, clearances and heights through the range and the sink

A-301

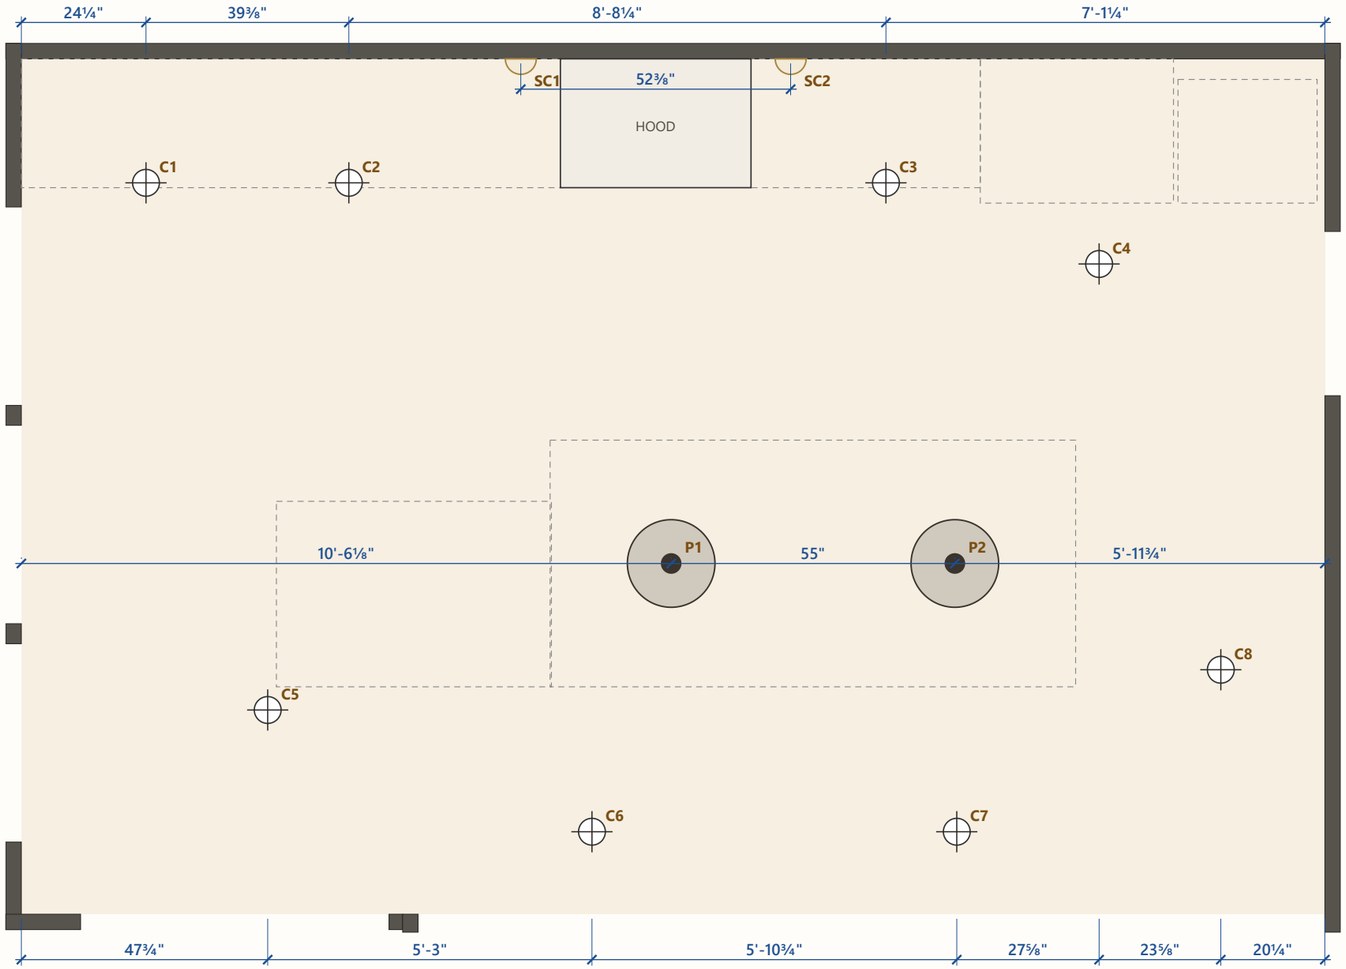

1 **REFLECTED CEILING PLAN**

≈ 3/8" = 1'-0" · ceiling 9'-0" · counters shown dashed for reference

FIXTURE LOCATIONS

Tag	Fixture	X from left wall	From back wall	Height
C1	Recessed downlight (≈5" tri…	24¼"	24"	in ceiling
C2	Recessed downlight (≈5" tri…	5'-3½"	24"	in ceiling
C3	Recessed downlight (≈5" tri…	13'-11¾"	24"	in ceiling
C4	Recessed downlight (≈5" tri…	17'-5¼"	39¾"	in ceiling
C5	Recessed downlight (≈5" tri…	47¾"	10'-6⅜"	in ceiling
C6	Recessed downlight (≈5" tri…	9'-2¾"	12'-6"	in ceiling
C7	Recessed downlight (≈5" tri…	15'-1½"	12'-6"	in ceiling
C8	Recessed downlight (≈5" tri…	19'-4¾"	9'-10½"	in ceiling
P1	17" dome pendant, dark bron…	10'-6⅛"	8'-2"	bottom 5'-7⅛" AFF
P2	17" dome pendant, dark bron…	15'-1¼"	8'-2"	bottom 5'-7⅛" AFF
SC1	Wall sconce, brass + alabas…	8'-1"	0"	center 76¾" AFF
SC2	Wall sconce, brass + alabas…	12'-5¼"	0"	center 76¾" AFF

Locations are fixture centers. Downlights C1–C3 over the counters sit 24" out from the back wall; adjust to the joists. Hood insert has 2 integral lights. No under-cabinet lights in the design. Switching, outlets and circuits are not in the model — lay these out to code (GFCI/AFCI, island receptacle, 240 V range).

KITCHEN REMODEL

Jane's Kitchen

Cabinet & layout dimensions

Issued 2026-10-21

For coordination — not for construction

NOTES

Dimensions from the design model.
Verify all dimensions in field.
Do not scale drawings.
Heights are above finished floor.
Plan dims from inside face of
left wall / back wall.

LIGHTING / REFLECTED CEILING PLAN

Fixture locations from the design model

A-401

CABINET SCHEDULE

Tag	Description	Location	Width	Height	Depth	Bottom AFF	Fronts / hardware
B1	Base — drawer over 2 doors	Back wall, under hutch	33"	34½"	24"	⅛"	12" bar pull on drawer, knobs at meeting stiles
B2	Base — 3 drawers	Back wall	36"	34½"	24"	⅛"	12" bar pulls
B3	Base — 3 drawers	Back wall, left of range	36"	34½"	24"	⅛"	12" bar pulls
B4	Base — narrow pull-out (slab front)	Back wall, right of range	9"	34½"	24"	⅛"	slab front, no hardware (verify)
B5	Base — 3 drawers	Back wall, left of fridge	36"	34½"	24"	⅛"	12" bar pulls
H1	Countertop hutch — 2 doors, sits on counter	Back wall, Breakfast end	33"	5'-⅛"	15"	36"	knobs low at meeting stiles
U1	Wall cabinet — 2 doors	Back wall	36"	42"	12"	54⅛"	knobs 3" up from bottom rail
U2	Wall cabinet — 1 door	Back wall, left of hood	21"	42"	12"	54⅛"	knob
U3	Wall cabinet — 2 doors	Back wall, right of hood	30"	42"	12"	54⅛"	knobs
U4	Wall cabinet over fridge — 2 doors	Above refrigerator	38⅞"	11⅜"	12"	7'-¾"	2" rails, knobs at center
T1	Tall pantry — 2 tall doors + 2 upper doors	Back wall, hall end	27"	7'-8¼"	24"	3⅞"	knobs at 39" and 77" AFF
I1	Island base — 1 door	Island, working side	18"	34½"	24"	¼"	knob
I2	Island sink base — 2 doors, 30" apron-front sink	Island, working side	33"	34½"	24¾"	¼"	knobs (doors below apron sink)
I3	Island base — double trash pull-out	Island, working side	21"	34½"	24"	⅛"	12" bar pull at top
S1	Island seating-side storage — tall door	Island, living-room side	12¾"	30⅝"	17¾"	4"	knob
S2	Island seating-side storage — small drawer over door	Island, living-room side	14⅝"	30⅝"	17¾"	4"	bail pulls on small drawers, bars + knobs on bank
S3	Island seating-side storage — 3-drawer bank	Island, living-room side	31¾"	30⅝"	17¾"	4"	bail pulls on small drawers, bars + knobs on bank
S4	Island seating-side storage — small drawer over door	Island, living-room side	14⅝"	30⅝"	17¾"	4"	bail pulls on small drawers, bars + knobs on bank
S5	Island seating-side storage — tall door	Island, living-room side	12¾"	30⅝"	17¾"	4"	knob

APPLIANCES & FIXTURES

Tag	Model	Type	Opening in model (W × H × D)	Notes for the GC
RANGE	Bosch HIS5657U	36" freestanding induction range	36" between cabinets, counter 36"	208/240 V, 40 A (50 A rec.), HARDWIRED to a junction box; ℄ 10'-3⅛" from left wall
REF	Thermador T36IB100SP	36" built-in, panel-ready, single door over freezer drawer	36" × 7'-0" × 28"	Spec cutout 84 × 36 × 25 ✓; 120 V/15 A outlet + cold water in the adjacent cabinet; ¾" panels
DW	Thermador Sapphire DWHD660EPR	24" panel-ready (fully integrated)	24" between cabinets, under 34⅝" top	Spec 24" min. ✓; 120 V/12 A, hot water, drain to sink base; push-to-open panel, NO handle
SINK	Rohl 30" fireclay apron-front	Single bowl, apron front, in 33" sink base I2	30" × 18", apron top at counter	Sink ℄ 13'-8½" from left wall; stone notched around apron
HOOD	Plaster hood + stainless insert	3 baffle filters, 2 lights	38½" wide band, bottom 72" AFF	Select insert & blower; duct route and make-up air per code / insert maker
FAUCET	Brass gooseneck, side lever	Single hole	behind sink ℄	Hole at sink ℄, ≈1¾" behind bowl

Finishes (design intent): perimeter + island cabinets painted warm cream, inset shaker, 3" stiles/rails; black stone counters; cream marble slab backsplash with gold/brown veining; matte black hardware; brass faucet; light white-oak floor with planks running parallel to the counters and island.

KITCHEN REMODEL

Jane's Kitchen

Cabinet & layout dimensions

Issued 2026-10-21

For coordination — not for construction

NOTES

Dimensions from the design model.
Verify all dimensions in field.
Do not scale drawings.
Heights are above finished floor.
Plan dims from inside face of
left wall / back wall.

CABINET & APPLIANCE SCHEDULES

Sizes from the design model — confirm
with shop drawings

A-501

APPLIANCE REQUIREMENTS

From the UAKC spec package, invoice 255075, v2.2 (Oct 20, 2026). ✓ = the design meets the spec. Always confirm against the installation guide in the box.

REF — Thermador T36IB100SP

36" built-in bottom-freezer refrigerator, panel-ready

CUTOUT & CLEARANCES	Spec	Design	
Cutout width	36"	36"	✓
Cutout height	84"	7'-0"	✓
Cutout depth	≥ 25"	28"	✓
Finished side returns	flush, ≥ 4" deep	28"	✓

POWER, WATER & DRAIN

- 120 V, 60 Hz, 15 A; 3-prong plug, 118" cord
- Outlet in an ADJACENT cabinet (preferred); behind the unit only if it can be switched off at the breaker
- Cold water line, 29–116 psi, reachable from the next cabinet
- Lines route through the recess at the base of the unit

PANELS & INSTALL

- Custom panels ¾" thick (clearances assume ¾")
- Door panel max 121 lb; drawer panels max 66 lb / 103 lb
- Door swing 115° max, 90° min to reach every drawer
- Unit height adjusts 83 9/16–85½" (83⅞" for an 84" niche)

RANGE — Bosch HIS5657U

36" 500 Series freestanding induction range

CUTOUT & CLEARANCES	Spec	Design	
Cutout width	36"	36"	✓
Counter depth	≥ 25"	25"	✓
Cooktop to hood bottom	≥ 30"	36"	✓
Counter to upper cabinets	≥ 18"	18⅛"	✓
Upper cabinet depth	≤ 13"	12"	✓

POWER, WATER & DRAIN

- 208/240 V, 60 Hz; 40 A breaker (50 A recommended), 8,400 W
- HARDWIRED — no cord: junction box, not a receptacle
- Anti-tip bracket (included) must be installed
- Zero clearance to the side cabinets below the counter

PANELS & INSTALL

- Freestanding, stainless; 35 15/16" W, 26 19/64" deep incl. bull nose
- Height adjusts 35¾–36¾" — set flush with the 36" counter

DW — Thermador Sapphire DWHD660EPR

24" custom-panel dishwasher

CUTOUT & CLEARANCES	Spec	Design	
Cutout width	24" min. (23⅝–24¼)	24"	✓
Cutout height (to underside of top)	33⅞–35"	34⅝"	✓
Cutout depth	24"	24"	✓
Toe kick height	3⅝–7½"	4"	✓

POWER, WATER & DRAIN

- 120 V, 60 Hz, 12 A; 67" cord (reaches 45" left / 56" right of the unit's corner)
- Hot water ≤ 140°F, ≥ 14 psi
- Drain hose 90½" — run to the sink base I2 (extension SGZ1010UC if needed)
- Optional install kit SMZ3IN1UC (junction box, 90° elbow, supply hose)

PANELS & INSTALL

- Custom panel 23⅛–23⅜" W (24" allowed by cabinet design) × 27½–30⅛" H × ⅝–⅞" thick, 11–18 lb
- PUSH-TO-OPEN — no handle on the panel
- Panel height measured from the underside of the countertop

DESIGN CHANGES MADE FOR THESE SPECS (Oct 21, 2026)

- Refrigerator opening reduced from 37" to 36": ¾" end panels each side, plus a ⅞" filler between the right panel and the pantry.
- Dishwasher opening widened from 23¾" to 24": the 18" door base I1 slides ¼" toward the island end (it had ⅞" spare).
- Dishwasher panel has no handle — the Sapphire opens with a push.

KITCHEN REMODEL

Jane's Kitchen

Cabinet & layout dimensions

Issued 2026-10-21

For coordination — not for construction

NOTES

Dimensions from the design model.
Verify all dimensions in field.
Do not scale drawings.
Heights are above finished floor.
Plan dims from inside face of left wall / back wall.

APPLIANCE REQUIREMENTS

Manufacturer specs checked against the design

A-502