
Bathroom 2

Hall bath renovation · 5'-0" × 8'-11" with walk-in shower

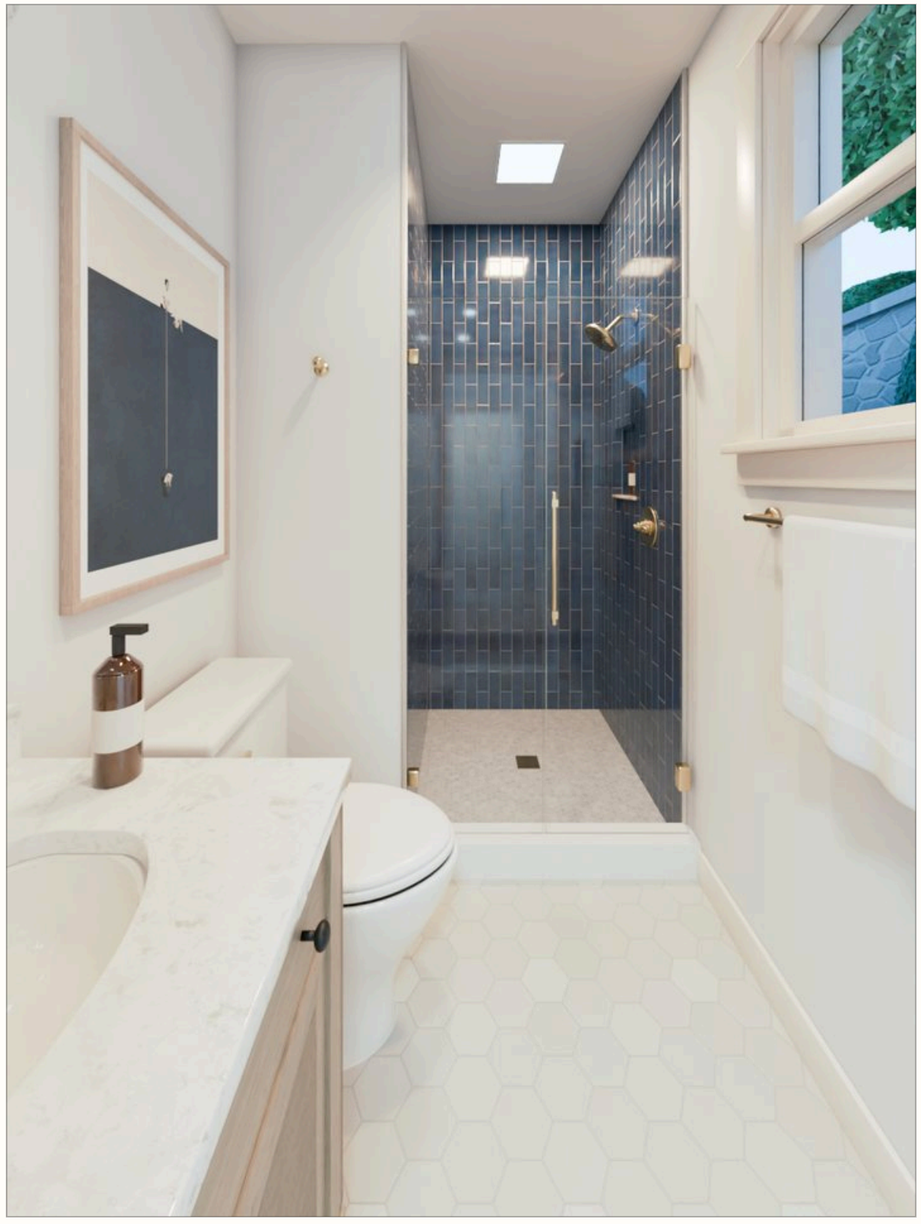

Design rendering from the doorway (Blender / Cycles). Finishes are representative.

DESIGN INTENT

Classic bath with a weathered-fir vanity with woven-cane doors (Carrara marble top, undermount oval basin), a white matte 4×5 hexagon porcelain floor with light warm gray grout, a solid white slab curb, Benjamin Moore Chantilly Lace walls, white painted baseboards, under a bright white ceiling, and a walk-in shower in muted navy glossy 2½×9 porcelain laid vertically in a staggered (vertical running bond) pattern with tight light joints, floor to ceiling, over a 1-inch honed White Carrara hexagon mosaic floor, behind clear frameless glass. Shower trim and vanity faucet Delta Saylor in Champagne Bronze; all other hardware Champagne Bronze to match.

GENERAL NOTES

1. Dimensions come from the design model (built from the owner's SketchUp file). Field-verify every dimension before ordering or cutting; the room has not been field-measured for this set.
2. Plan dimensions are to finished wall faces. Heights are above finished floor (AFF).
3. Fixture sizes are the specified products' published dimensions; confirm rough-ins against the manufacturer spec sheets on site.
4. Toilet: 12" rough-in, 15⅞" from the shower jog wall to centerline and 15" from the 30" vanity's side (the 15" code minimum, IRC P2705 / IPC 405.3.1) -- do not widen the vanity.
5. Shower: provide waterproof membrane on all wet walls and the pan, sloped to the drain. Niche is recessed into the window-side wall, lined in the navy 2×6 with a veined marble shelf.
6. Shower tile set-out: 2×6 mosaic sheets, horizontal running bond with a half-tile stagger, no liner; keep the sheet joints invisible. Start a full course on the curb line, centre the head joints on the back wall so the corner cuts match; cut row at the ceiling. Handmade-look tile: expect varied edges and glaze.
7. GFCI receptacle is required by code but not modeled — locate with the electrician. Exhaust: L-2 fan/light in the shower. MR-1 mirror has no power (no box needed).
8. Owner direction: no plant or vase on the vanity; vanity faucet Delta Saylor, Champagne Bronze.

SHEET INDEX

A-001	Cover, notes & index
A-101	Floor plan — dimensioned
A-201	Elevations — vanity / toilet wall & door wall
A-202	Elevations — window wall & shower
A-401	Reflected ceiling & lighting plan
A-501	Fixture & finish schedule

BATHROOM REMODEL

Bathroom 2

Layout, fixtures & finishes

Issued 2026-11-12

For coordination — not for construction


NOTES

Dimensions from the design model, built from the owner's SketchUp.
Verify all dimensions in field.
Do not scale drawings.
Heights are above finished floor.
Plan dims to finished wall faces.

COVER, NOTES & INDEX

Design intent, general notes and sheet index

A-001

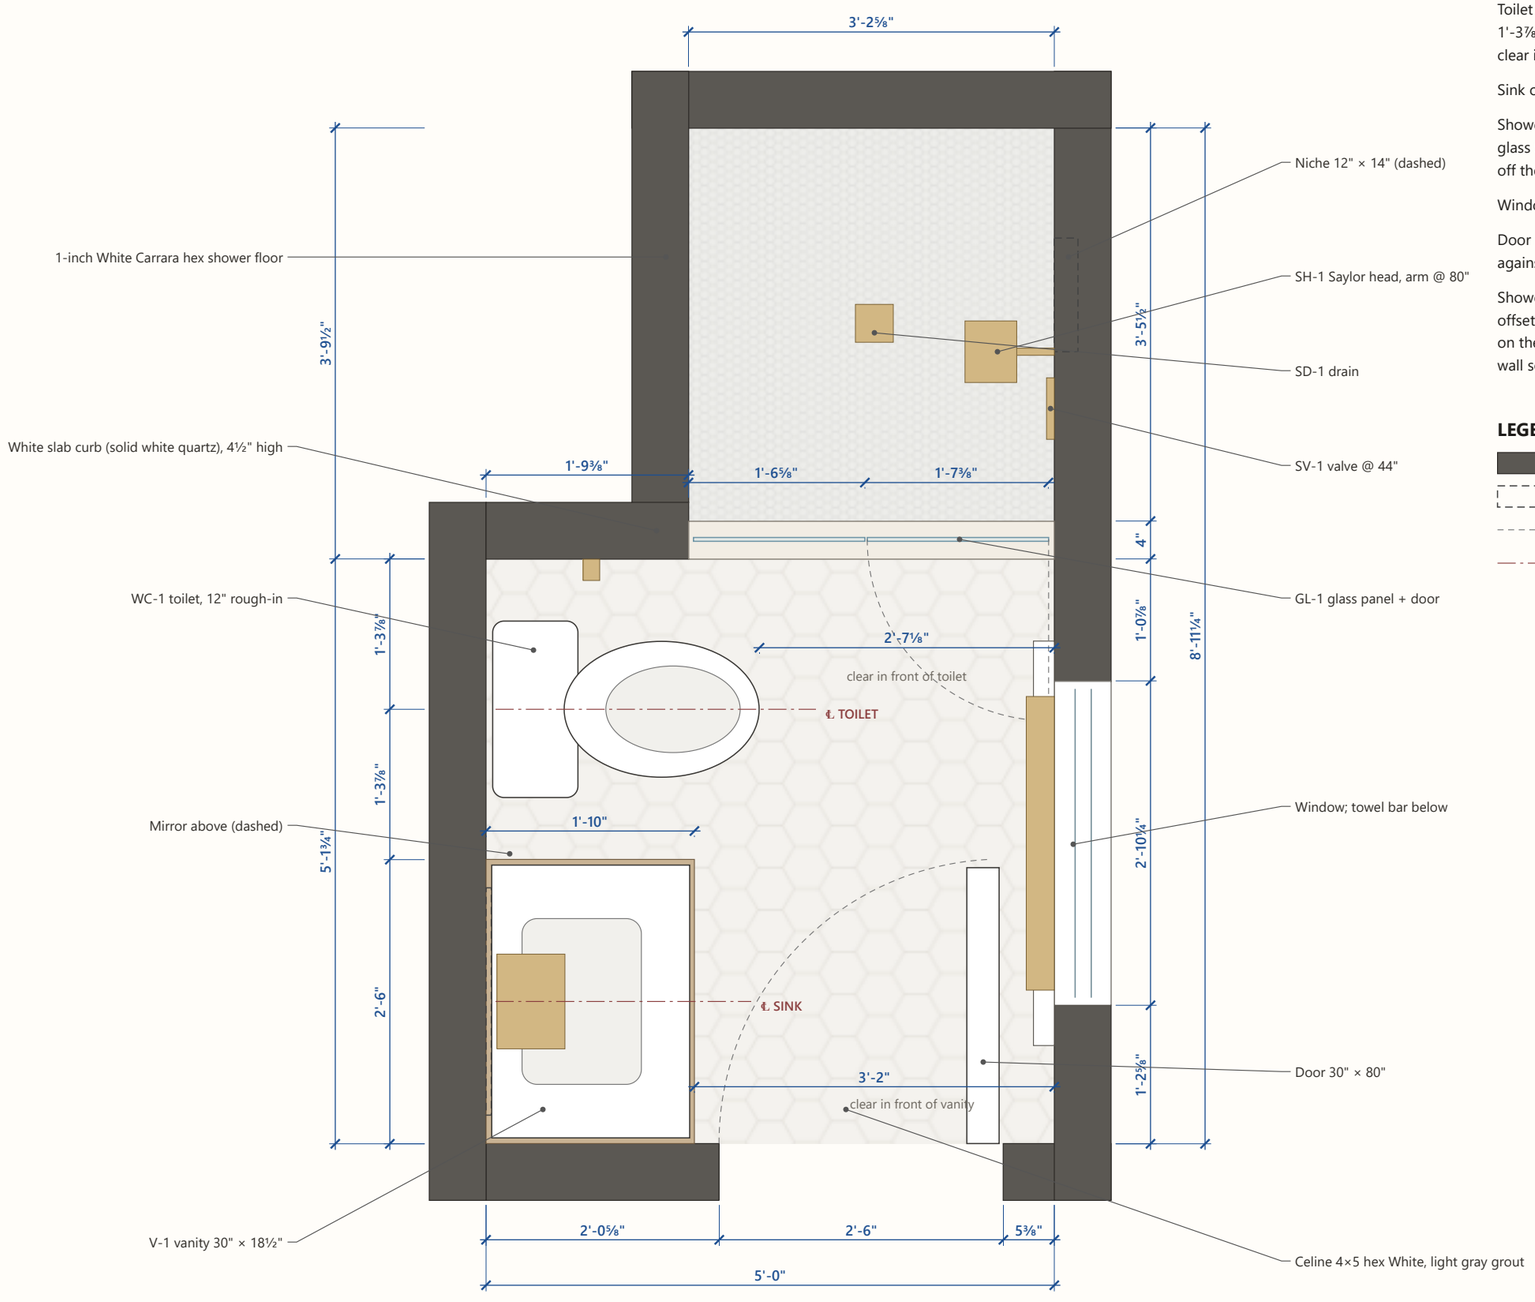

1 **FLOOR PLAN**

3/4" = 1'-0" on 11×17 · north = toward the shower

PLAN NOTES

Toilet centerline 1'-3⅜" from the vanity side and 1'-3⅜" from the jog wall (code min. 15"). 2'-7⅛" clear in front (min. 21").

Sink centerline 1'-3" from the door wall.

Shower inside 3'-2⅝" × 3'-5½" beyond a 4" curb; glass 5'-11½" tall on the curb, door 1'-7⅛" hinged off the window-side wall.

Window rough opening 2'-10¼" wide, sill 4'-6⅝" AFF.

Door hinged on the window side; it opens flat against the window-side wall.

Shower walls: Zenia 2½×9 set vertically, each column offset half a tile from the next; start full tiles on the curb line and centre a column on the back wall so the corner cuts match.

LEGEND

- Wall (existing / new, 6")
- Above / recessed (mirror, niche)
- Door swing
- Centerline

BATHROOM REMODEL

Bathroom 2

Layout, fixtures & finishes

Issued 2026-11-12

For coordination — not for construction


NOTES

Dimensions from the design model, built from the owner's SketchUp.
Verify all dimensions in field.
Do not scale drawings.
Heights are above finished floor.
Plan dims to finished wall faces.

FLOOR PLAN — DIMENSIONED


Room, fixture locations, clearances and rough-in centerlines

A-101

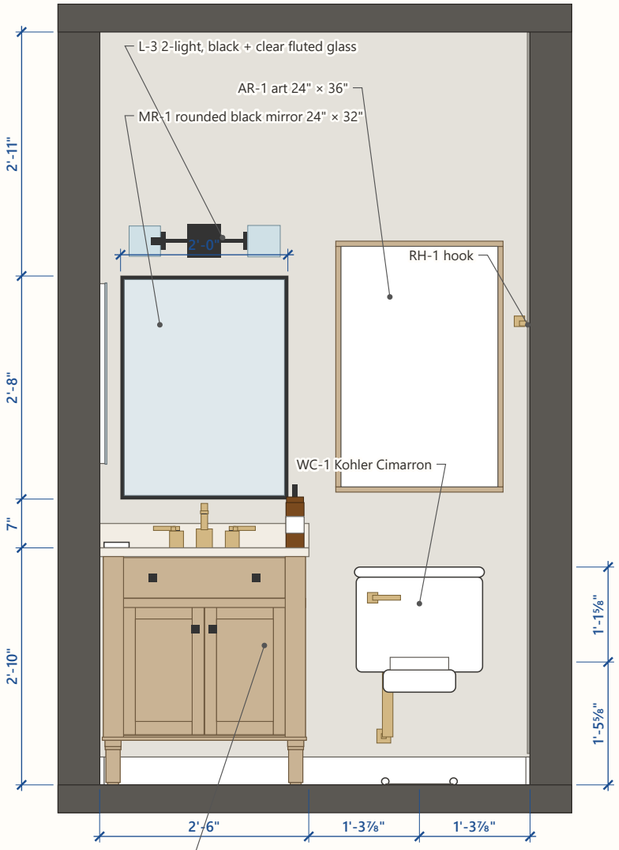

1 **VANITY & TOILET WALL**

1/2" = 1'-0" on 11×17 · looking west

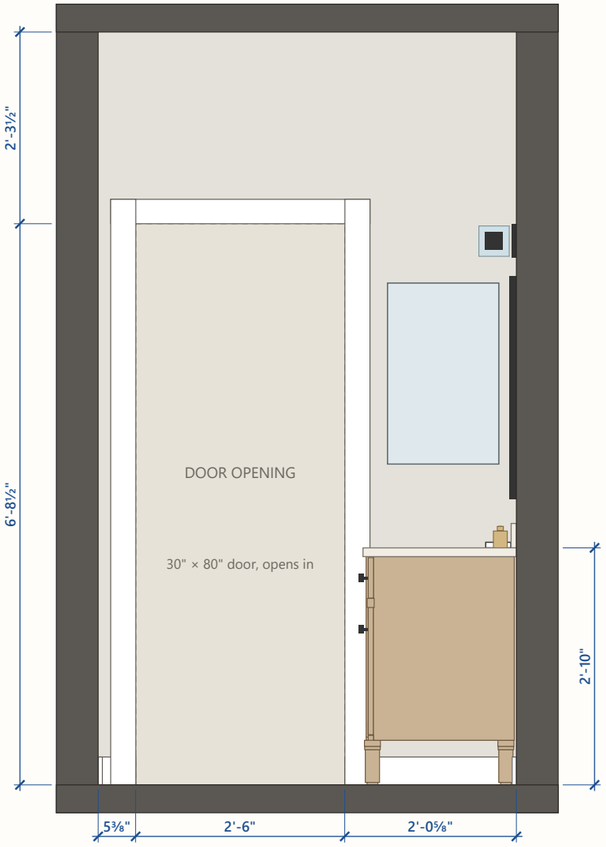

2 **DOOR WALL**

1/2" = 1'-0" on 11×17 · looking south

BATHROOM REMODEL

Bathroom 2

Layout, fixtures & finishes

Issued 2026-11-12

For coordination — not for construction


NOTES

Dimensions from the design model, built from the owner's SketchUp.
Verify all dimensions in field.
Do not scale drawings.
Heights are above finished floor.
Plan dims to finished wall faces.

INTERIOR ELEVATIONS


Vanity & toilet wall and door wall

A-201

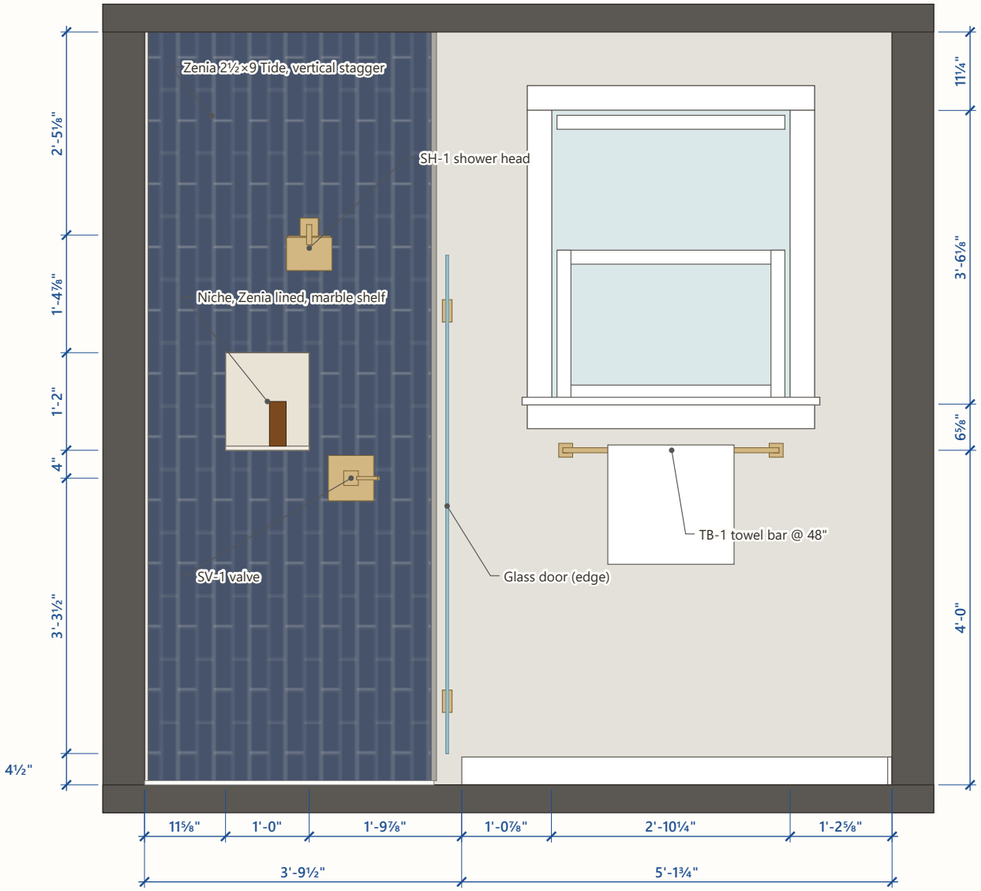

3 **WINDOW WALL**

1/2" = 1'-0" on 11×17 · looking east

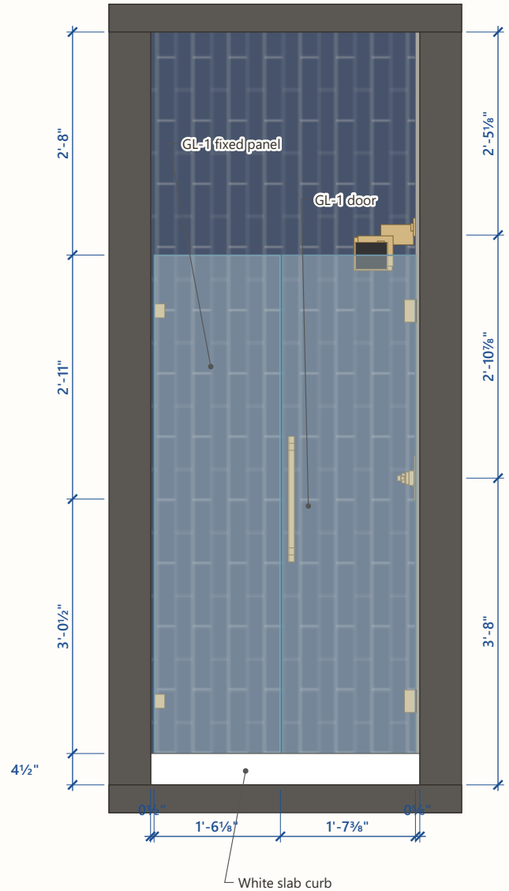

4 **SHOWER**

1/2" = 1'-0" on 11×17 · looking north, through the glass

BATHROOM REMODEL

Bathroom 2

Layout, fixtures & finishes

Issued 2026-11-12

For coordination — not for construction


NOTES

Dimensions from the design model, built from the owner's SketchUp.
Verify all dimensions in field.
Do not scale drawings.
Heights are above finished floor.
Plan dims to finished wall faces.

INTERIOR ELEVATIONS

Window wall (with shower side wall) and shower back wall

A-202

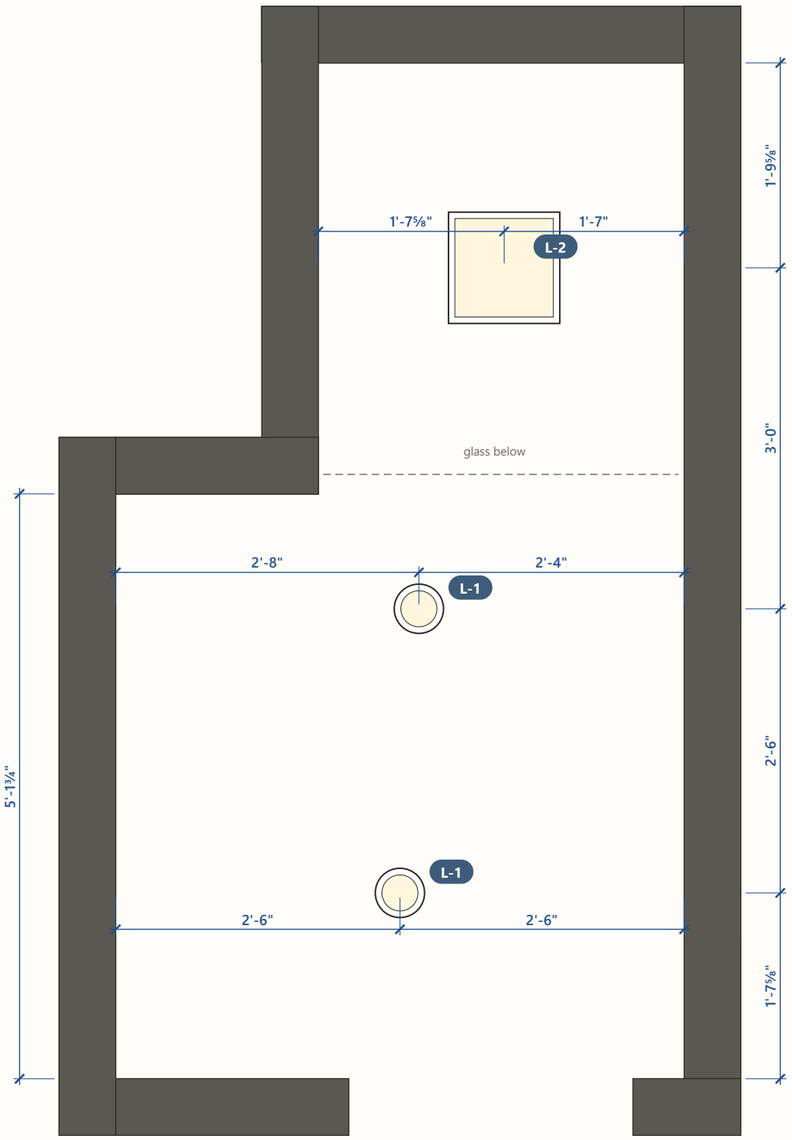

1 **REFLECTED CEILING PLAN**

3/4" = 1'-0" on 11×17 · ceiling 9'-0" AFF

LIGHTING SCHEDULE

L-1	× 2	4" recessed downlight, white trim, 2700–3000 K, dimmable
L-2	× 1	Shower fan/light: Delta Breez Integrity ITG100ELED, 100 CFM, 1.5 sone, dimmable edge-lit LED panel 1000 lm 3000 K; ~11¾" sq. grille, 4" duct (wet-location listed; confirm with spec sheet)
L-3	× 1	Vanity light over the mirror, as the owner's inspiration photo: 2-light bar in matte black -- round backplate, straight arm, a black cup at each end holding a clear fluted (ribbed) glass shade pointing outward, exposed globe bulbs (2700 K); ~23" wide, centred over the mirror, 78" AFF to centre; owner to pick the exact fixture
EF-1	× —	Exhaust fan: provided by L-2 in the shower; duct to exterior

NOTES

Switch at the door, latch side (window wall), 48" AFF: L-1/L-2 on a dimmer; L-3 sconce on its own dimmer; L-2 fan on a separate switch or timer.

L-2 over the shower must be listed for wet locations (shower use) and GFCI protected per code; confirm the joist bay and the 4" duct run to the exterior.

BATHROOM REMODEL

Bathroom 2

Layout, fixtures & finishes

Issued 2026-11-12

For coordination — not for construction

NOTES

Dimensions from the design model, built from the owner's SketchUp.
Verify all dimensions in field.
Do not scale drawings.
Heights are above finished floor.
Plan dims to finished wall faces.

REFLECTED CEILING & LIGHTING PLAN

Fixture locations from the design model

A-401

FIXTURES & EQUIPMENT

Tag	Item	Product	Size / finish / location
V-1	Vanity	Ari Bath Annie 30" Bathroom Vanity, Weathered Fir (owner; 30" keeps the toilet clearance)	30" W × 22" D × 34½" H; solid wood, plain solid sides, slab tilt-out top drawer, 2 doors with woven-cane panels, tapered legs, ashy weathered-fir finish; Italian Carrara marble top, pre-drilled 8" widespread; matte black round knobs as supplied, 2 on the drawer + 2 on the doors; 3½" Carrara backsplash. 22" deep: check the walkway to the door
F-1	Lavatory faucet	Delta Saylor two-handle widespread 3536-CZMPU-DST, Champagne Bronze; 6⅜" high, 5.56" reach, lever handles	8" spread on the top's 3 holes; matching Champagne Bronze pop-up drain (included); 2½" min. to backsplash
WC-1	Toilet	Kohler Cimarron Comfort Height elongated, 2-piece	12" rough-in; 28-13/16" D, 18-5/8" W tank, 16½" rim, 31¼" H; left-hand lever
SV-1	Shower valve trim	Delta Saylor Monitor 14 Series T14235-CZ (single-function), 6½" round plate, lever handle, Champagne Bronze	On a MultiChoice R10000-UNBXHF rough valve (sold separately); valve center 44" AFF on the window-side wall
SH-1	Shower head	Delta Saylor 6½" 5-spray head on a 5½" arm with round flange (part of T14235-CZ), Champagne Bronze	Arm outlet 80" AFF above the valve line; no handshower
SD-1	Shower drain	4" square tile-in drain cover	Champagne Bronze; at shower center
GL-1	Shower glass	Frameless ⅜" clear (low-iron) fixed panel + hinged door with pull bar	Panel 1'-6⅛", door 1'-7⅛"; 5'-11½" tall on the curb; Champagne Bronze clamps & hinges
MC-1	Medicine cabinet	Frameless mirrored medicine cabinet, recessed (as existing, owner photo)	16" W × 26" H, ~1" proud of the wall; door wall between the vanity corner and the door casing, 46" – 72" AFF, top aligned with the MR-1 mirror (9' ceiling); provide blocking / check the stud bay
MR-1	Mirror	Rounded-rectangle mirror in a slim matte black metal frame (owner's inspiration photo), ~5" corner radius	24" W × 32" H; centred on the faucet, bottom 41" AFF, top 73" AFF; D-rings / French cleat on the stud wall
TB-1	Towel bar	30" towel bar	Champagne Bronze; under the window at 48" AFF
RH-1	Robe hook	Single hook	Champagne Bronze; jog wall at 66" AFF
AR-1	Art	Owner's framed print (24" × 36"), thin natural-oak frame	Centered over the toilet, bottom 42" AFF (level with the mirror bottom)

FINISHES

Surface	Material	Where / notes
Floor	Bedrosians Celine 4" × 5" Hexagon Matte Porcelain, White (100003132; actual 4" × 4-9/16")	Main room and under the vanity, to the curb; 1/8" light warm gray grout (owner); V4 shade variation -- blend from several cartons
Shower walls	Bedrosians Zenia 2.5" × 9" Porcelain Floor & Wall Tile, Tide, gloss (DECZENTID259G)	All three shower walls, pan to ceiling, VERTICAL running bond (long side plumb, alternate columns offset half a tile, as the owner's photo); tight ~1/16" light warm white grout; no liner; niche lined to match; metal edge profile in a brass / bronze finish on exposed edges
Shower floor	1" honed White Carrara marble hexagon mosaic on 12" sheets (Bedrosians stocks 3" only -- owner to pick the product)	Shower floor, sloped to the drain; 1/16" white grout; marble: seal before and after grouting, pH-neutral cleaner; small chips and many joints give good grip underfoot
Shower curb	Solid white slab (white quartz look), polished, one piece	4" × 4½" high, full width under the glass; slope the top 1/4" toward the shower
Niche shelf	Grey-veined white marble (Arabescato / Calacatta Viola look, per the owner's inspiration photo), polished -- owner to pick the slab	Shower niche
Walls	Benjamin Moore Chantilly Lace OC-65, matte (bath rated); trim stays white semi-gloss	All non-tiled walls
Ceiling	Bright flat white paint, bath rated (a shade whiter than the walls)	9'-0" AFF
Baseboard	Painted wood (MDF or poplar) baseboard, 4" with a simple eased / small-ogee top, white semi-gloss to match the trim	All walls; on the jog wall it runs to the shower corner
Trim	Semi-gloss white; door & window casings	Match existing profiles
Hardware	Champagne Bronze (owner), matching the Delta Saylor F-1 / SV-1 / SH-1; vanity knobs matte black (as the Annie ships) to go with the black L-3 and MR-1 frame	SD-1; TB-1, RH-1; glass hardware; toilet lever; door hardware. Vanity knobs: matte black

BATHROOM REMODEL

Bathroom 2

Layout, fixtures & finishes

Issued 2026-11-12

For coordination — not for construction

NOTES

Dimensions from the design model, built from the owner's SketchUp.
Verify all dimensions in field.
Do not scale drawings.
Heights are above finished floor.
Plan dims to finished wall faces.

FIXTURE & FINISH SCHEDULE

Products and finishes as designed — confirm availability and lead times

A-501