
Simon's Bathroom

Hall bath renovation · 5'-0" × 8'-11" with walk-in shower

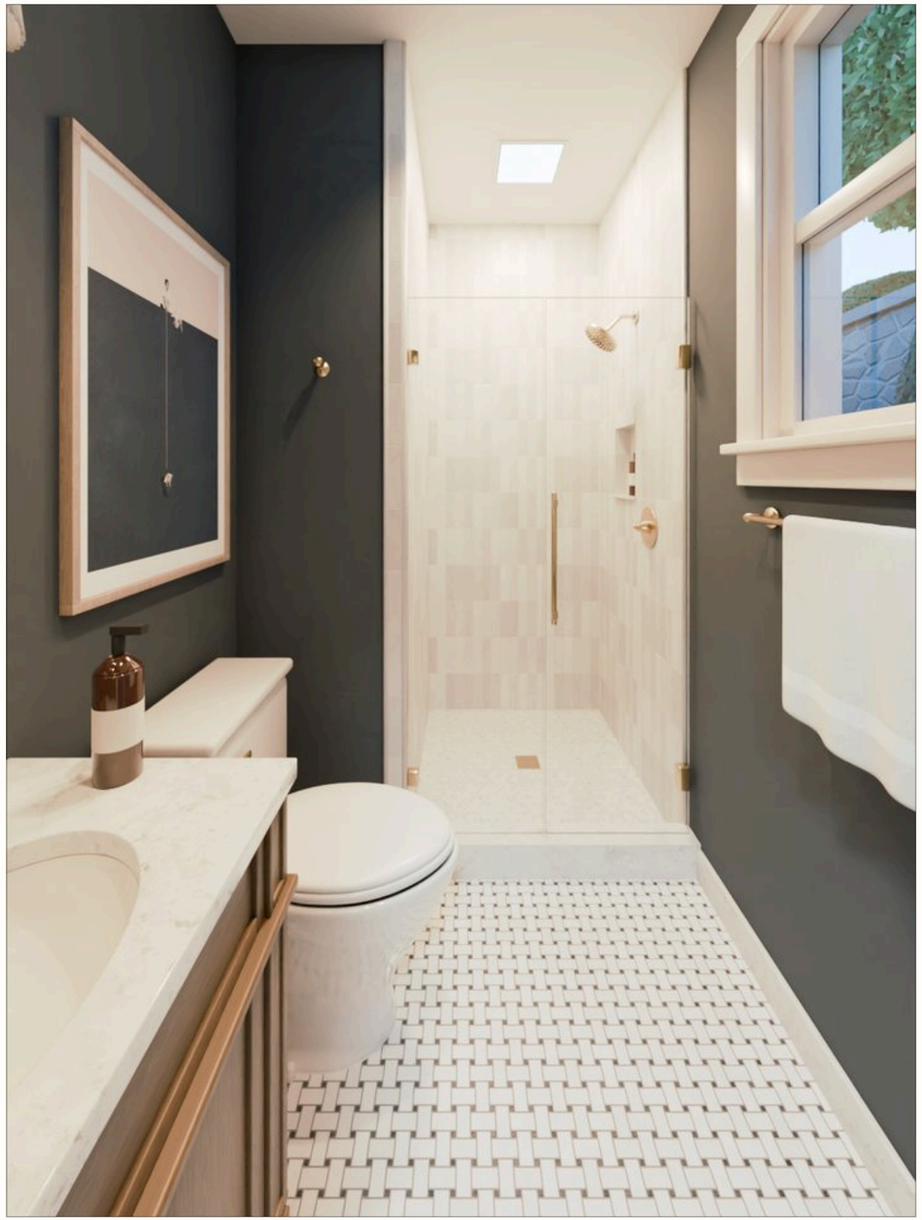

Design rendering from the doorway (Blender / Cycles). Finishes are representative.

DESIGN INTENT

Classic bath with a traditional brown-ash vanity (Carrara marble top, undermount oval basin), marble white marble basketweave floor, Hale Navy walls under a bright white ceiling, and a walk-in shower in honed Oriental White marble 2×8, vertical stack floor to ceiling, over a matching Oriental White 1" penny round floor, behind clear frameless glass. Shower trim and vanity faucet Delta Saylor in Champagne Bronze; all other hardware Champagne Bronze to match.

GENERAL NOTES

1. Dimensions come from the design model (built from the owner's SketchUp file). Field-verify every dimension before ordering or cutting; the room has not been field-measured for this set.
2. Plan dimensions are to finished wall faces. Heights are above finished floor (AFF).
3. Fixture sizes are the specified products' published dimensions; confirm rough-ins against the manufacturer spec sheets on site.
4. Toilet: 12" rough-in, 15⅞" from the shower jog wall to centerline and 15" from the 30" vanity's side (the 15" code minimum, IRC P2705 / IPC 405.3.1) -- do not widen the vanity.
5. Shower: provide waterproof membrane on all wet walls and the pan, sloped to the drain. Niche is recessed into the window-side wall, lined in the Monet 2×8 with a marble sill.
6. Shower tile set-out: 2×8 marble upright in a vertical stack (joints aligned both ways), no liner. Back wall centred with equal 1¾" end cuts; side walls centred with equal 1½" cuts; first joint on the pan, full 8" rows up, cut row at the ceiling.
7. GFCI receptacle is required by code but not modeled — locate with the electrician. Exhaust: L-2 fan/light in the shower. MR-1 mirror has no power (no box needed).
8. Owner direction: no plant or vase on the vanity; vanity faucet Delta Saylor, Champagne Bronze.

SHEET INDEX

A-001	Cover, notes & index
A-101	Floor plan — dimensioned
A-201	Elevations — vanity / toilet wall & door wall
A-202	Elevations — window wall & shower
A-401	Reflected ceiling & lighting plan
A-501	Fixture & finish schedule

BATHROOM REMODEL

Simon's Bathroom

Layout, fixtures & finishes

Issued 2026-11-04

For coordination — not for construction


NOTES

Dimensions from the design model, built from the owner's SketchUp.
Verify all dimensions in field.
Do not scale drawings.
Heights are above finished floor.
Plan dims to finished wall faces.

COVER, NOTES & INDEX

Design intent, general notes and sheet index

A-001

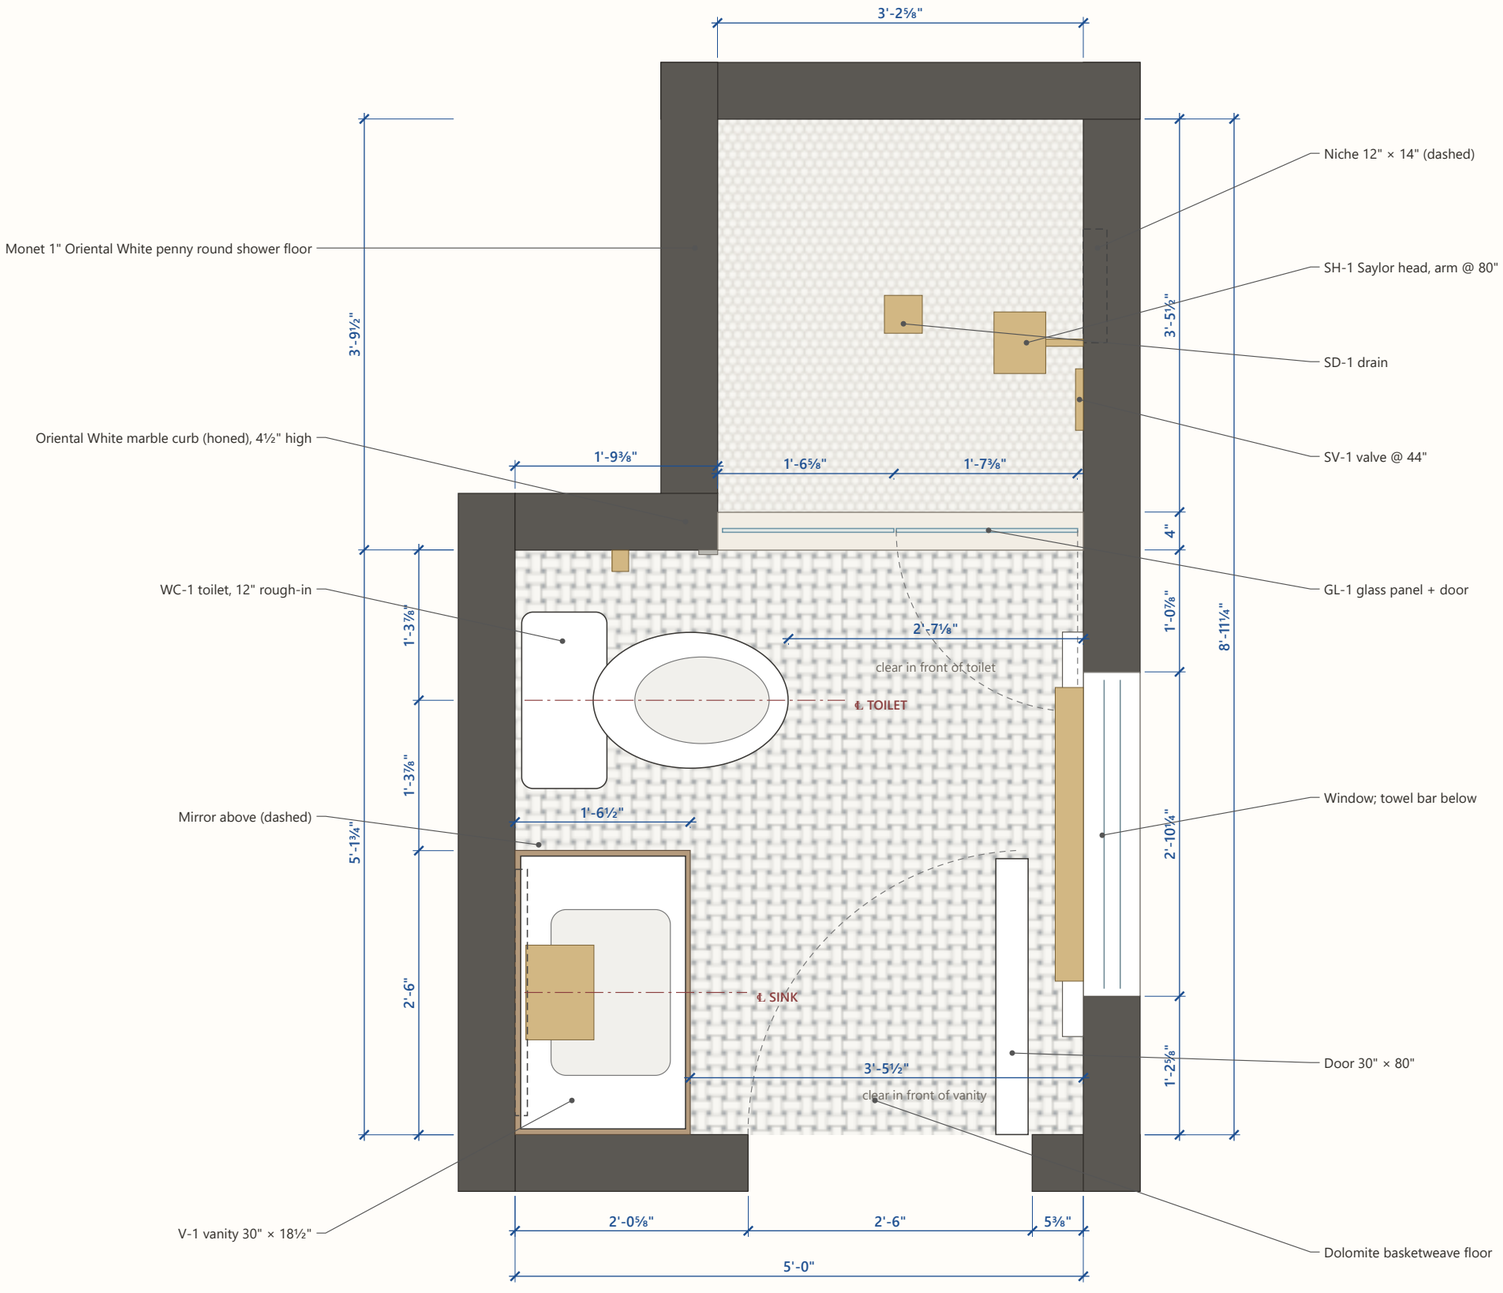

PLAN NOTES

Toilet centerline 1'-3⅞" from the vanity side and 1'-3⅞" from the jog wall (code min. 15"). 2'-7⅛" clear in front (min. 21").

Sink centerline 1'-3" from the door wall.

Shower inside 3'-2⅝" × 3'-5½" beyond a 4" curb; glass 5'-11½" tall on the curb, door 1'-7⅛" hinged off the window-side wall.

Window rough opening 2'-10¼" wide, sill 4'-6⅝" AFF.

Door hinged on the window side; it opens flat against the window-side wall.

Floor tile runs under the vanity and to the curb; the shower floor is the Monet penny round, sloped to the drain.

LEGEND

- Wall (existing / new, 6")
- Above / recessed (mirror, niche)
- Door swing
- Centerline

1 FLOOR PLAN

3/4" = 1'-0" on 11×17 · north = toward the shower

BATHROOM REMODEL

Simon's Bathroom

Layout, fixtures & finishes

Issued 2026-11-04

For coordination — not for construction


NOTES

Dimensions from the design model, built from the owner's SketchUp.
Verify all dimensions in field.
Do not scale drawings.
Heights are above finished floor.
Plan dims to finished wall faces.

FLOOR PLAN — DIMENSIONED


Room, fixture locations, clearances and rough-in centerlines

A-101

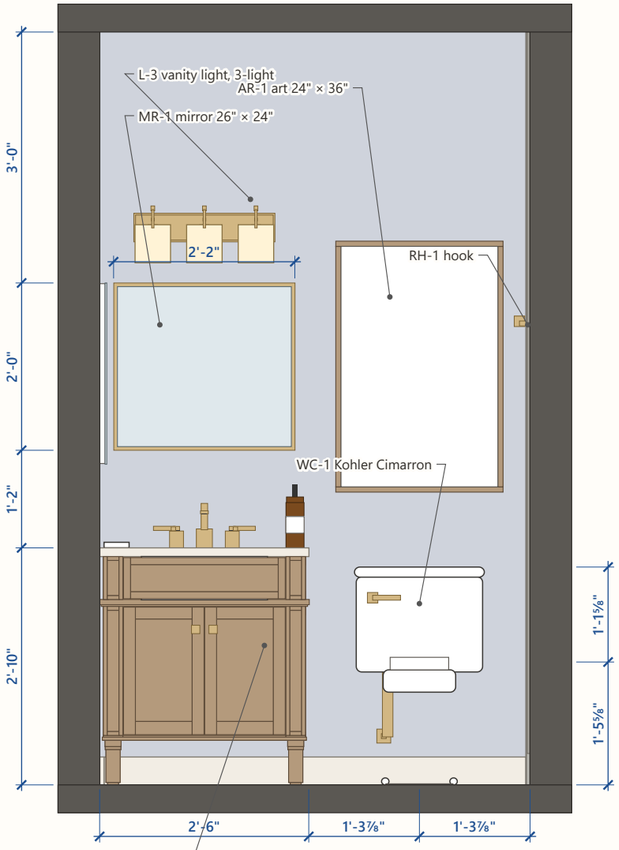

1 VANITY & TOILET WALL

1/2" = 1'-0" on 11×17 · looking west

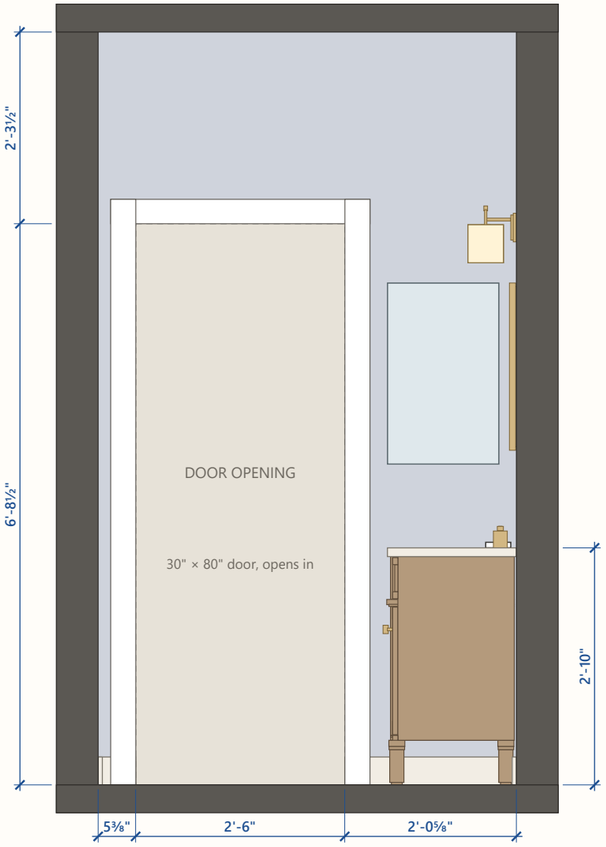

2 DOOR WALL

1/2" = 1'-0" on 11×17 · looking south

BATHROOM REMODEL

Simon's Bathroom

Layout, fixtures & finishes

Issued 2026-11-04

For coordination — not for construction


NOTES

Dimensions from the design model, built from the owner's SketchUp.
Verify all dimensions in field.
Do not scale drawings.
Heights are above finished floor.
Plan dims to finished wall faces.

INTERIOR ELEVATIONS


Vanity & toilet wall and door wall

A-201

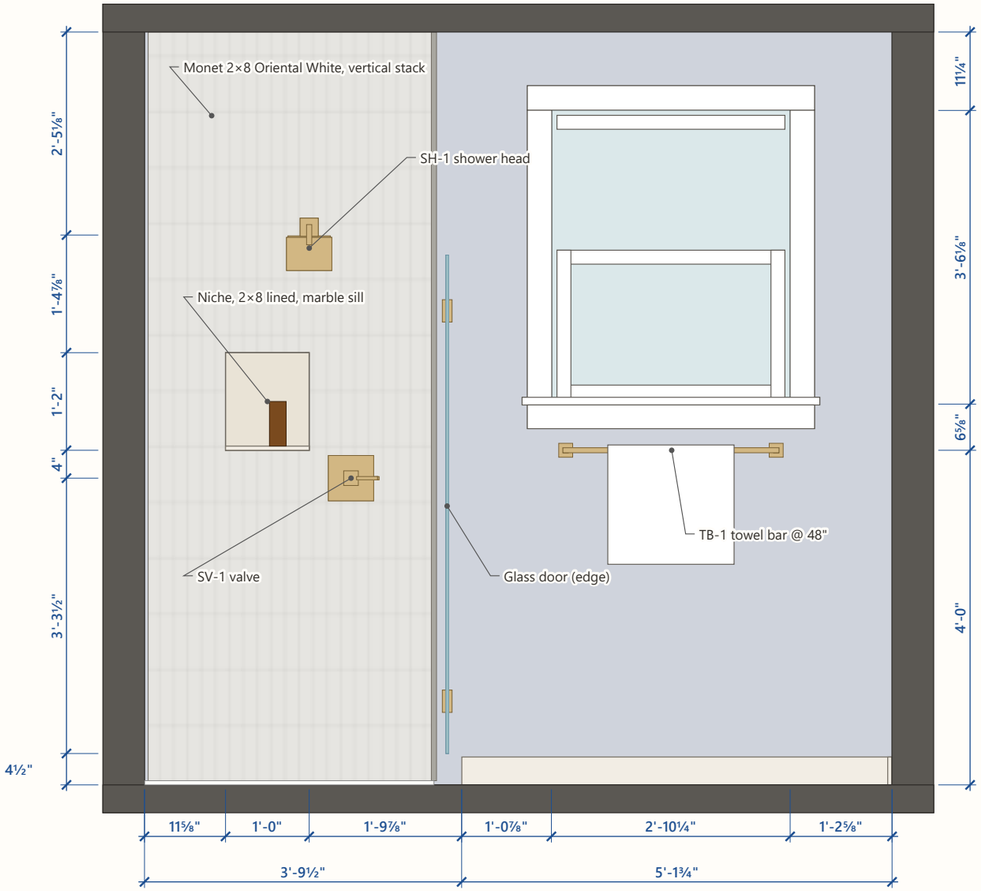

3 **WINDOW WALL**

1/2" = 1'-0" on 11×17 · looking east

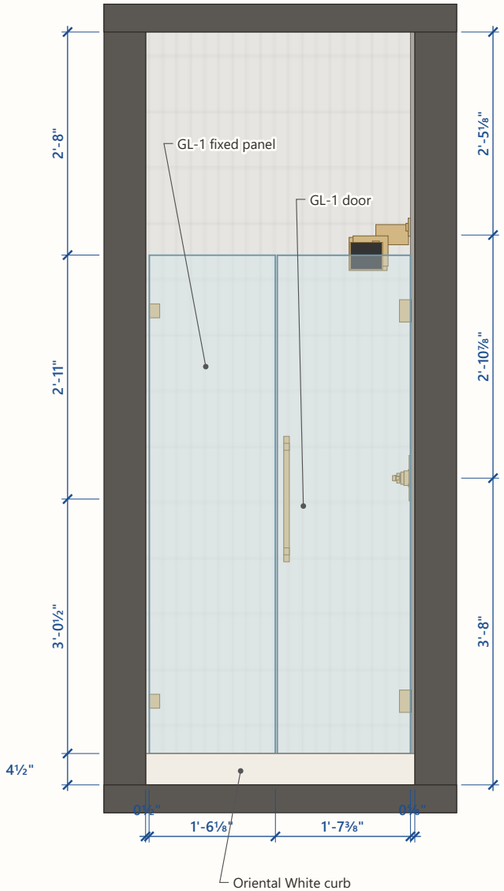

4 **SHOWER**

1/2" = 1'-0" on 11×17 · looking north, through the glass

BATHROOM REMODEL

Simon's Bathroom

Layout, fixtures & finishes

Issued 2026-11-04

For coordination — not for construction


NOTES

Dimensions from the design model, built from the owner's SketchUp.
Verify all dimensions in field.
Do not scale drawings.
Heights are above finished floor.
Plan dims to finished wall faces.

INTERIOR ELEVATIONS

Window wall (with shower side wall) and shower back wall

A-202

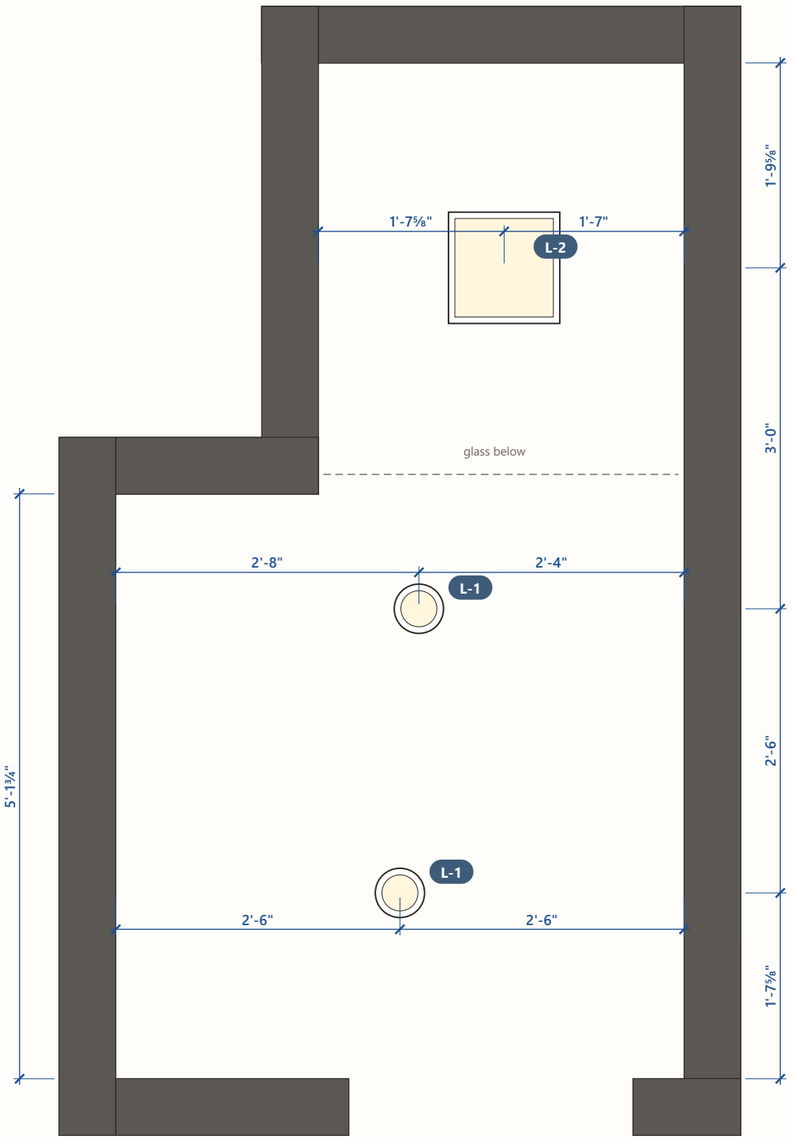

1 **REFLECTED CEILING PLAN**

3/4" = 1'-0" on 11×17 · ceiling 9'-0" AFF

LIGHTING SCHEDULE

L-1	× 2	4" recessed downlight, white trim, 2700–3000 K, dimmable
L-2	× 1	Shower fan/light: Delta Breez Integrity ITG100ELED, 100 CFM, 1.5 sone, dimmable edge-lit LED panel 1000 lm 3000 K; ~11¾" sq. grille, 4" duct (wet-location listed; confirm with spec sheet)
L-3	× 1	Vanity light over the mirror: Wildon Home 3-light (Wayfair W118271903, owner's photo), rectangular brass backplate with a chamfered face, three tapered pleated white shades on stems; Champagne Bronze-type finish; ~20¼" W plate (scaled from the photo -- confirm with the spec sheet); 3 × E26, 2700-3000 K dimmable; box centered on the mirror, plate 78" - 82" AFF, shade bottoms ~3" above the mirror
EF-1	× —	Exhaust fan: provided by L-2 in the shower; duct to exterior

NOTES

Switch at the door, latch side (window wall), 48" AFF: L-1/L-2 on a dimmer; L-3 sconce on its own dimmer; L-2 fan on a separate switch or timer.

L-2 over the shower must be listed for wet locations (shower use) and GFCI protected per code; confirm the joist bay and the 4" duct run to the exterior.

BATHROOM REMODEL

Simon's Bathroom

Layout, fixtures & finishes

Issued 2026-11-04

For coordination — not for construction

NOTES

Dimensions from the design model, built from the owner's SketchUp.
Verify all dimensions in field.
Do not scale drawings.
Heights are above finished floor.
Plan dims to finished wall faces.

REFLECTED CEILING & LIGHTING PLAN

Fixture locations from the design model

A-401

FIXTURES & EQUIPMENT

Tag	Item	Product	Size / finish / location
V-1	Vanity	30" traditional freestanding vanity, weathered brown ash, per owner's product photo (30" keeps the toilet clearance)	30" W × 18½" D × 34" H; Carrara marble top, undermount oval basin; recessed-panel corner pilasters, false drawer front, belt moulding, 2 shaker doors; turned tapered legs; Champagne Bronze round knobs (owner)
F-1	Lavatory faucet	Delta Saylor two-handle widespread 3536-CZMPU-DST, Champagne Bronze; 6⅜" high, 5.56" reach, lever handles	8" spread on the top's 3 holes; matching Champagne Bronze pop-up drain (included); 2½" min. to backsplash
WC-1	Toilet	Kohler Cimarron Comfort Height elongated, 2-piece	12" rough-in; 28-13/16" D, 18-5/8" W tank, 16½" rim, 31¼" H; left-hand lever
SV-1	Shower valve trim	Delta Saylor Monitor 14 Series T14235-CZ (single-function), 6½" round plate, lever handle, Champagne Bronze	On a MultiChoice R10000-UNBXHF rough valve (sold separately); valve center 44" AFF on the window-side wall
SH-1	Shower head	Delta Saylor 6½" 5-spray head on a 5½" arm with round flange (part of T14235-CZ), Champagne Bronze	Arm outlet 80" AFF above the valve line; no handshower
SD-1	Shower drain	4" square tile-in drain cover	Champagne Bronze; at shower center
GL-1	Shower glass	Frameless ⅜" clear (low-iron) fixed panel + hinged door with pull bar	Panel 1'-6⅛", door 1'-7⅛"; 5'-11½" tall on the curb; Champagne Bronze clamps & hinges
MC-1	Medicine cabinet	Frameless mirrored medicine cabinet, recessed (as existing, owner photo)	16" W × 26" H, ~1" proud of the wall; door wall between the vanity corner and the door casing, 46" – 72" AFF, top aligned with the MR-1 mirror (9' ceiling); provide blocking / check the stud bay
MR-1	Mirror	Wildon Home combo mirror (owner's photo): plain glass in a thin flat brass frame (⅝" face); no lighting	26" W × 24" H × ~1" D (the photo's proportions; 30" would run into MC-1 in the corner), centered over the vanity, 48" - 72" AFF, top in line with MC-1; hang on a French cleat or D-rings into blocking
TB-1	Towel bar	30" towel bar	Champagne Bronze; under the window at 48" AFF
RH-1	Robe hook	Single hook	Champagne Bronze; jog wall at 66" AFF
AR-1	Art	Owner's framed print (24" × 36"), thin natural-oak frame	Centered over the toilet, bottom 42" AFF (level with the mirror bottom)

FINISHES

Surface	Material	Where / notes
Floor	Surfaces Galore Bianco Dolomite basketweave w/ blue-gray dots, polished (SG514), 12" sheets, ⅜" thick	Main room and under the vanity; ~2" × 1.1" pieces, ⅜" dots on a 1.59" grid; 1/16" MEDIUM GRAY grout; grid centered on the room (equal cuts at the walls, door and curb)
Shower walls	Bedrosians Monet 2" × 8" honed marble, Oriental White (100001380)	All three shower walls, pan to ceiling, tiles upright in a vertical stack; no liner; Monet ½" × 12" Oriental White trim on exposed edges; niche lined to match; 1/16" white grout; seal the marble
Shower floor	Bedrosians Monet Honed Marble Mosaic 8, 1" penny round, Oriental White (100001428)	Shower floor, sloped to the drain; white grout; same stone as the walls; seal the marble
Shower curb	Oriental White marble slab, honed, one piece (to match the Monet Oriental White shower floor and walls)	4" × 4½" high, full width under the glass
Wall border	Monet 2" × 8" Oriental White, as the shower walls	Jog wall outside the shower (toilet side): 2" band (one full column) from the shower corner, floor to ceiling, vertical stack; ½" Monet trim on the outer edge
Niche sill	Oriental White marble, polished	Shower niche
Walls	Benjamin Moore Hale Navy HC-154 (LRV 8.4), matte (bath rated); trim stays white semi-gloss	All non-tiled walls
Ceiling	Bright flat white paint, bath rated (contrast with the navy walls)	9'-0" AFF
Baseboard	Honed Oriental White marble, 4" × ⅜" flat with eased top (to match the curb and shower)	All walls; stops at the shower border on the jog wall
Trim	Semi-gloss white; door & window casings	Match existing profiles
Hardware	Champagne Bronze throughout (owner), matching the Delta Saylor F-1 / SV-1 / SH-1	Vanity knobs; SD-1; TB-1, RH-1; L-3 light; MR-1 frame; glass hardware; toilet lever; door hardware

BATHROOM REMODEL

Simon's Bathroom

Layout, fixtures & finishes

Issued 2026-11-04

For coordination — not for construction

NOTES

Dimensions from the design model, built from the owner's SketchUp.
Verify all dimensions in field.
Do not scale drawings.
Heights are above finished floor.
Plan dims to finished wall faces.

FIXTURE & FINISH SCHEDULE

Products and finishes as designed — confirm availability and lead times

A-501