
Simon's Bathroom

Hall bath renovation · 5'-0" × 8'-11" with walk-in shower

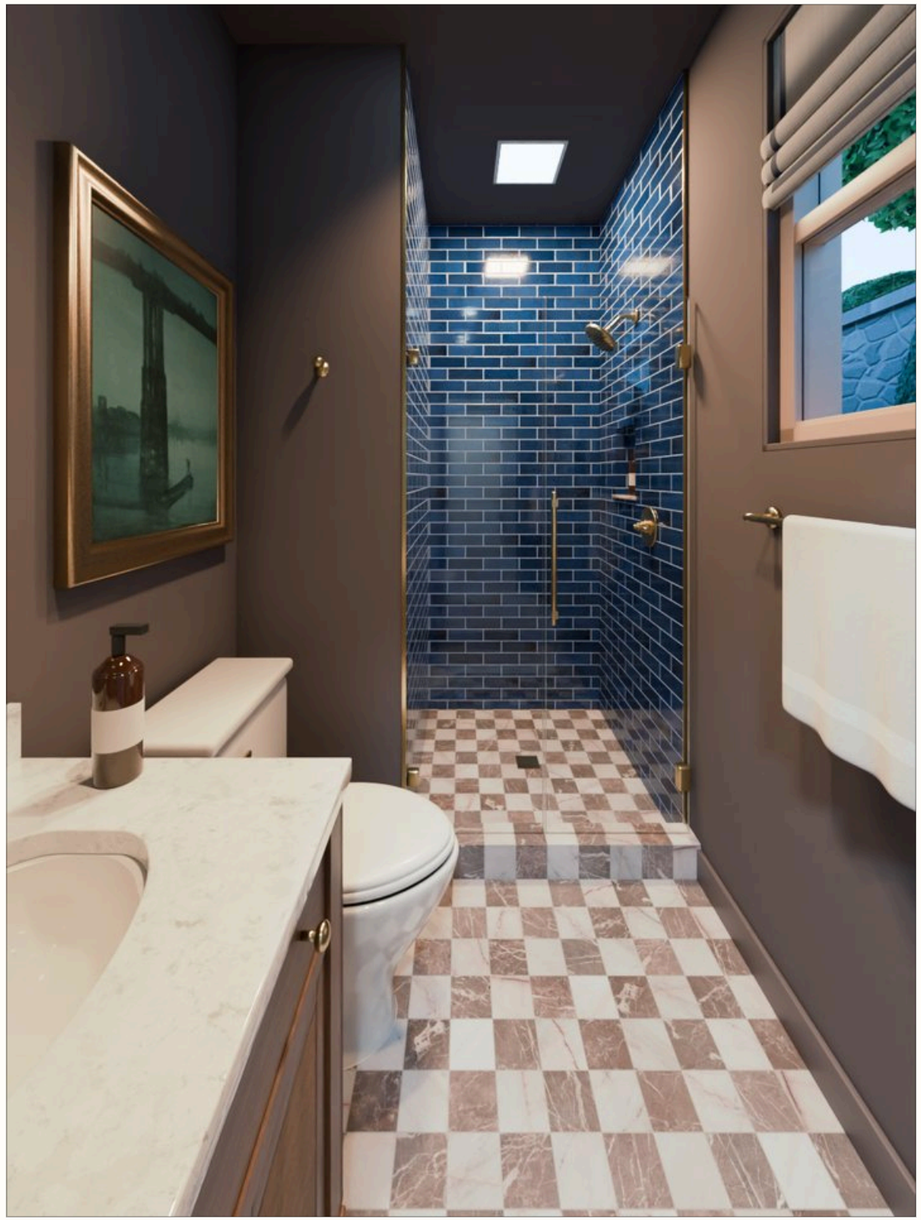

Design rendering from the doorway (Blender / Cycles). Finishes are representative.

DESIGN INTENT

Classic bath with a walnut vanity with woven-cane doors and Champagne Bronze knobs (Carrara marble top, undermount oval basin), a White #7 and Cafe Tenayo 4×4 tumbled marble checkerboard floor, carried over the curb and through the shower, the whole room colour-drenched in Farrow & Ball London Clay -- walls, ceiling, baseboards, door and window trim -- for a moody London-house feel, and a walk-in shower in cobalt-navy glossy 2½×8 handmade-look ceramic subway tile with white grout, floor to ceiling, behind clear frameless glass. Shower trim and vanity faucet Delta Saylor in Champagne Bronze; all other hardware Champagne Bronze to match.

GENERAL NOTES

1. Dimensions come from the design model (built from the owner's SketchUp file). Field-verify every dimension before ordering or cutting; the room has not been field-measured for this set.
2. Plan dimensions are to finished wall faces. Heights are above finished floor (AFF).
3. Fixture sizes are the specified products' published dimensions; confirm rough-ins against the manufacturer spec sheets on site.
4. Toilet: 12" rough-in, 15⅞" from the shower jog wall to centerline and 15" from the 30" vanity's side (the 15" code minimum, IRC P2705 / IPC 405.3.1) -- do not widen the vanity.
5. Shower: provide waterproof membrane on all wet walls and the pan, sloped to the drain. Niche is recessed into the window-side wall, lined in the blue subway tile with a veined marble shelf.
6. Shower tile set-out: 2½×8 subway, horizontal running bond with a half-tile stagger, 1/8" white joints, no liner. Start a full course on the curb line, centre the head joints on the back wall so the corner cuts match; cut row at the ceiling. Handmade-look tile: expect varied edges and glaze.
7. GFCI receptacle is required by code but not modeled — locate with the electrician. Exhaust: L-2 fan/light in the shower. MR-1 mirror has no power (no box needed).
8. Owner direction: no plant or vase on the vanity; vanity faucet Delta Saylor, Champagne Bronze.

SHEET INDEX

A-001	Cover, notes & index
A-101	Floor plan — dimensioned
A-201	Elevations — vanity / toilet wall & door wall
A-202	Elevations — window wall & shower
A-401	Reflected ceiling & lighting plan
A-501	Fixture & finish schedule

BATHROOM REMODEL

Simon's Bathroom

Layout, fixtures & finishes

Issued 2026-11-11

For coordination — not for construction


NOTES

Dimensions from the design model, built from the owner's SketchUp.
Verify all dimensions in field.
Do not scale drawings.
Heights are above finished floor.
Plan dims to finished wall faces.

COVER, NOTES & INDEX

Design intent, general notes and sheet index

A-001

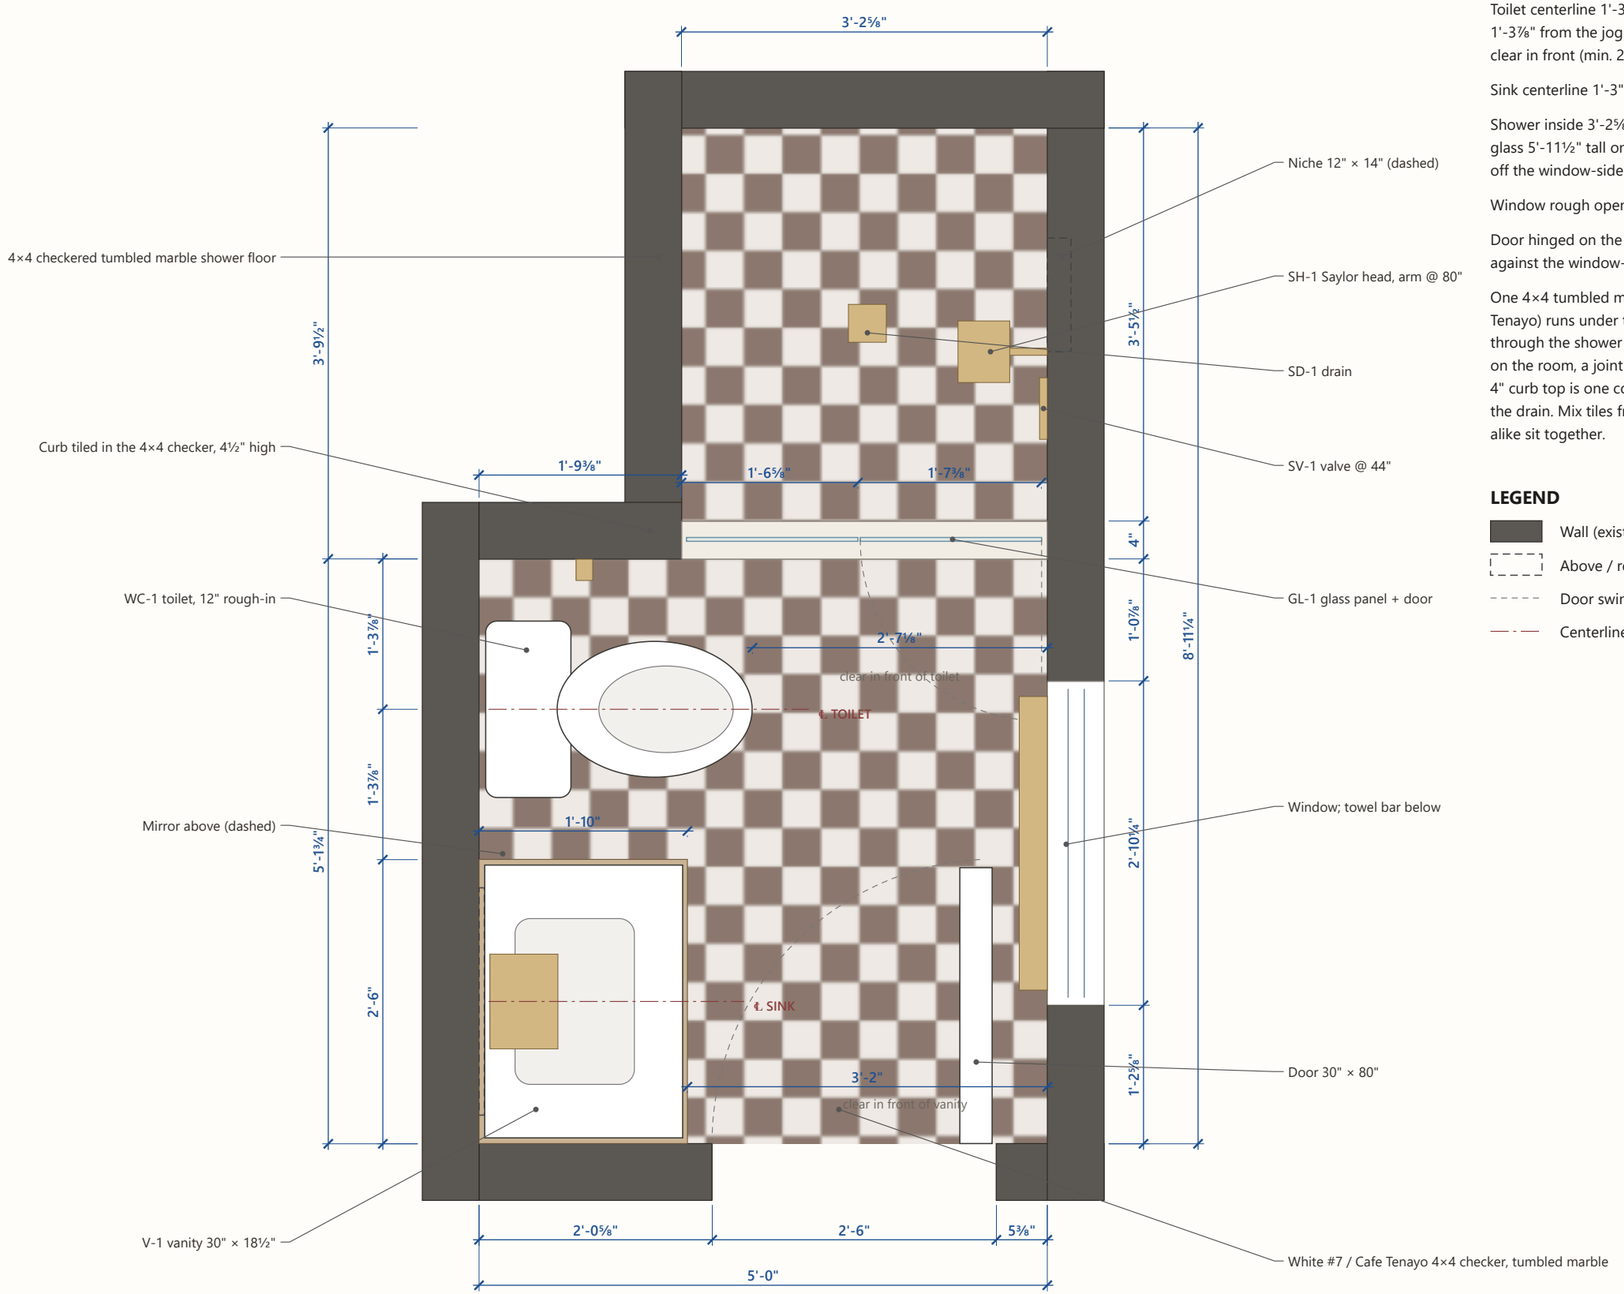

PLAN NOTES

Toilet centerline 1'-3⅜" from the vanity side and 1'-3⅜" from the jog wall (code min. 15"). 2'-7⅛" clear in front (min. 21").

Sink centerline 1'-3" from the door wall.

Shower inside 3'-2⅝" × 3'-5½" beyond a 4" curb; glass 5'-11½" tall on the curb, door 1'-7⅛" hinged off the window-side wall.

Window rough opening 2'-10¼" wide, sill 4'-6⅝" AFF.

Door hinged on the window side; it opens flat against the window-side wall.

One 4×4 tumbled marble checkerboard (White #7 / Cafe Tenayo) runs under the vanity, over the curb and through the shower on a single grid: a tile centred on the room, a joint on the curb's room edge so the 4" curb top is one course; shower floor sloped to the drain. Mix tiles from several boxes so no two alike sit together.

LEGEND

- Wall (existing / new, 6")
- Above / recessed (mirror, niche)
- Door swing
- Centerline

1 **FLOOR PLAN**

3/4" = 1'-0" on 11×17 · north = toward the shower

BATHROOM REMODEL

Simon's Bathroom

Layout, fixtures & finishes

Issued 2026-11-11

For coordination — not for construction


NOTES

Dimensions from the design model, built from the owner's SketchUp.
Verify all dimensions in field.
Do not scale drawings.
Heights are above finished floor.
Plan dims to finished wall faces.

FLOOR PLAN — DIMENSIONED


Room, fixture locations, clearances and rough-in centerlines

A-101

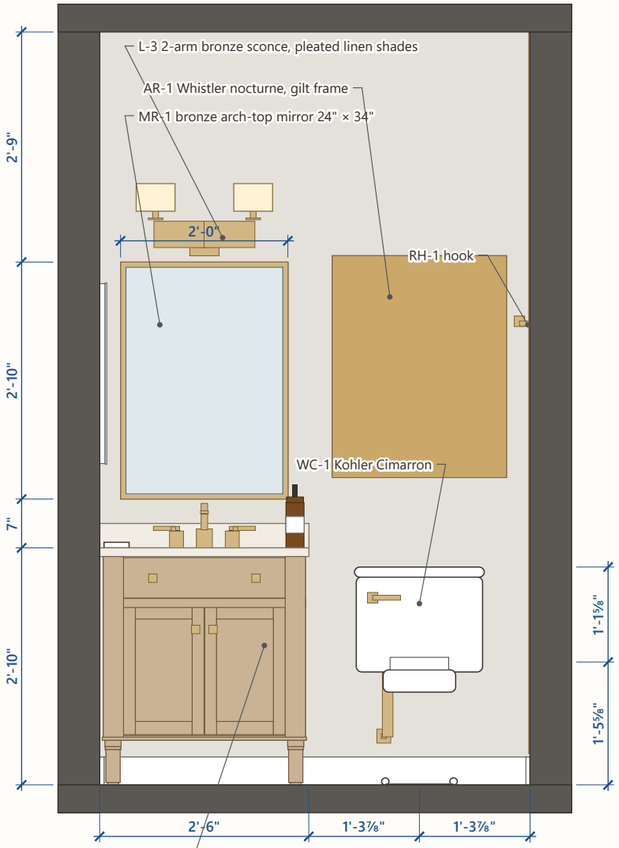

1 **VANITY & TOILET WALL**

1/2" = 1'-0" on 11×17 · looking west

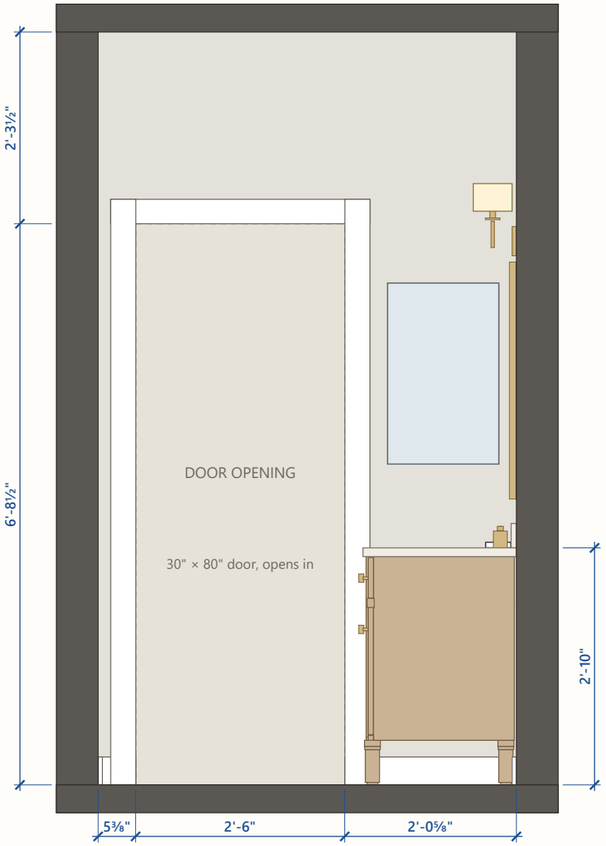

2 **DOOR WALL**

1/2" = 1'-0" on 11×17 · looking south

BATHROOM REMODEL

Simon's Bathroom

Layout, fixtures & finishes

Issued 2026-11-11

For coordination — not for construction


NOTES

Dimensions from the design model, built from the owner's SketchUp.
Verify all dimensions in field.
Do not scale drawings.
Heights are above finished floor.
Plan dims to finished wall faces.

INTERIOR ELEVATIONS


Vanity & toilet wall and door wall

A-201

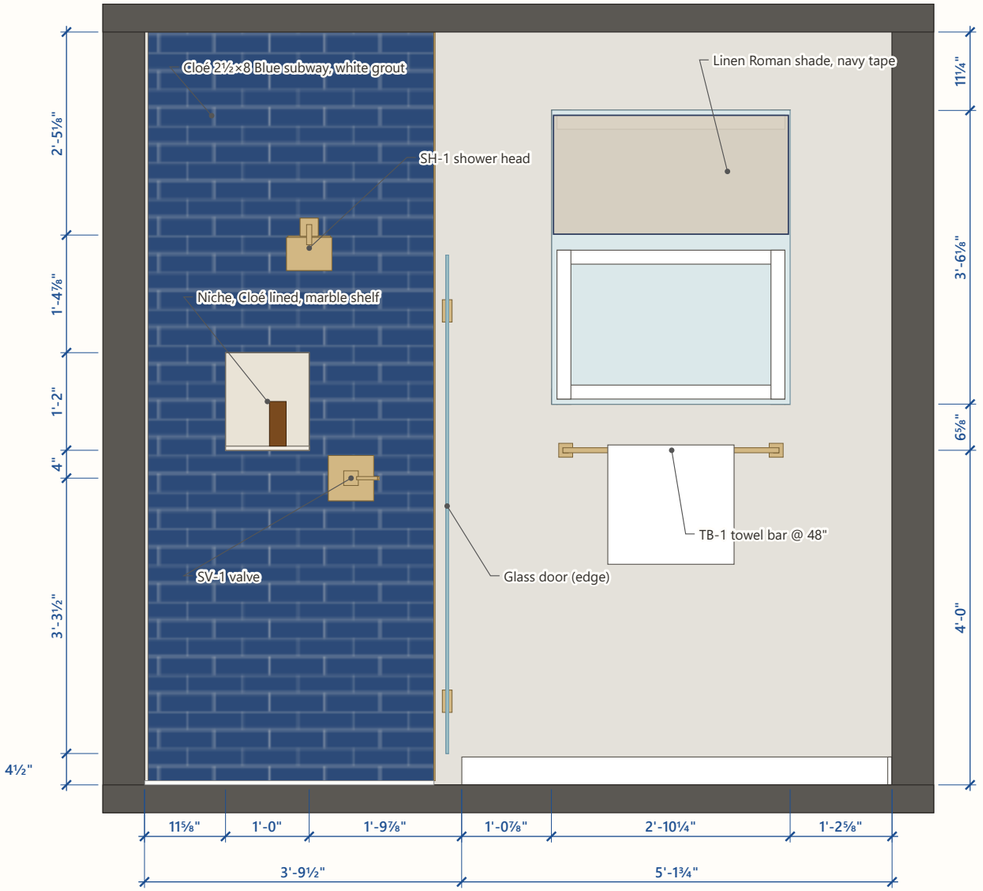

3 **WINDOW WALL**

1/2" = 1'-0" on 11×17 · looking east

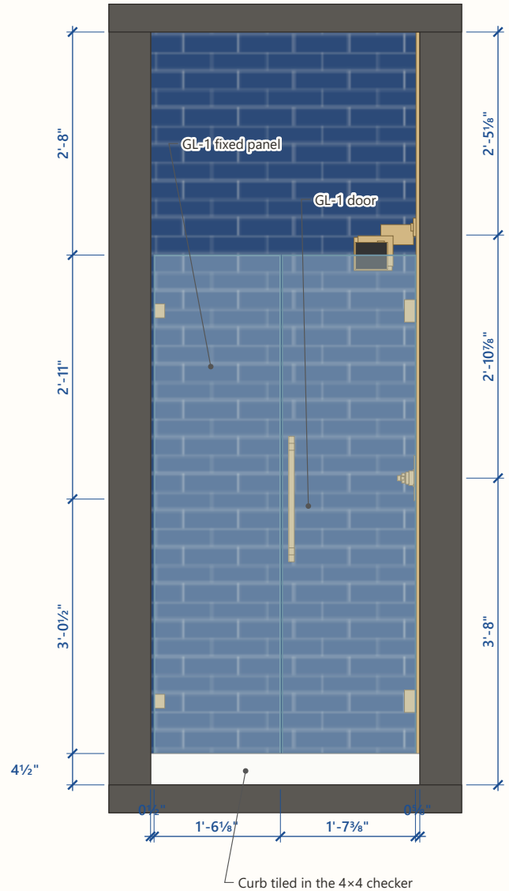

4 **SHOWER**

1/2" = 1'-0" on 11×17 · looking north, through the glass

BATHROOM REMODEL

Simon's Bathroom

Layout, fixtures & finishes

Issued 2026-11-11

For coordination — not for construction


NOTES

Dimensions from the design model, built from the owner's SketchUp.
Verify all dimensions in field.
Do not scale drawings.
Heights are above finished floor.
Plan dims to finished wall faces.

INTERIOR ELEVATIONS

Window wall (with shower side wall) and shower back wall

A-202

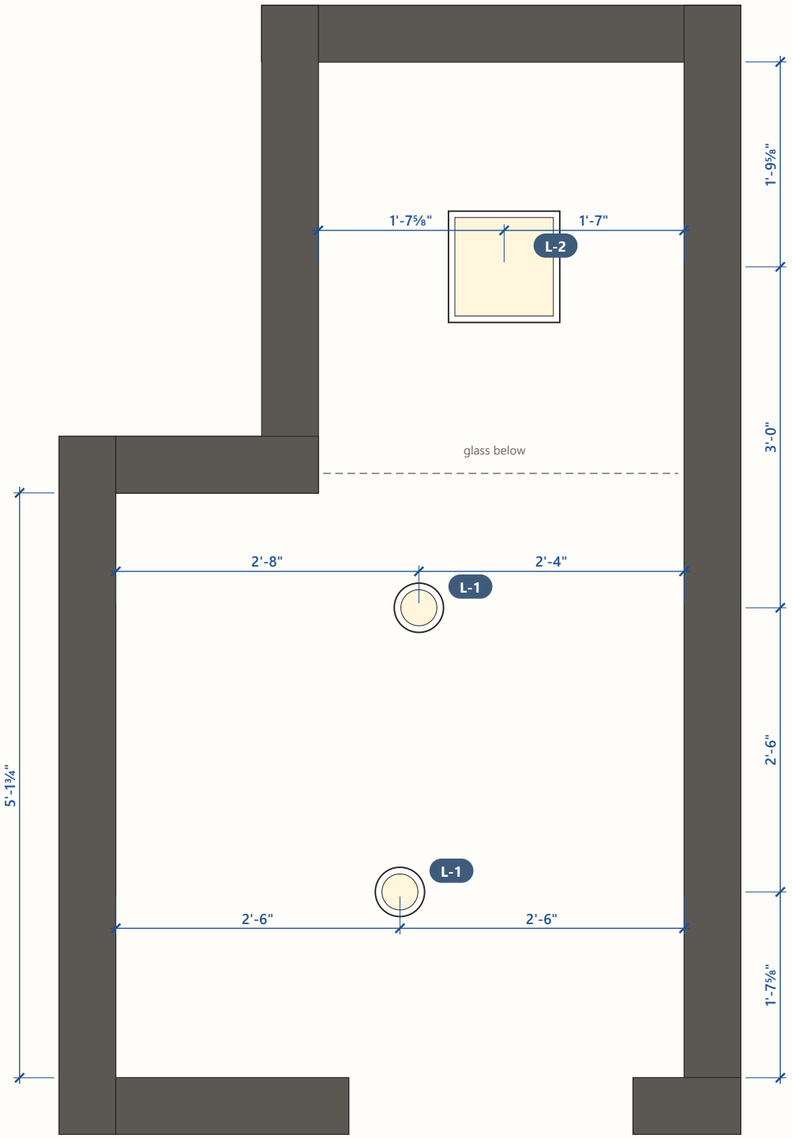

1 **REFLECTED CEILING PLAN**

3/4" = 1'-0" on 11×17 · ceiling 9'-0" AFF

LIGHTING SCHEDULE

L-1	× 2	4" recessed downlight, white trim, 2700–3000 K, dimmable
L-2	× 1	Shower fan/light: Delta Breez Integrity ITG100ELED, 100 CFM, 1.5 sone, dimmable edge-lit LED panel 1000 lm 3000 K; ~11¾" sq. grille, 4" duct (wet-location listed; confirm with spec sheet)
L-3	× 1	Vanity light over the mirror: traditional 2-arm wall sconce in Champagne Bronze -- round backplate, swan-neck arms, bobeches and candle sleeves, small pleated cream linen tapered shades (about 5" base), candle bulbs 2700 K; ~19" wide, centred over the mirror, backplate 78" AFF; owner to pick the exact fixture (damp-rated)
EF-1	× —	Exhaust fan: provided by L-2 in the shower; duct to exterior

NOTES

Switch at the door, latch side (window wall), 48" AFF: L-1/L-2 on a dimmer; L-3 sconce on its own dimmer; L-2 fan on a separate switch or timer.

L-2 over the shower must be listed for wet locations (shower use) and GFCI protected per code; confirm the joist bay and the 4" duct run to the exterior.

BATHROOM REMODEL

Simon's Bathroom

Layout, fixtures & finishes

Issued 2026-11-11

For coordination — not for construction

NOTES

Dimensions from the design model, built from the owner's SketchUp.
Verify all dimensions in field.
Do not scale drawings.
Heights are above finished floor.
Plan dims to finished wall faces.

REFLECTED CEILING & LIGHTING PLAN

Fixture locations from the design model

A-401

FIXTURES & EQUIPMENT

Tag	Item	Product	Size / finish / location
V-1	Vanity	Ari Bath Annie 30" style vanity in a WALNUT finish (owner, design81) -- Annie is listed in Weathered Fir: confirm a walnut finish, or use a walnut vanity of the same size and style (30" keeps the toilet clearance)	30" W × 22" D × 34½" H; solid wood, plain solid sides, slab tilt-out top drawer, 2 doors with woven-cane panels, tapered legs, warm mid-dark walnut, satin oiled finish; Italian Carrara marble top, pre-drilled 8" widespread; Champagne Bronze round knobs (replace the supplied black ones), 2 on the drawer + 2 on the doors; 3½" Carrara backsplash. 22" deep: check the walkway to the door
F-1	Lavatory faucet	Delta Saylor two-handle widespread 3536-CZMPU-DST, Champagne Bronze; 6⅜" high, 5.56" reach, lever handles	8" spread on the top's 3 holes; matching Champagne Bronze pop-up drain (included); 2½" min. to backsplash
WC-1	Toilet	Kohler Cimarron Comfort Height elongated, 2-piece	12" rough-in; 28-13/16" D, 18-5/8" W tank, 16½" rim, 31¼" H; left-hand lever
SV-1	Shower valve trim	Delta Saylor Monitor 14 Series T14235-CZ (single-function), 6½" round plate, lever handle, Champagne Bronze	On a MultiChoice R10000-UNBXHF rough valve (sold separately); valve center 44" AFF on the window-side wall
SH-1	Shower head	Delta Saylor 6½" 5-spray head on a 5½" arm with round flange (part of T14235-CZ), Champagne Bronze	Arm outlet 80" AFF above the valve line; no handshower
SD-1	Shower drain	4" square tile-in drain cover	Champagne Bronze; at shower center
GL-1	Shower glass	Frameless ⅜" clear (low-iron) fixed panel + hinged door with pull bar	Panel 1'-6⅛", door 1'-7⅛"; 5'-11½" tall on the curb; Champagne Bronze clamps & hinges
MC-1	Medicine cabinet	Frameless mirrored medicine cabinet, recessed (as existing, owner photo)	16" W × 26" H, ~1" proud of the wall; door wall between the vanity corner and the door casing, 46" – 72" AFF, top aligned with the MR-1 mirror (9' ceiling); provide blocking / check the stud bay
MR-1	Mirror	Arch-top (round-top) mirror in a slim Champagne Bronze metal frame, 3/4" face	24" W × 34" H; centred on the faucet, bottom 41" AFF, top 75" AFF; D-rings / French cleat on the stud wall
TB-1	Towel bar	30" towel bar	Champagne Bronze; under the window at 48" AFF
RH-1	Robe hook	Single hook	Champagne Bronze; jog wall at 66" AFF
AR-1	Art	James McNeill Whistler, Nocturne: Blue and Gold - Old Battersea Bridge (c. 1872-75, public domain) -- fine-art canvas print about 20" × 26-7/8", in a 2-1/2" antique gilt bead-and-cove frame (about 25" × 31-7/8" overall)	Centred over the toilet at 60" AFF; hang on two hooks so it stays level in the steam

FINISHES

Surface	Material	Where / notes
Floor	Castelli Marble White #7 & Cafe Tenayo 4" × 4" Checkered Tumbled Marble, 3/8" thick (sold as a checker mix; min. 30 sf, 10 sf increments, ships 3-4 weeks)	Main room and under the vanity, to the curb; checkerboard square to the room, tile centred on the room's centre line; 1/16" light warm gray sanded grout; natural stone: blend from several boxes, seal before and after grouting, pH-neutral cleaner
Shower walls	Bedrosians Cloé 2.5" × 8" Glossy Ceramic, Blue (DECCLOBLU28G; actual 2-1/2" × 7-13/16"), handmade-look wavy glaze, V4 shade variation	All three shower walls, pan to ceiling, subway: horizontal running bond, half-tile stagger; 1/8" white grout; no liner; niche lined to match; blend tiles from several boxes; exposed tile edges at both sides of the shower opening: 3/8" square metal edge profile (Schluter Quadec class) in a brushed brass / bronze finish to match the Champagne Bronze, floor to ceiling (no grey pencil liner)
Shower floor	Same Castelli White #7 & Cafe Tenayo 4" × 4" checkered tumbled marble	Shower floor, continuing the room's checker over the curb; sloped to the drain (4" tiles take the slope with a centre drain; a linear drain would let them lie flatter); tumbled surface grips well wet; seal as the floor
Shower curb	Tiled in the same 4" × 4" checkered tumbled marble	4" × 4½" high, full width under the glass; one course on top (the checker continues from the floor), face tiles match the colour of the top tile above; slope the top 1/4" toward the shower
Niche shelf	Grey-veined white marble (Arabescato / Calacatta Viola look, per the owner's inspiration photo), polished -- owner to pick the slab	Shower niche
Walls	Farrow & Ball London Clay No. 244, Modern Emulsion (matte, bath rated)	All non-tiled walls; colour drench -- ceiling and woodwork in the same colour
Ceiling	Farrow & Ball London Clay No. 244, flat / Modern Emulsion, bath rated	9'-0" AFF; same colour as the walls (colour drench); recessed-light trims stay white
Baseboard	Painted wood (MDF or poplar) baseboard, 4" with a simple eased / small-ogee top, Farrow & Ball London Clay No. 244 in Modern Eggshell to match the walls	All walls; on the jog wall it runs to the shower corner
Trim & door	Farrow & Ball London Clay No. 244, Modern Eggshell: door (both faces), door casing & jambs. Window: no trim -- drywall-wrapped opening (returns and sill) in the wall paint, rounded corner bead	Match existing profiles; the vinyl window sashes stay their existing sandy peach
Window shade	Tailored flat Roman shade, warm oatmeal linen (lined), navy grosgrain border tape 7/8" wide set 1-1/2" in from	Window over the towel bar, measure the opening inside the jambs (about 34-1/4" W

BATHROOM REMODEL

Simon's Bathroom

Layout, fixtures & finishes

Issued 2026-11-11

For coordination — not for construction

NOTES

Dimensions from the design model, built from the owner's SketchUp.
Verify all dimensions in field.
Do not scale drawings.
Heights are above finished floor.
Plan dims to finished wall faces.

FIXTURE & FINISH SCHEDULE

Products and finishes as designed — confirm availability and lead times

A-501