
Bathroom 2

Hall bath renovation · 5'-0" × 8'-11" with walk-in shower

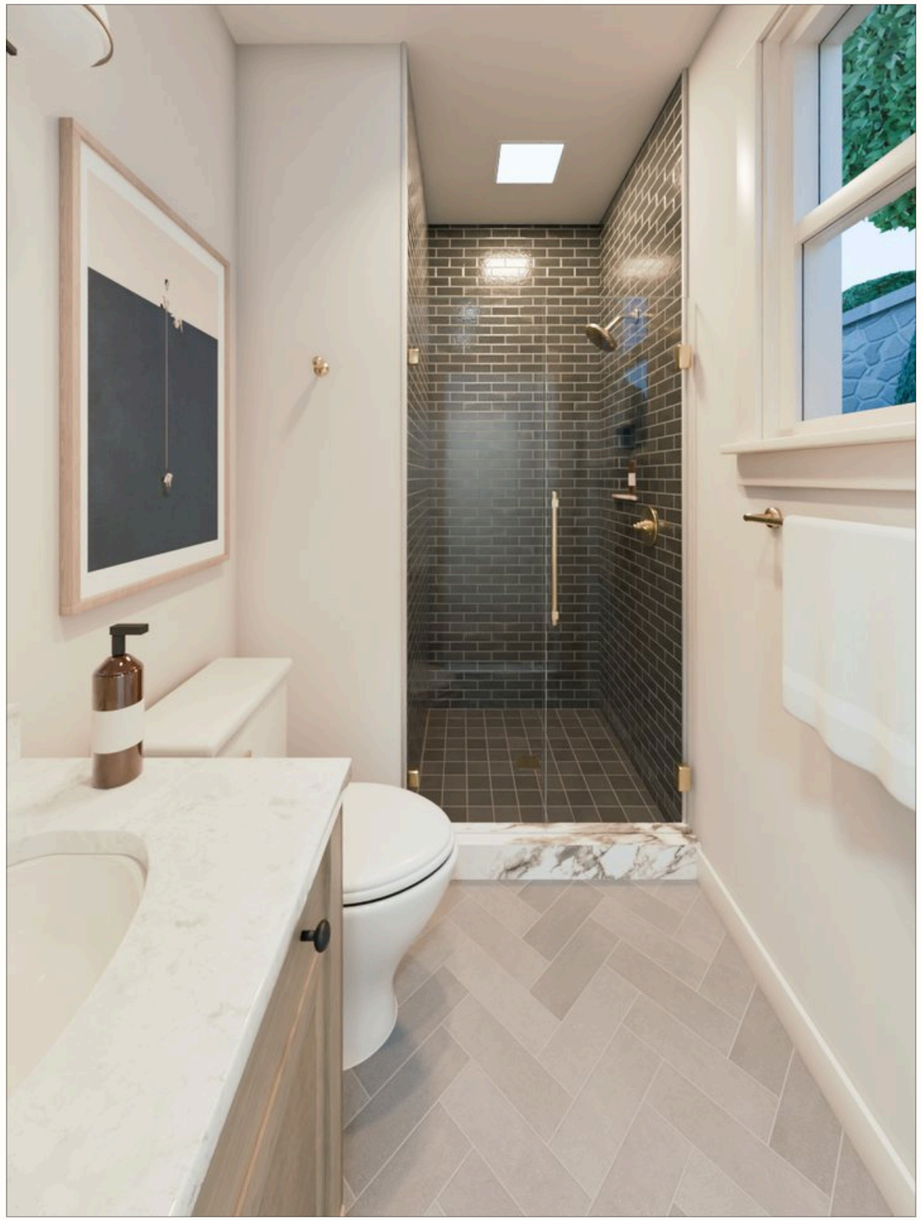

Design rendering from the doorway (Blender / Cycles). Finishes are representative.

DESIGN INTENT

Classic bath with a weathered-fir vanity with woven-cane doors (Carrara marble top, undermount oval basin), a light grey concrete-look 4×12 porcelain floor in a herringbone, Benjamin Moore Classic Gray walls, white painted baseboards, under a bright white ceiling, and a walk-in shower in charcoal glossy zellige 2×6 subway tile floor to ceiling, over a matte charcoal (Ebony) 4×4 shower floor, behind clear frameless glass. Shower trim and vanity faucet Delta Saylor in Champagne Bronze; all other hardware Champagne Bronze to match.

GENERAL NOTES

1. Dimensions come from the design model (built from the owner's SketchUp file). Field-verify every dimension before ordering or cutting; the room has not been field-measured for this set.
2. Plan dimensions are to finished wall faces. Heights are above finished floor (AFF).
3. Fixture sizes are the specified products' published dimensions; confirm rough-ins against the manufacturer spec sheets on site.
4. Toilet: 12" rough-in, 15⅞" from the shower jog wall to centerline and 15" from the 30" vanity's side (the 15" code minimum, IRC P2705 / IPC 405.3.1) -- do not widen the vanity.
5. Shower: provide waterproof membrane on all wet walls and the pan, sloped to the drain. Niche is recessed into the window-side wall, lined in the charcoal 2×6 with a veined marble shelf.
6. Shower tile set-out: 2×6 laid horizontally in a half-offset running bond (subway), no liner. Centre each wall so the end cuts match (no slivers under 2"); first joint on the pan, full 2" rows up, cut row at the ceiling. Handmade-look tile: expect varied edges and glaze.
7. GFCI receptacle is required by code but not modeled — locate with the electrician. Exhaust: L-2 fan/light in the shower. MR-1 mirror has no power (no box needed).
8. Owner direction: no plant or vase on the vanity; vanity faucet Delta Saylor, Champagne Bronze.

SHEET INDEX

A-001	Cover, notes & index
A-101	Floor plan — dimensioned
A-201	Elevations — vanity / toilet wall & door wall
A-202	Elevations — window wall & shower
A-401	Reflected ceiling & lighting plan
A-501	Fixture & finish schedule

BATHROOM REMODEL

Bathroom 2

Layout, fixtures & finishes

Issued 2026-11-08

For coordination — not for construction


NOTES

Dimensions from the design model, built from the owner's SketchUp.
Verify all dimensions in field.
Do not scale drawings.
Heights are above finished floor.
Plan dims to finished wall faces.

COVER, NOTES & INDEX

Design intent, general notes and sheet index

A-001

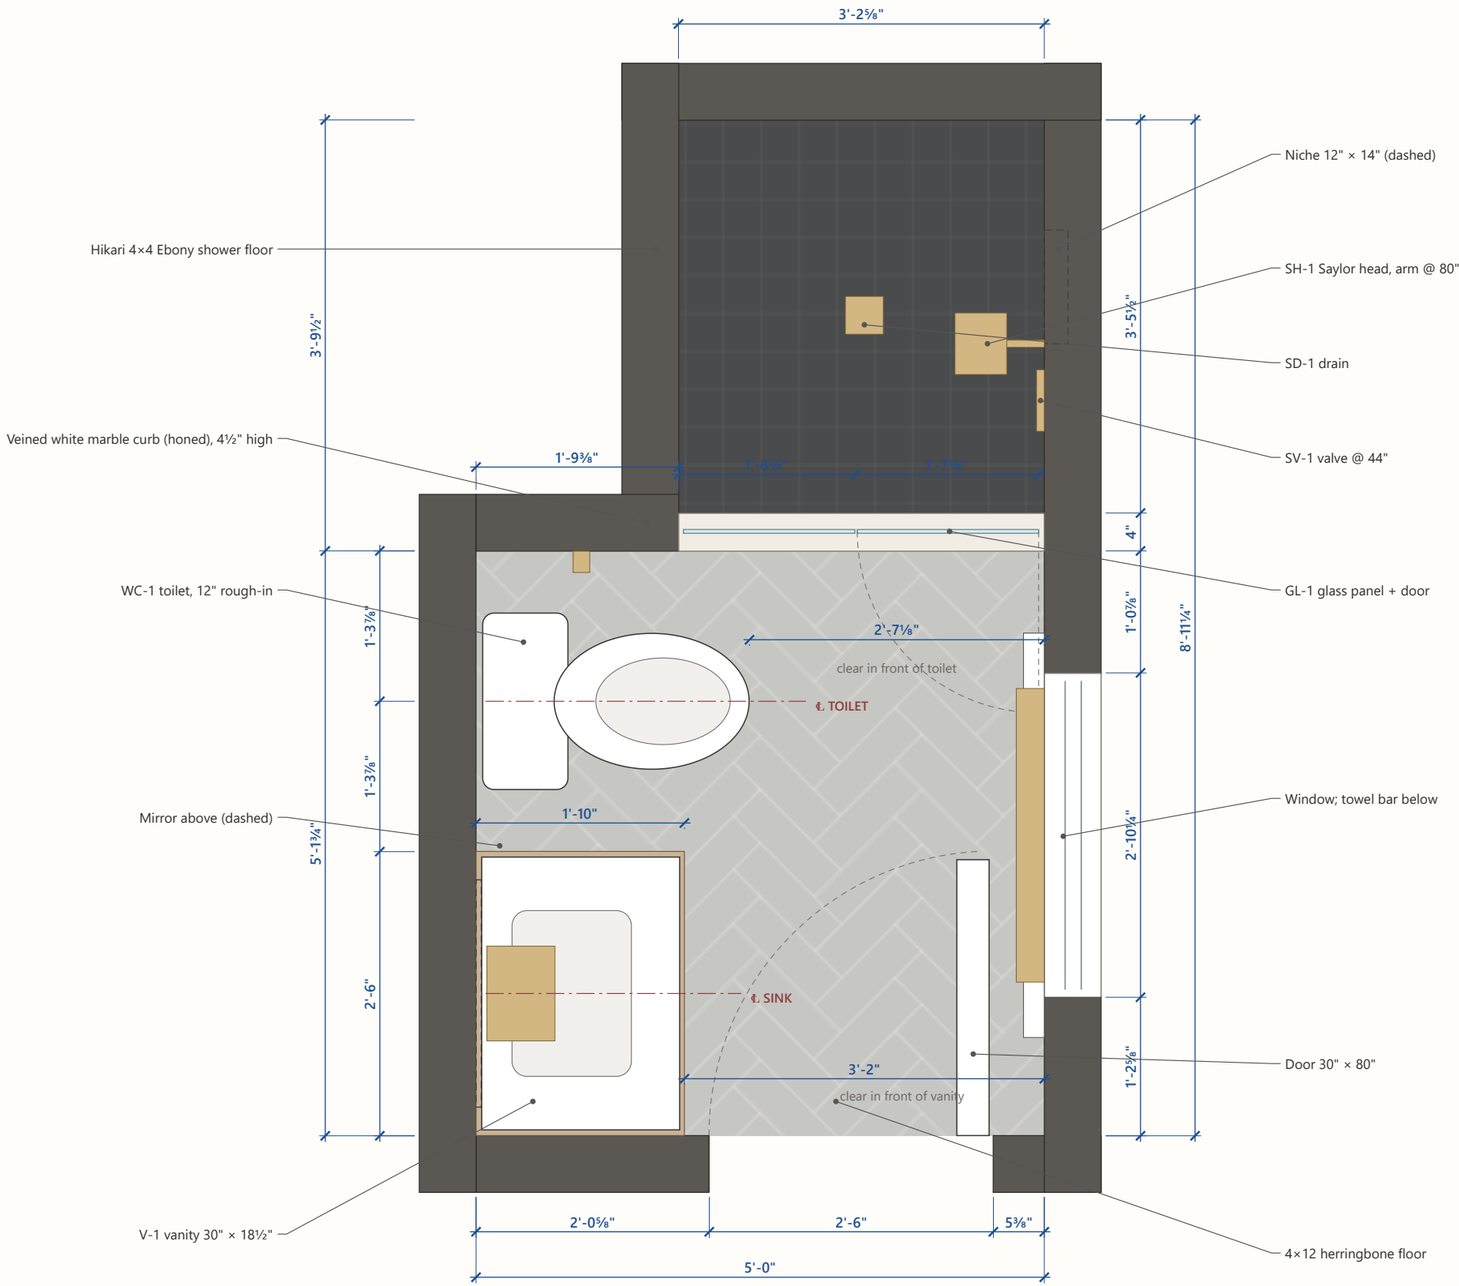

PLAN NOTES

Toilet centerline 1'-3⅞" from the vanity side and 1'-3⅞" from the jog wall (code min. 15"). 2'-7⅛" clear in front (min. 21").

Sink centerline 1'-3" from the door wall.

Shower inside 3'-2⅝" × 3'-5½" beyond a 4" curb; glass 5'-11½" tall on the curb, door 1'-7⅛" hinged off the window-side wall.

Window rough opening 2'-10¼" wide, sill 4'-6⅝" AFF.

Door hinged on the window side; it opens flat against the window-side wall.

Floor tile runs under the vanity and to the curb; the shower floor is the Hikari 4×4 Ebony, sloped to the drain.

LEGEND

- Wall (existing / new, 6")
- Above / recessed (mirror, niche)
- Door swing
- Centerline

1 **FLOOR PLAN**

3/4" = 1'-0" on 11×17 · north = toward the shower

BATHROOM REMODEL

Bathroom 2

Layout, fixtures & finishes

Issued 2026-11-08

For coordination — not for construction


NOTES

Dimensions from the design model, built from the owner's SketchUp.
Verify all dimensions in field.
Do not scale drawings.
Heights are above finished floor.
Plan dims to finished wall faces.

FLOOR PLAN — DIMENSIONED


Room, fixture locations, clearances and rough-in centerlines

A-101

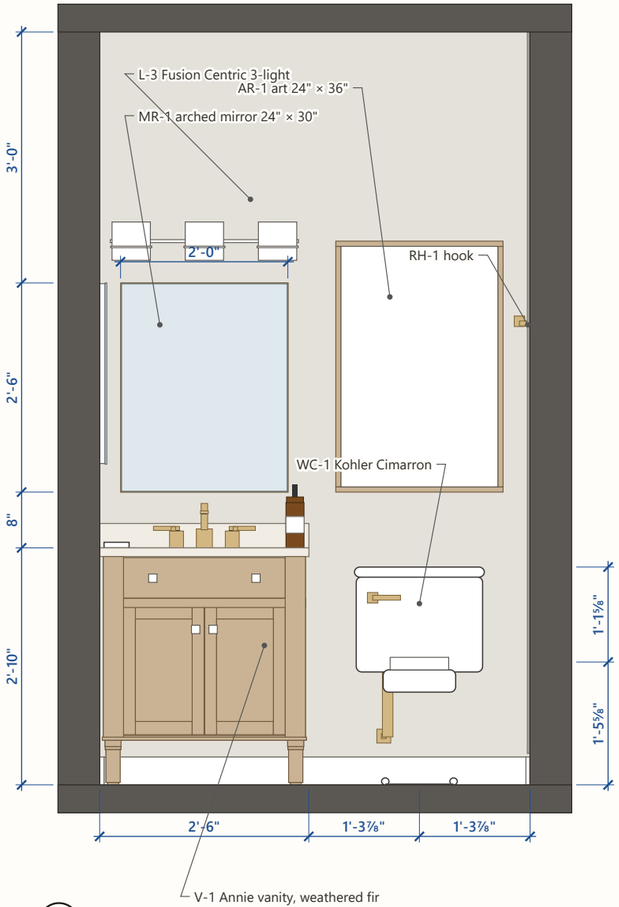

1 **VANITY & TOILET WALL**

1/2" = 1'-0" on 11×17 · looking west

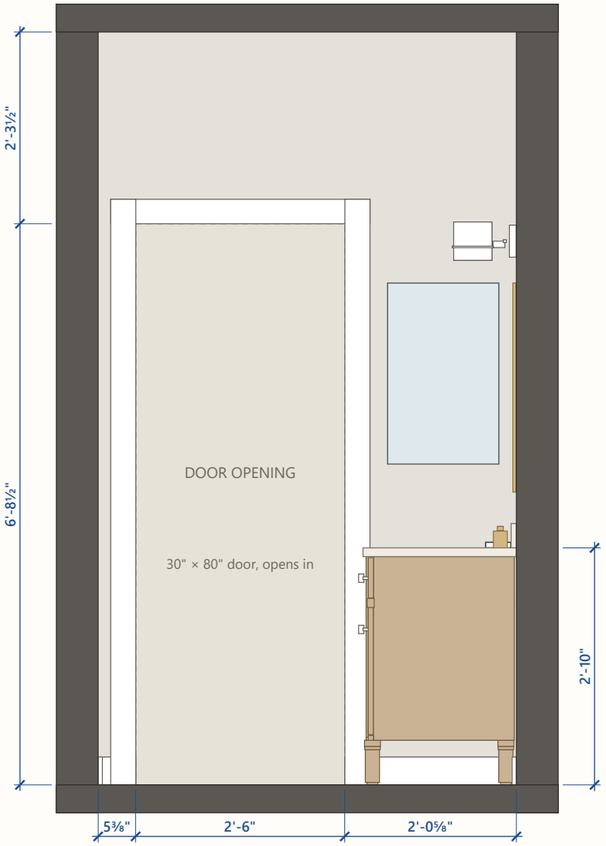

2 **DOOR WALL**

1/2" = 1'-0" on 11×17 · looking south

BATHROOM REMODEL

Bathroom 2

Layout, fixtures & finishes

Issued 2026-11-08

For coordination — not for construction


NOTES

Dimensions from the design model, built from the owner's SketchUp.
Verify all dimensions in field.
Do not scale drawings.
Heights are above finished floor.
Plan dims to finished wall faces.

INTERIOR ELEVATIONS


Vanity & toilet wall and door wall

A-201

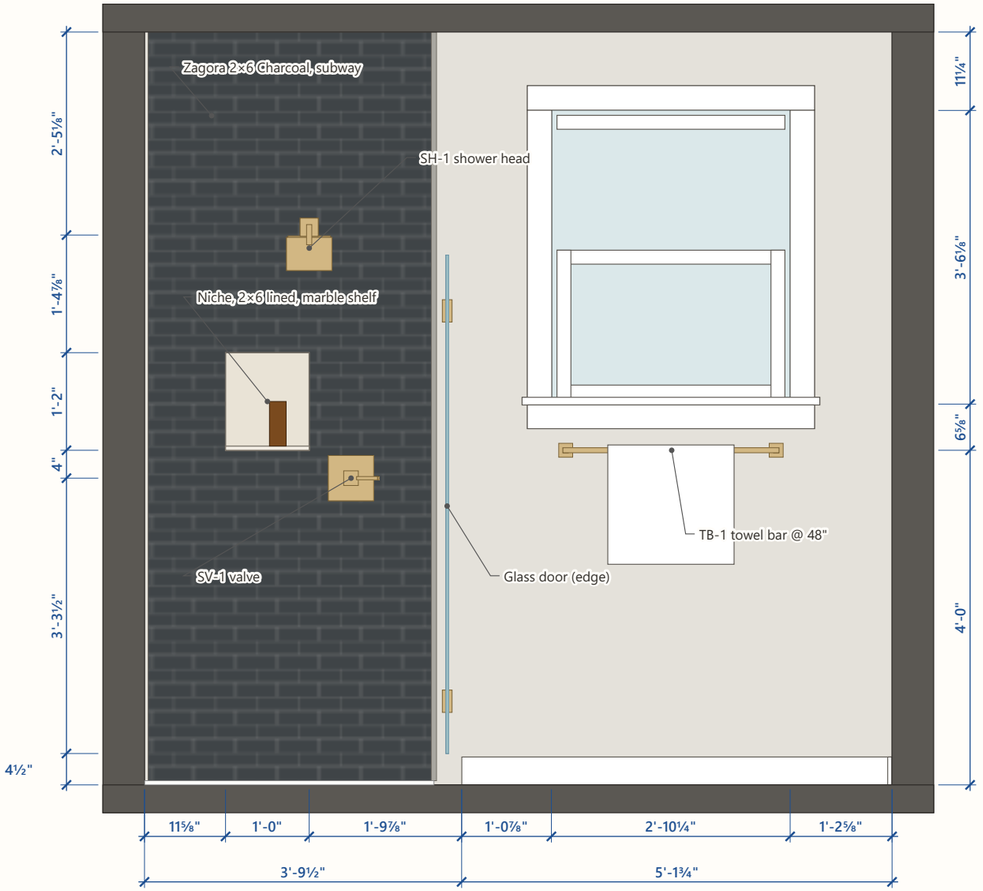

3 **WINDOW WALL**

1/2" = 1'-0" on 11×17 · looking east

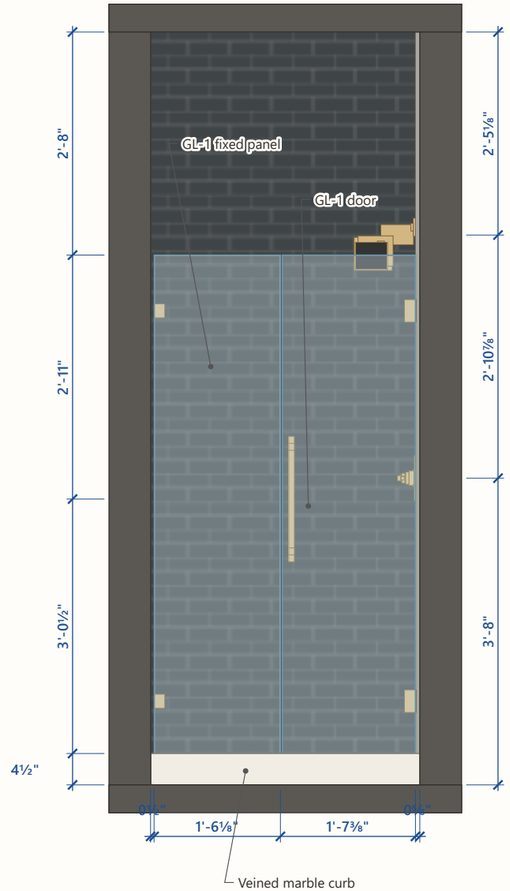

4 **SHOWER**

1/2" = 1'-0" on 11×17 · looking north, through the glass

BATHROOM REMODEL

Bathroom 2

Layout, fixtures & finishes

Issued 2026-11-08

For coordination — not for construction


NOTES

Dimensions from the design model, built from the owner's SketchUp.
Verify all dimensions in field.
Do not scale drawings.
Heights are above finished floor.
Plan dims to finished wall faces.

INTERIOR ELEVATIONS

Window wall (with shower side wall) and shower back wall

A-202

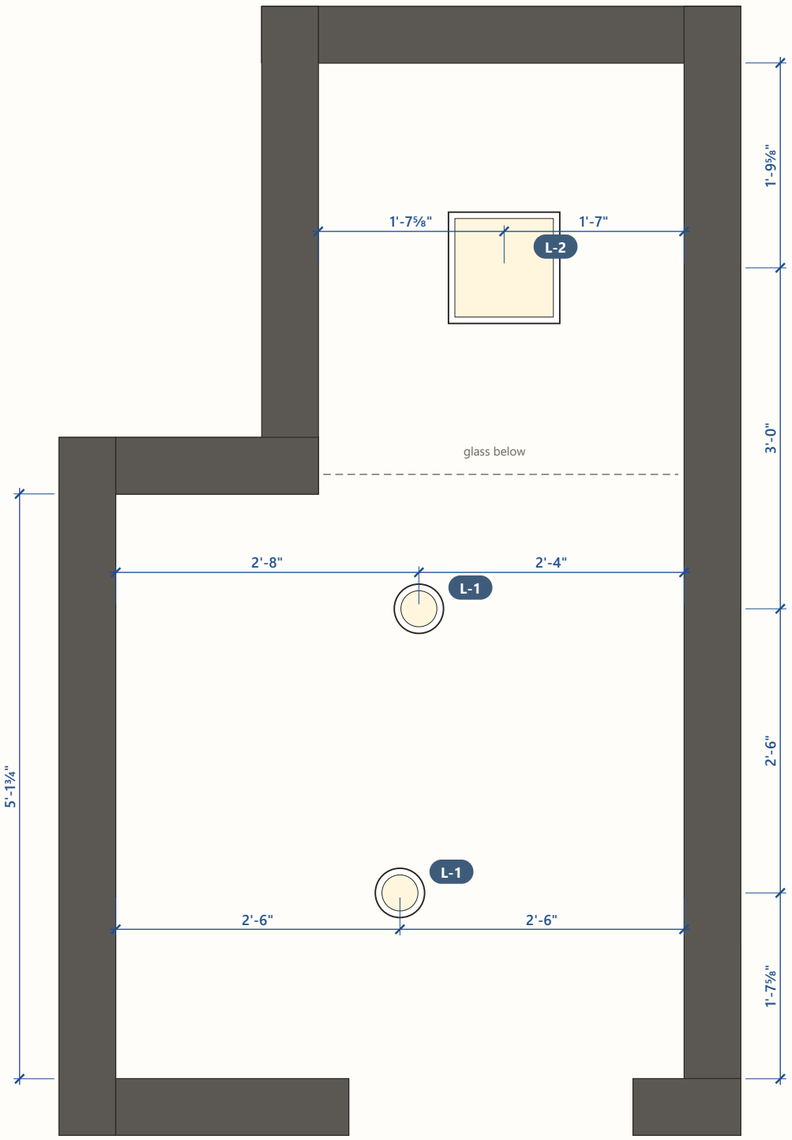

1 **REFLECTED CEILING PLAN**

3/4" = 1'-0" on 11×17 · ceiling 9'-0" AFF

LIGHTING SCHEDULE

L-1	× 2	4" recessed downlight, white trim, 2700–3000 K, dimmable
L-2	× 1	Shower fan/light: Delta Breez Integrity ITG100ELED, 100 CFM, 1.5 sone, dimmable edge-lit LED panel 1000 lm 3000 K; ~11¾" sq. grille, 4" duct (wet-location listed; confirm with spec sheet)
L-3	× 1	Vanity light over the mirror: Justice Design Group Fusion Centric 3-light (FSN-4163-OPAL-MBBR, Lumens JDG2633577), Matte Black with Brass, three cream opal globes set forward of a flat matte-black bar, each in a thin brass ring, round satin-brass backplate; centred over the mirror, ~78" AFF to centre (confirm size on the spec sheet: modelled ~27" W bar, 5½" globes)
EF-1	× —	Exhaust fan: provided by L-2 in the shower; duct to exterior

NOTES

Switch at the door, latch side (window wall), 48" AFF: L-1/L-2 on a dimmer; L-3 sconce on its own dimmer; L-2 fan on a separate switch or timer.

L-2 over the shower must be listed for wet locations (shower use) and GFCI protected per code; confirm the joist bay and the 4" duct run to the exterior.

BATHROOM REMODEL

Bathroom 2

Layout, fixtures & finishes

Issued 2026-11-08

For coordination — not for construction

NOTES

Dimensions from the design model, built from the owner's SketchUp.
Verify all dimensions in field.
Do not scale drawings.
Heights are above finished floor.
Plan dims to finished wall faces.

REFLECTED CEILING & LIGHTING PLAN

Fixture locations from the design model

A-401

FIXTURES & EQUIPMENT

Tag	Item	Product	Size / finish / location
V-1	Vanity	Ari Bath Annie 30" Bathroom Vanity, Weathered Fir (owner; 30" keeps the toilet clearance)	30" W × 22" D × 34½" H; solid wood, plain solid sides, slab tilt-out top drawer, 2 doors with woven-cane panels, tapered legs, ashy weathered-fir finish; Italian Carrara marble top, pre-drilled 8" widespread; matte black round knobs as supplied, 2 on the drawer + 2 on the doors; 3½" Carrara backsplash. 22" deep: check the walkway to the door
F-1	Lavatory faucet	Delta Saylor two-handle widespread 3536-CZMPU-DST, Champagne Bronze; 6⅜" high, 5.56" reach, lever handles	8" spread on the top's 3 holes; matching Champagne Bronze pop-up drain (included); 2½" min. to backsplash
WC-1	Toilet	Kohler Cimarron Comfort Height elongated, 2-piece	12" rough-in; 28-13/16" D, 18-5/8" W tank, 16½" rim, 31¼" H; left-hand lever
SV-1	Shower valve trim	Delta Saylor Monitor 14 Series T14235-CZ (single-function), 6½" round plate, lever handle, Champagne Bronze	On a MultiChoice R10000-UNBXHF rough valve (sold separately); valve center 44" AFF on the window-side wall
SH-1	Shower head	Delta Saylor 6½" 5-spray head on a 5½" arm with round flange (part of T14235-CZ), Champagne Bronze	Arm outlet 80" AFF above the valve line; no handshower
SD-1	Shower drain	4" square tile-in drain cover	Champagne Bronze; at shower center
GL-1	Shower glass	Frameless ⅜" clear (low-iron) fixed panel + hinged door with pull bar	Panel 1'-6⅛", door 1'-7⅛"; 5'-11½" tall on the curb; Champagne Bronze clamps & hinges
MC-1	Medicine cabinet	Frameless mirrored medicine cabinet, recessed (as existing, owner photo)	16" W × 26" H, ~1" proud of the wall; door wall between the vanity corner and the door casing, 46" – 72" AFF, top aligned with the MR-1 mirror (9' ceiling); provide blocking / check the stud bay
MR-1	Mirror	Moon Mirror Andy Star arched bathroom mirror, stainless steel frame in Champagne Bronze (thin frame, glass floating 1/12" inside)	24" W × 30" H; centred on the faucet, bottom 42" AFF (clears the spout), top 72" AFF; D-rings on the stud wall
TB-1	Towel bar	30" towel bar	Champagne Bronze; under the window at 48" AFF
RH-1	Robe hook	Single hook	Champagne Bronze; jog wall at 66" AFF
AR-1	Art	Owner's framed print (24" × 36"), thin natural-oak frame	Centered over the toilet, bottom 42" AFF (level with the mirror bottom)

FINISHES

Surface	Material	Where / notes
Floor	Grey concrete-look 4" × 12" matte porcelain (owner's selection; confirm make and item no.), laid in a 45° herringbone	Main room and under the vanity; 1/8" light grey grout as the owner's photo (owner to confirm colour); herringbone centred on the room so the cuts at the walls, door and curb match; follow the maker's grout-joint requirement
Shower walls	Bedrosians Zagora 2" × 6" Glossy Zellige Field Tile, Charcoal (100003212), ceramic	All three shower walls, pan to ceiling, laid horizontally in a half-offset running bond (subway); no liner; Zagora has no bullnose / trim pieces (Bedrosians line = 2x6 & 4x4 field, 2x2 and triangle mosaics), so finish exposed edges with a metal edge profile in a brushed brass / bronze finish to match the Champagne Bronze; niche lined to match; 1/8" light gray grout (as Bedrosians' photo); handmade-look: expect varied edges and glaze
Shower floor	Bedrosians Hikari 4" × 4" Matte Porcelain Field Tile, Ebony (100011402)	Shower floor, sloped to the drain; 1/8" medium gray grout; stack bond; confirm with Bedrosians that it is rated for wet floors (DCOF) -- a mosaic-mounted version grips better on the slope
Shower curb	Grey-veined white marble slab (as the baseboards and niche shelf), honed, one piece	4" × 4½" high, full width under the glass
Niche shelf	Grey-veined white marble (Arabescato / Calacatta Viola look, per the owner's inspiration photo), polished -- owner to pick the slab	Shower niche
Walls	Benjamin Moore Classic Gray OC-23, matte (bath rated); trim stays white semi-gloss	All non-tiled walls
Ceiling	Bright flat white paint, bath rated (a shade whiter than the Classic Gray walls)	9'-0" AFF
Baseboard	Painted wood (MDF or poplar) baseboard, 4" with a simple eased / small-ogee top, white semi-gloss to match the trim	All walls; on the jog wall it runs to the shower corner
Trim	Semi-gloss white; door & window casings	Match existing profiles
Hardware	Champagne Bronze (owner), matching the Delta Saylor F-1 / SV-1 / SH-1; vanity knobs matte black (as the Annie ships) to go with the black-and-brass L-3	SD-1; TB-1, RH-1; MR-1 frame; glass hardware; toilet lever; door hardware. Vanity knobs: matte black

BATHROOM REMODEL

Bathroom 2

Layout, fixtures & finishes

Issued 2026-11-08

For coordination — not for construction

NOTES

Dimensions from the design model, built from the owner's SketchUp.
Verify all dimensions in field.
Do not scale drawings.
Heights are above finished floor.
Plan dims to finished wall faces.

FIXTURE & FINISH SCHEDULE

Products and finishes as designed — confirm availability and lead times

A-501