Simon's Bathroom

Hall bath renovation · 5'-0" × 8'-11" with walk-in shower



Design rendering from the doorway (Blender / Cycles). Finishes are representative.

DESIGN INTENT

Classic bath with a traditional brown-ash vanity (Carrara marble top, undermount oval basin), marble white octagon-and-dot mosaic floor, Hale Navy walls under a bright white ceiling, and a walk-in shower in honed Carrara marble 2×8, vertical stack floor to ceiling, over a matching Carrara 1" penny round shower floor, behind clear frameless glass. Shower system champagne bronze (Delta); vanity hardware and faucet satin / brushed nickel.

GENERAL NOTES

1. Dimensions come from the design model (built from the owner's SketchUp file). Field-verify every dimension before ordering or cutting; the room has not been field-measured for this set.
2. Plan dimensions are to finished wall faces. Heights are above finished floor (AFF).
3. Fixture sizes are the specified products' published dimensions; confirm rough-ins against the manufacturer spec sheets on site.
4. Toilet: 12" rough-in, centered 15⅞" from the vanity and from the shower jog wall (code min. 15" to centerline, 21" clear in front).
5. Shower: provide waterproof membrane on all wet walls and the pan, sloped to the drain. Niche is recessed into the window-side wall, lined in the Monet 2×8 with a marble sill.
6. Shower tile set-out: 2×8 marble upright in a vertical stack (joints aligned both ways), no liner. Back wall centred with equal 1¾" end cuts; side walls centred with equal 1½" cuts; first joint on the pan, full 8" rows up, cut row at the ceiling.
7. Exhaust fan and GFCI receptacle are required by code but not modeled — locate with the electrician. MR-1 LED mirror: hardwire to a box behind the mirror (or plug-in), on the vanity circuit.
8. Owner direction: no plant or vase on the vanity; vanity hardware and faucet satin nickel.

SHEET INDEX

A-001	Cover, notes & index
A-101	Floor plan — dimensioned
A-201	Elevations — vanity / toilet wall & door wall
A-202	Elevations — window wall & shower
A-401	Reflected ceiling & lighting plan
A-501	Fixture & finish schedule

BATHROOM REMODEL

Simon's Bathroom

Layout, fixtures & finishes

Issued 2026-11-04

For coordination — not for construction


NOTES

Dimensions from the design model, built from the owner's SketchUp.
Verify all dimensions in field.
Do not scale drawings.
Heights are above finished floor.
Plan dims to finished wall faces.

COVER, NOTES & INDEX

Design intent, general notes and sheet index

A-001

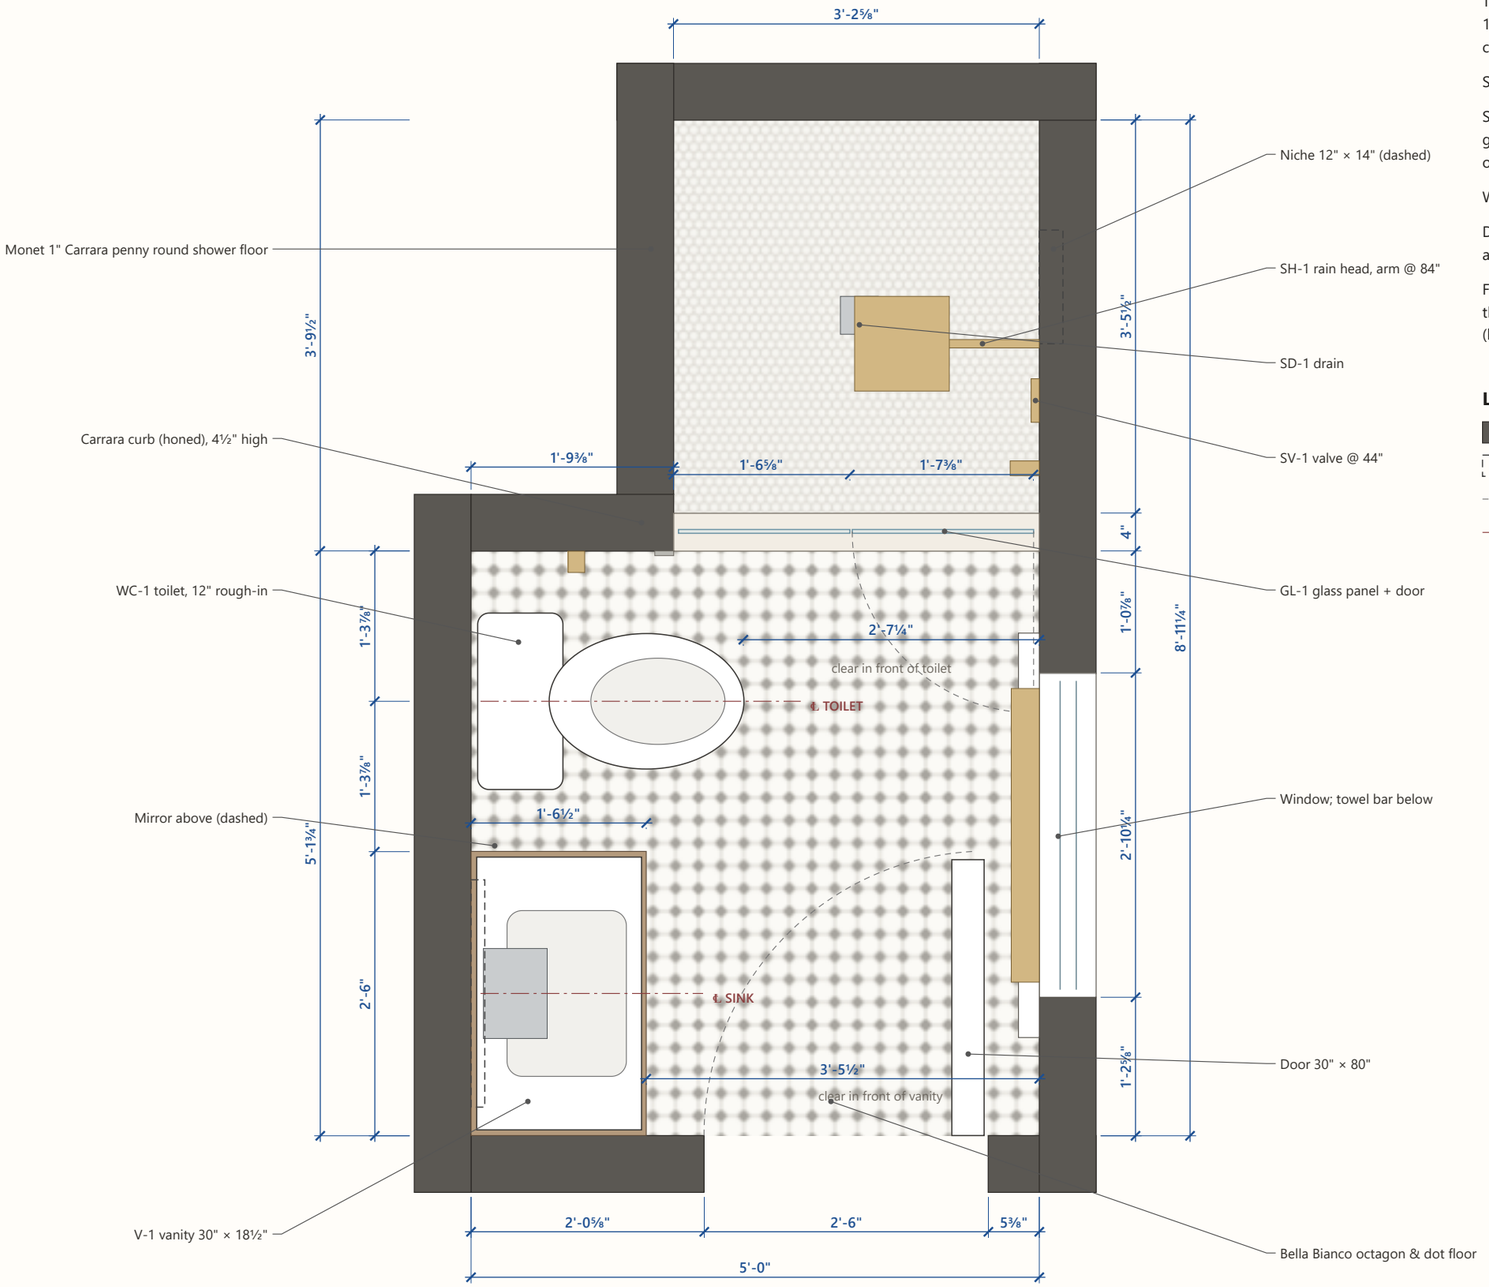

PLAN NOTES

Toilet centerline 1'-3⅜" from the vanity side and 1'-3⅜" from the jog wall (code min. 15"). 2'-7¼" clear in front (min. 21").

Sink centerline 1'-3" from the door wall.

Shower inside 3'-2⅝" × 3'-5½" beyond a 4" curb; glass 5'-11½" tall on the curb, door 1'-7⅛" hinged off the window-side wall.

Window rough opening 2'-10¼" wide, sill 4'-6⅝" AFF.

Door hinged on the window side; it opens flat against the window-side wall.

Floor tile runs under the vanity and to the curb; the shower floor is Monet 1" Carrara penny round (honed), sloped to the drain.

LEGEND

- Wall (existing / new, 6")
- Above / recessed (mirror, niche)
- Door swing
- Centerline

1 **FLOOR PLAN**

3/4" = 1'-0" on 11×17 · north = toward the shower

BATHROOM REMODEL

Simon's Bathroom

Layout, fixtures & finishes

Issued 2026-11-04

For coordination — not for construction


NOTES

Dimensions from the design model, built from the owner's SketchUp.
Verify all dimensions in field.
Do not scale drawings.
Heights are above finished floor.
Plan dims to finished wall faces.

FLOOR PLAN — DIMENSIONED


Room, fixture locations, clearances and rough-in centerlines

A-101

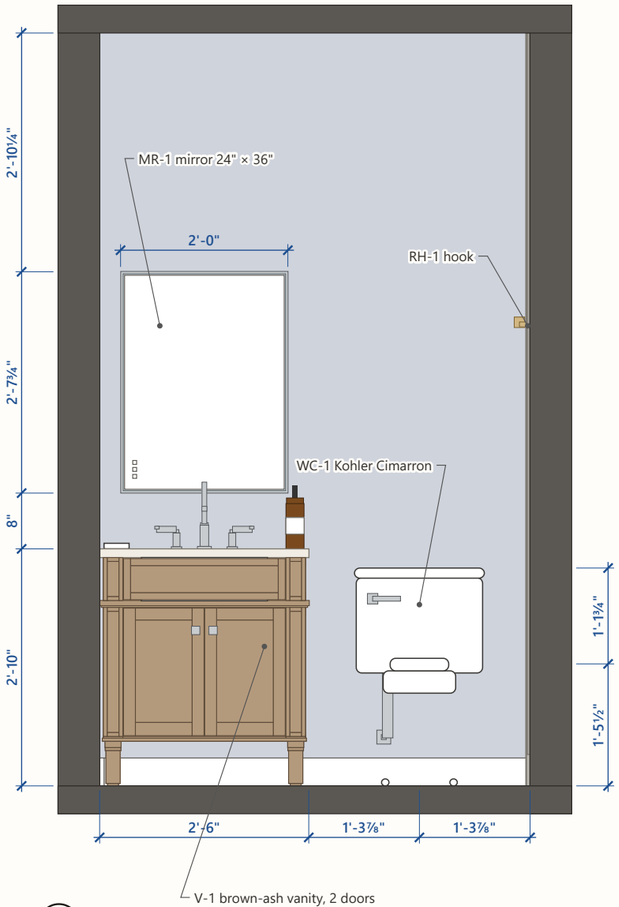

1 **VANITY & TOILET WALL**

1/2" = 1'-0" on 11×17 · looking west

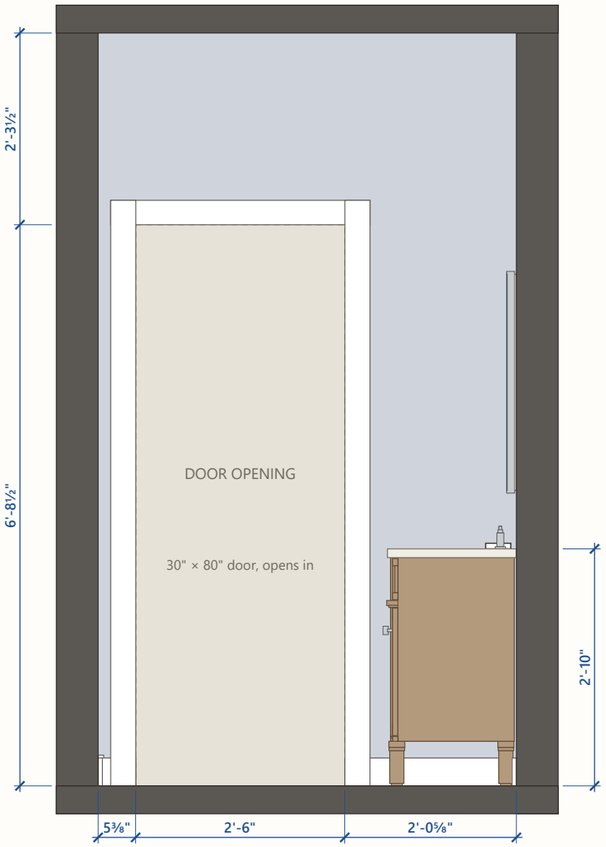

2 **DOOR WALL**

1/2" = 1'-0" on 11×17 · looking south

BATHROOM REMODEL

Simon's Bathroom

Layout, fixtures & finishes

Issued 2026-11-04

For coordination — not for construction


NOTES

Dimensions from the design model, built from the owner's SketchUp.
Verify all dimensions in field.
Do not scale drawings.
Heights are above finished floor.
Plan dims to finished wall faces.

INTERIOR ELEVATIONS


Vanity & toilet wall and door wall

A-201

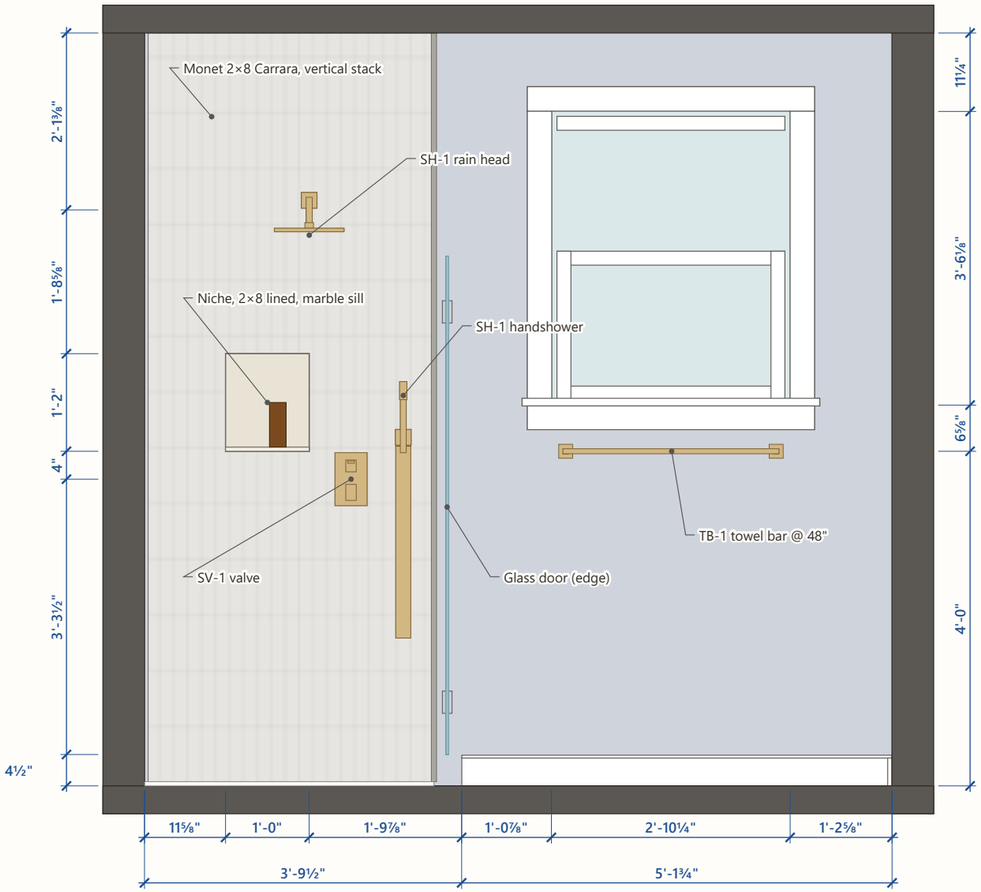

3 **WINDOW WALL**

1/2" = 1'-0" on 11×17 · looking east

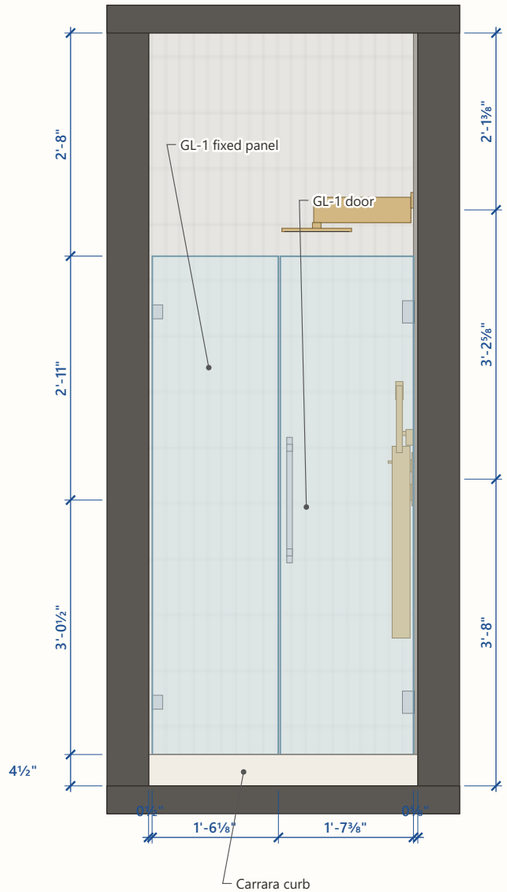

4 **SHOWER**

1/2" = 1'-0" on 11×17 · looking north, through the glass

BATHROOM REMODEL

Simon's Bathroom

Layout, fixtures & finishes

Issued 2026-11-04

For coordination — not for construction


NOTES

Dimensions from the design model, built from the owner's SketchUp.
Verify all dimensions in field.
Do not scale drawings.
Heights are above finished floor.
Plan dims to finished wall faces.

INTERIOR ELEVATIONS

Window wall (with shower side wall) and shower back wall

A-202

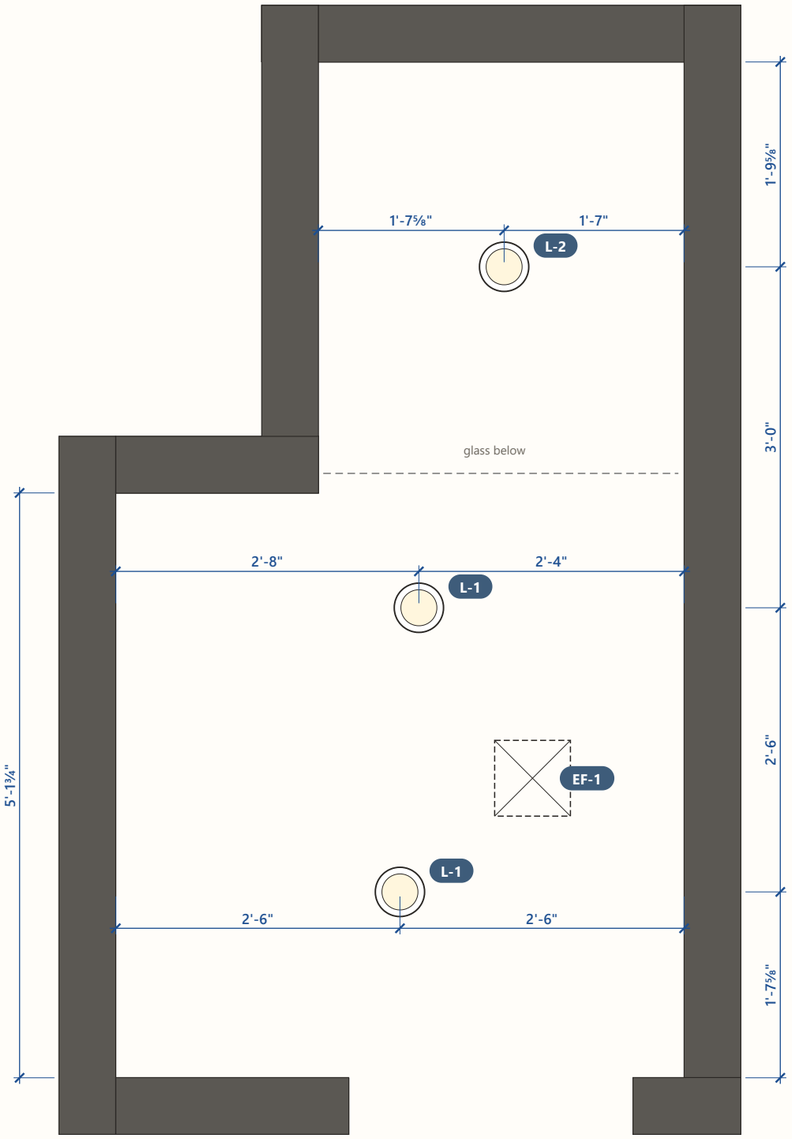

1 **REFLECTED CEILING PLAN**

3/4" = 1'-0" on 11×17 · ceiling 9'-0" AFF

LIGHTING SCHEDULE

L-1	× 2	4" recessed downlight, white trim, 2700–3000 K, dimmable
L-2	× 1	4" recessed downlight, wet-location rated (shower), 3000 K
EF-1	× 1	Exhaust fan (code required, not in model) — location TBD, ducted to exterior

NOTES

Switch at the door, latch side (window wall), 48" AFF: L-1/L-2 on a dimmer; EF-1 separate. No wall sconce (owner).

Shower downlight must be rated for wet locations; GFCI protection per code.

Dashed square = suggested fan location, clear of joists to be confirmed in field.

BATHROOM REMODEL

Simon's Bathroom

Layout, fixtures & finishes

Issued 2026-11-04

For coordination — not for construction

NOTES

Dimensions from the design model, built from the owner's SketchUp.
Verify all dimensions in field.
Do not scale drawings.
Heights are above finished floor.
Plan dims to finished wall faces.

REFLECTED CEILING & LIGHTING PLAN

Fixture locations from the design model

A-401

FIXTURES & EQUIPMENT

Tag	Item	Product	Size / finish / location
V-1	Vanity	30" traditional freestanding vanity, weathered brown ash, per owner's product photo	30" W × 18½" D × 34" H; Carrara marble top, undermount oval basin; recessed-panel corner pilasters, false drawer front, belt moulding, 2 shaker doors; turned tapered legs; satin nickel round knobs (owner choice over the stock bronze)
F-1	Lavatory faucet	Kohler-style 3-piece widespread, arched spout, lever handles	Brushed nickel (owner: not the photo's bronze); 8" spread; verify with top's 3 holes
WC-1	Toilet	Kohler Cimarron Comfort Height elongated, 2-piece	12" rough-in; 28-13/16" D, 18-5/8" W tank, 16½" rim, 31¼" H; left-hand lever
SV-1	Shower system	Delta 342701-CZ: MultiChoice R22000 valve with integrated diverter, rectangular lever trim	Champagne bronze; valve center 44" AFF on the window-side wall
SH-1	Rain head & handshower	Delta 342701-CZ: 10" square rain head on a 16" wall arm; handshower on a wall-mount holder/outlet with hose	Champagne bronze; arm 84" AFF; handshower mount 50" AFF, door side of the valve
SD-1	Shower drain	4" square tile-in drain cover	Brushed nickel; at shower center
GL-1	Shower glass	Frameless ⅜" clear (low-iron) fixed panel + hinged door with pull bar	Panel 1'-6⅛", door 1'-7⅛"; 5'-11½" tall on the curb; nickel clamps & hinges
MR-1	LED mirror	Artika Royce LED wall mirror with integrated defogger (item 1937019), vertical; frosted LED border, selectable 3000/4000/5000 K, dimmable, touch controls	24" W × 31.8" H × 1.4" D, centered over the vanity, bottom 42" AFF; brushed nickel frame; plug-in or hardwired — provide a junction box behind it
TB-1	Towel bar	30" towel bar	Champagne bronze to match SH-1; under the window at 48" AFF
RH-1	Robe hook	Single hook	Champagne bronze to match SH-1; jog wall at 66" AFF

FINISHES

Surface	Material	Where / notes
Floor	STAINMASTER Bella Bianco 12" × 12" matte ceramic marble-look octagon & dot mosaic (Lowe's 5016331083, SM592OCTXTMTLW), 6 mm	Main room and under the vanity; 2.4" white octagons, black dots; ⅛" light grey grout; grout line on the vanity wall (25 full across), equal 2" cuts at the door and curb
Shower walls	Bedrosians Monet 2" × 8" honed marble, White Carrara (100001379)	All three shower walls, pan to ceiling, tiles upright in a vertical stack; no liner; Monet ½" × 12" White Carrara trim on exposed edges; niche lined to match; 1/16" white grout; seal the marble
Shower floor	Bedrosians Monet Honed Marble Mosaic 8, 1" penny round, White Carrara (100001427)	Shower floor, sloped to the drain; white grout; same stone as the walls; seal the marble
Shower curb	White Carrara marble slab, honed, one piece (to match the shower floor and walls)	4" × 4½" high, full width under the glass
Wall border	Monet 2" × 8" White Carrara, as the shower walls	Jog wall outside the shower (toilet side): 2" band (one full column) from the shower corner, floor to ceiling, vertical stack; ½" Monet trim on the outer edge
Niche sill	Polished Carrara-type marble	Shower niche
Walls	Benjamin Moore Hale Navy HC-154 (LRV 8.4), matte (bath rated); trim stays white semi-gloss	All non-tiled walls
Ceiling	Bright flat white paint, bath rated (contrast with the navy walls)	9'-0" AFF
Trim	Semi-gloss white; 4" baseboard, door & window casings	Match existing profiles
Hardware	Satin / brushed nickel; shower system champagne bronze	Nickel: vanity knobs, faucet, drain. Bronze: SV-1, SH-1, TB-1, RH-1

BATHROOM REMODEL

Simon's Bathroom

Layout, fixtures & finishes

Issued 2026-11-04

For coordination — not for construction

NOTES

Dimensions from the design model, built from the owner's SketchUp.
Verify all dimensions in field.
Do not scale drawings.
Heights are above finished floor.
Plan dims to finished wall faces.

FIXTURE & FINISH SCHEDULE

Products and finishes as designed — confirm availability and lead times

A-501