KITCHEN REMODEL

Dimensioned cabinet & layout drawings for the contractor



Design render — looking at the cabinet wall from the living room



Design render — island, range wall and fridge / pantry

GENERAL NOTES

1. All dimensions come from the 3D design model (SketchUp → Blender), not from field measurement. Verify every dimension on site before ordering cabinets, stone or appliances.
2. Do not scale drawings — use the written dimensions. Sheets are laid out for 11×17 (tabloid); stated scales apply only at 100% print size.
3. Plan dimensions run from the finished inside face of the Breakfast (left) wall and the cabinet (back) wall. Heights are above finished floor (AFF).
4. Cabinet sizes are box widths. Back-wall fronts are FULL OVERLAY on the face frames (⅛" gaps): beaded shaker with chevron V-groove panels (2½" boards, 45°, centre seam), shallow top drawers flat slab; island fronts stay inset in its face frame, same chevron/slab styling. Toe kick 4" high (island: open 4" base on corner posts); countertops 1⅜" thick (model), 1" front overhang.
5. Appliance openings were sized to the UAKC spec package (invoice 255075, v2.2) — see A-502 for every requirement, utility and panel size. Confirm against the installation guide in each box.
6. The model has no outlets, switches or plumbing rough-in. Only fixture locations (A-401) and appliance/sink centerlines are given.
7. Wall thickness is drawn nominal (3"). Hood, hutch, fridge surround and island furniture details are design intent — shop drawings to follow from the cabinetmaker.

SHEET INDEX

A-001	Cover, notes & index
A-101	Overall floor plan
A-102	Kitchen plan — dimensioned
A-201	Cabinet wall elevation
A-202	Island elevations
A-203	Side wall elevations
A-301	Sections through range and sink
A-401	Lighting / reflected ceiling plan
A-501	Cabinet & appliance schedules
A-502	Appliance requirements (spec check)

KEY DIMENSIONS

Room, wall to wall (cabinet wall)	21'-1"
Ceiling height	9'-0"
Counter height	36"
Upper cabinets, bottom AFF	54⅛"
Upper cabinets, top AFF	8'-8"
Island top	8'-6"
Aisle, counter edge to island	48¼"

KITCHEN REMODEL

Jane's Kitchen

Cabinet & layout dimensions

Issued 2026-10-26

For coordination — not for construction


NOTES

Dimensions from the design model.
Verify all dimensions in field.
Do not scale drawings.
Heights are above finished floor.
Plan dims from inside face of
left wall / back wall.

COVER, NOTES & INDEX

General notes · sheet index · design intent

A-001

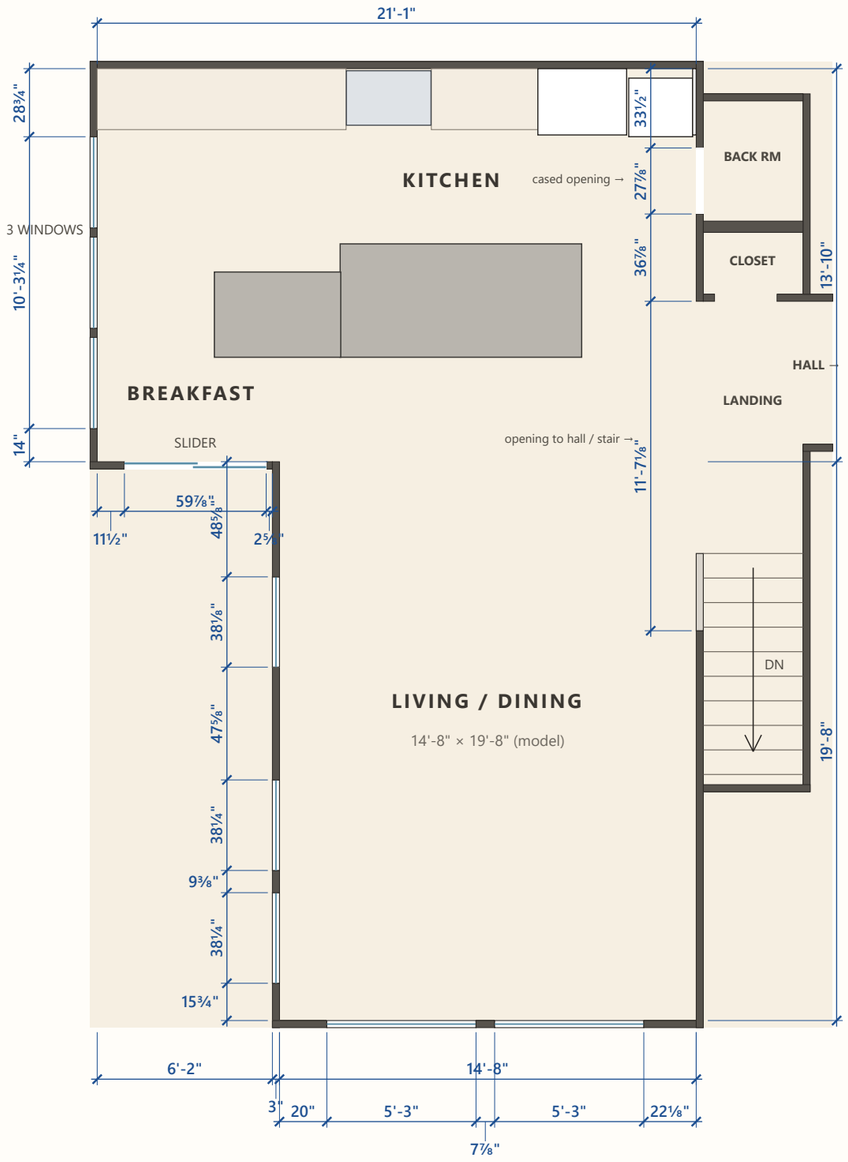

LEGEND

- Wall (nominal 3")
- Window
- Marble counter (perimeter)
- Black stone (island, extension)
- Tall cabinet / appliance panel
- Sliding door, open position
- Half wall / guard

Room names follow the floor plan supplied by the owner. Living / Dining walls and windows, and the hall, closet, back room and stair beyond the right wall, are approximate — verify on site. Stair direction assumed DN.

1 OVERALL FLOOR PLAN

3/16" = 1'-0" at 11×17 · window sizes approximate (from floor plan)

KITCHEN REMODEL

Jane's Kitchen

Cabinet & layout dimensions

Issued 2026-10-26

For coordination — not for construction


NOTES

Dimensions from the design model.
Verify all dimensions in field.
Do not scale drawings.
Heights are above finished floor.
Plan dims from inside face of left wall / back wall.

OVERALL FLOOR PLAN

Kitchen, Breakfast and Living / Dining

A-101

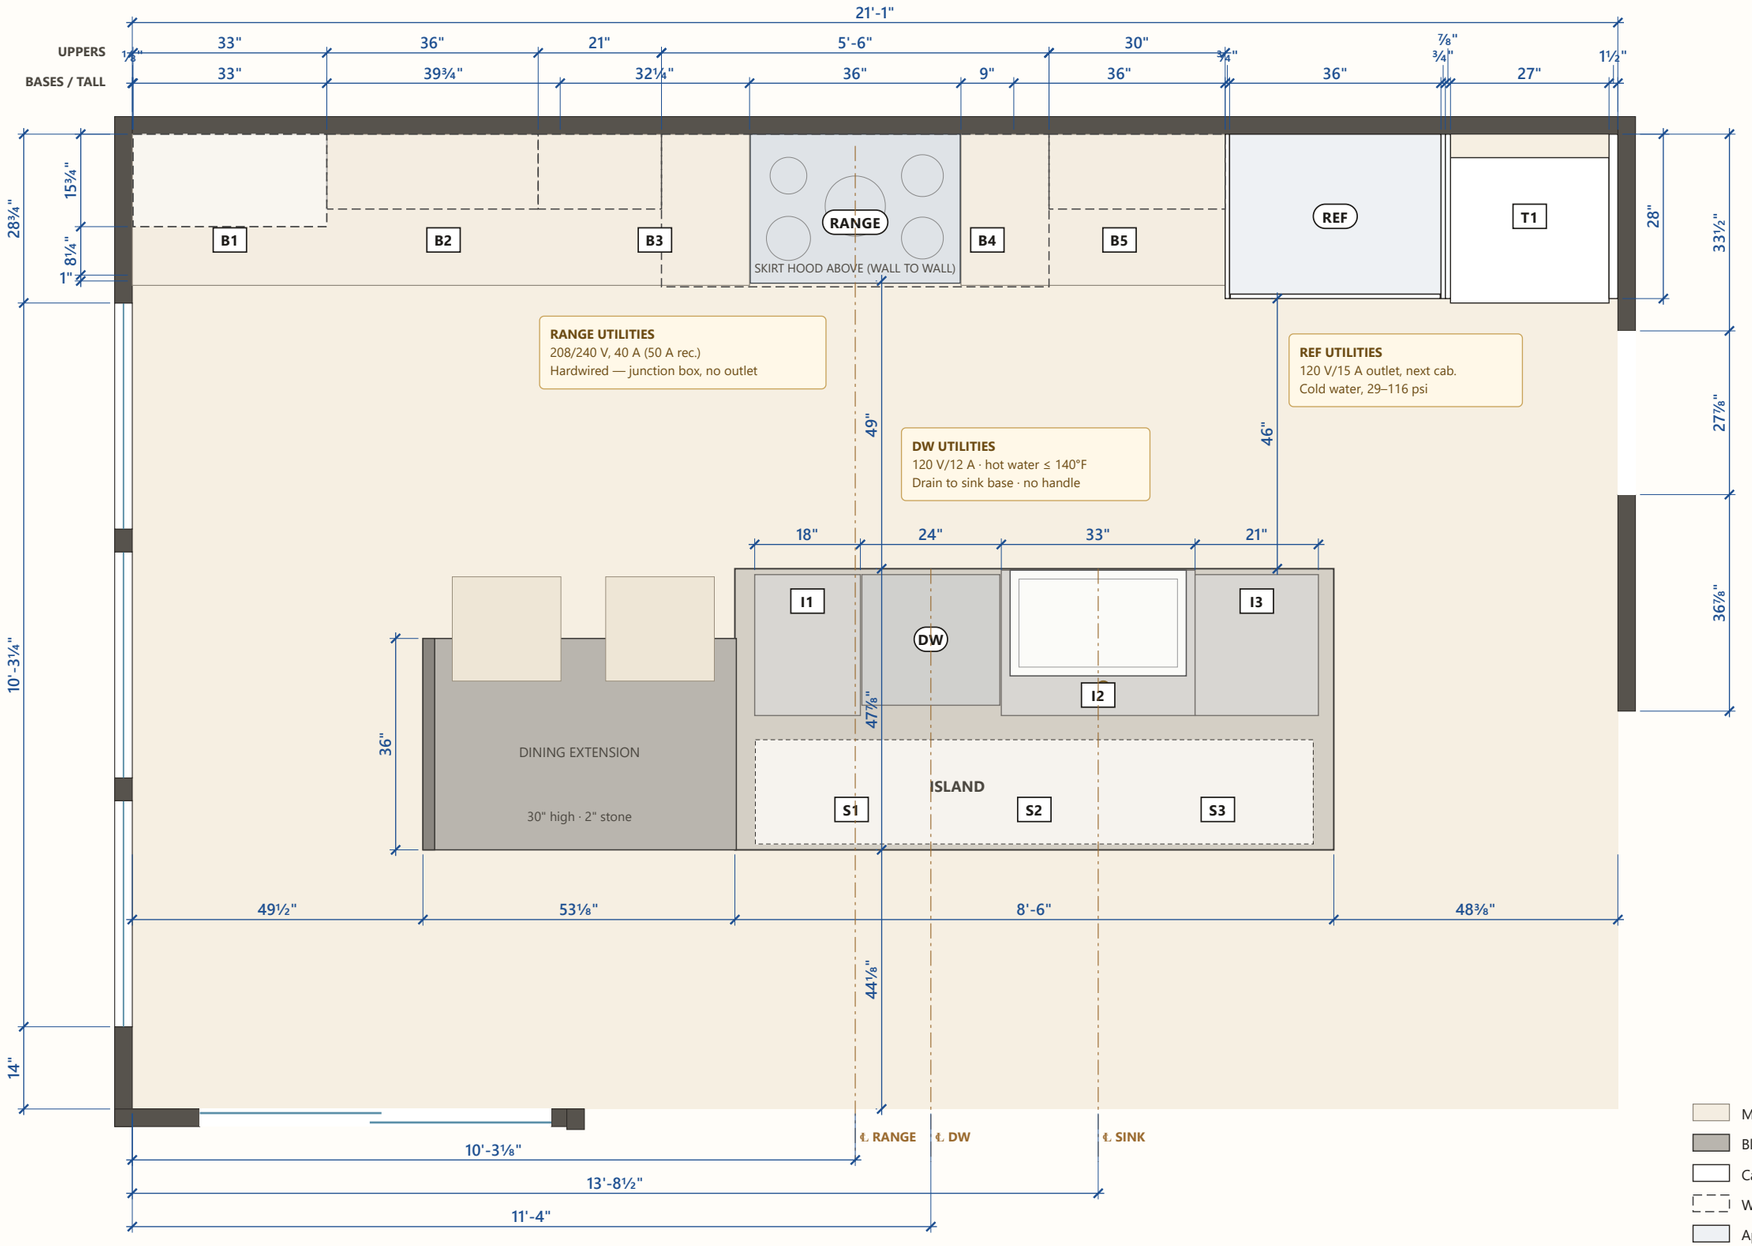

Marble counter (perimeter)
Black stone (island top, extension)
Cabinet box
Wall cabinet / hood above
Appliance (panel-ready)
Loose furniture

1 **KITCHEN PLAN**

≈ 1/2" = 1'-0" at 11×17 (reduced to fit) — use dimensions · dashed = cabinets/hood above

KITCHEN REMODEL

Jane's Kitchen

Cabinet & layout dimensions

Issued 2026-10-26

For coordination — not for construction


NOTES

Dimensions from the design model.
Verify all dimensions in field.
Do not scale drawings.
Heights are above finished floor.
Plan dims from inside face of
left wall / back wall.

KITCHEN PLAN — DIMENSIONED

Cabinet runs, island location,
clearances and rough-in centerlines

A-102

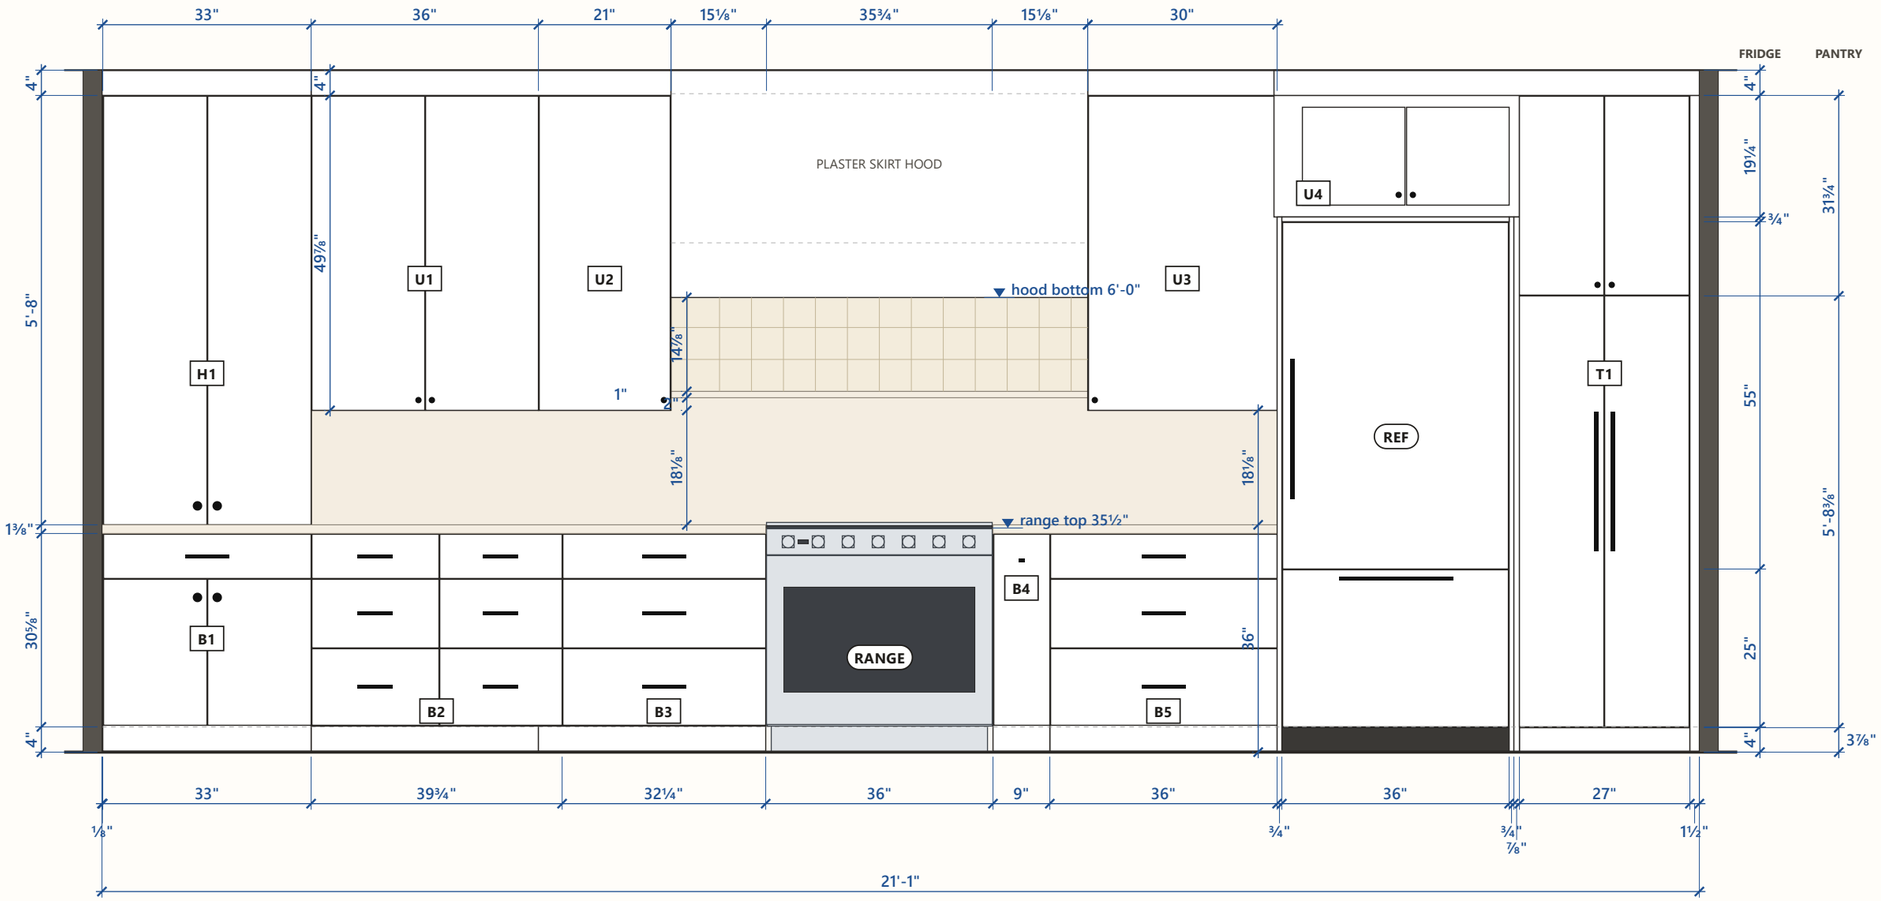

1 CABINET WALL ELEVATION

1/2" = 1'-0" at 11×17 · looking at the back wall from the room

Backsplash: one 2cm Calacatta Macchia Vecchia marble slab, counter to the underside of the uppers (18⅛"). In the range bay the marble stops 2" above the bottom of the uppers (56⅛" AFF) and is capped by a 1"-thick marble ledge, 3" deep off the slab face. Above the ledge, from the ledge up behind the hood: Bedrosians Cloé 5×5 Creme glossy ceramic tile (DECCLOCRE55G), straight stacked grid, 1/16" grout, a full course starting on the ledge, grid centered on the hood centerline (joint on the centerline). ≈6.8 sq ft visible; order ≈8 sq ft.

Hood: smooth plaster skirt hood, 5'-6" wide — the whole bay, wall to wall between uppers U2 and U3 — from 6'-0" AFF to the ceiling. Side profile (see A-301): 8⅝" vertical apron projecting 26" from the wall, then an ogee over 23⅝" back to flush with the upper cabinet doors (12" deep), straight to the ceiling. Stainless insert in a recess underneath, 3 baffle filters, 2 lights. Bottom of hood 6'-0" AFF = 36⅛" above the cooktop.

Hutch H1 sits on the counter, 15" deep (3" proud of the 12" uppers), top flush with uppers.

Hardware: uppers — small polished-brass mushroom knob (~1"), tucked into the bottom meeting corner; lower doors — Ashley Norton 3624 Round Step Knob 1½", Natural Bronze (NB) aged patina; lower drawers — Ashley Norton MB5341 Classic Pull, Distressed Brass (DBS), 5⅛" on drawers under 24" wide, 6⅜" on wider ones; fridge, freezer drawer and appliance-garage doors (T1) — polished-brass bar pulls with acorn finials (22⅛" on the door and garage, 18⅛" on the freezer drawer, model).

KITCHEN REMODEL

Jane's Kitchen

Cabinet & layout dimensions

Issued 2026-10-26

For coordination — not for construction


NOTES

Dimensions from the design model.
Verify all dimensions in field.
Do not scale drawings.
Heights are above finished floor.
Plan dims from inside face of
left wall / back wall.

CABINET WALL ELEVATION


Back wall: hutch, range & hood, fridge, pantry

A-201

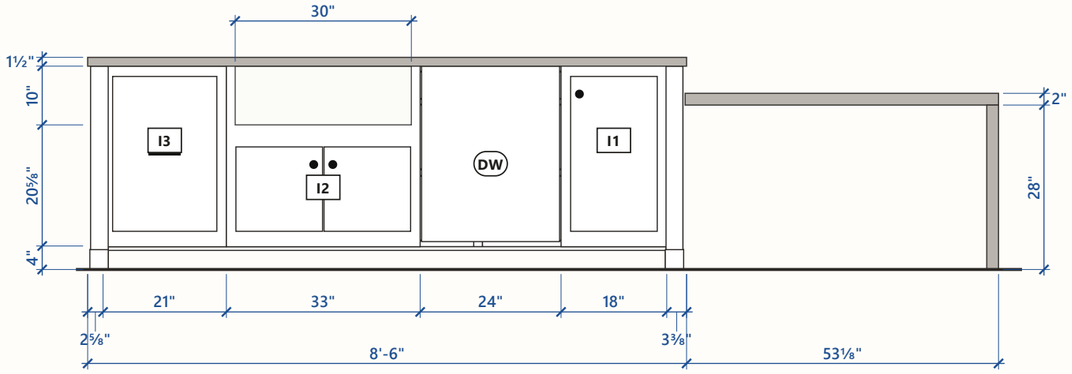


1 ISLAND — WORKING SIDE (SINK / DISHWASHER)

≈ 1/2" = 1'-0" (reduced) · seen from the range

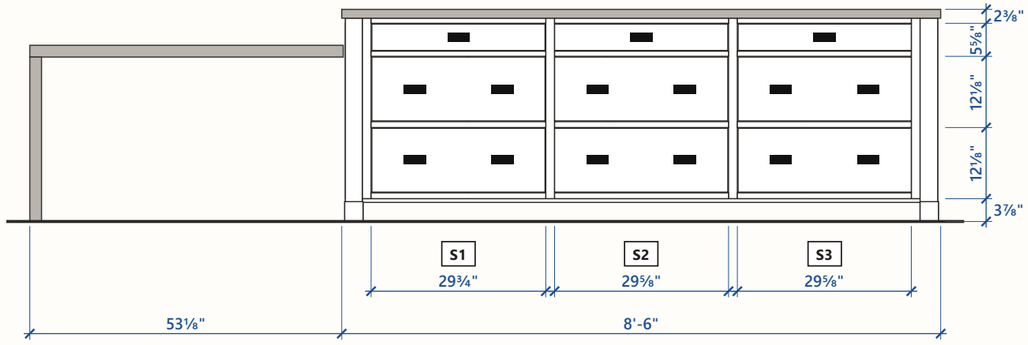


2 ISLAND — SEATING SIDE (STORAGE)

≈ 1/2" = 1'-0" (reduced) · seen from the living room · opening widths, 1½" stiles

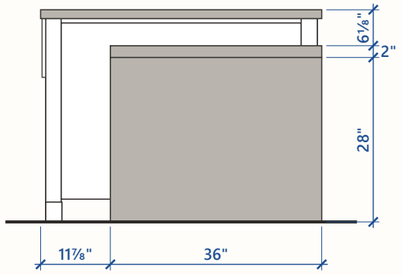

3 ISLAND — LEFT END WITH DINING EXTENSION

≈ 1/2" = 1'-0" (reduced) · seen from the Breakfast end

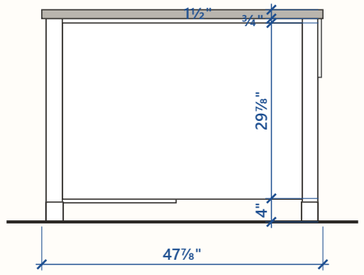

4 ISLAND — RIGHT END (HALL SIDE)

≈ 1/2" = 1'-0" (reduced)

Island body: painted to match the perimeter cabinets, square corner posts to the floor in polished-nickel corner caps, paneled ends. Open base, no toe kick: the cabinetry stops 3⅞" above the floor all round (a painted bottom panel closes the drawer side; the dishwasher panel still runs to the floor). Seating side: 3 columns, each a short flat slab drawer over two deep inset beaded drawers with chevron panels, with Ashley Norton MB5120 Faux Screw Bin Pulls, Distressed Brass (DBS) — one on each top drawer, two on each deep drawer (15 total). Top: honed black stone with an ogee edge, overhangs the body ½"–⅞" on all sides (model).

Working side (faces the range): 18" door base, 24" dishwasher with custom panel, 33" sink base with 30" apron-front sink, 21" double trash pull-out.

Dining extension butts the left end: 2" stone slab, 30" high, waterfall leg at the free end, flush with the island's seating (living-room) side.

KITCHEN REMODEL

Jane's Kitchen

Cabinet & layout dimensions

Issued 2026-10-26

For coordination — not for construction


NOTES

Dimensions from the design model.
Verify all dimensions in field.
Do not scale drawings.
Heights are above finished floor.
Plan dims from inside face of
left wall / back wall.

ISLAND ELEVATIONS

Working side, seating side and both ends


A-202

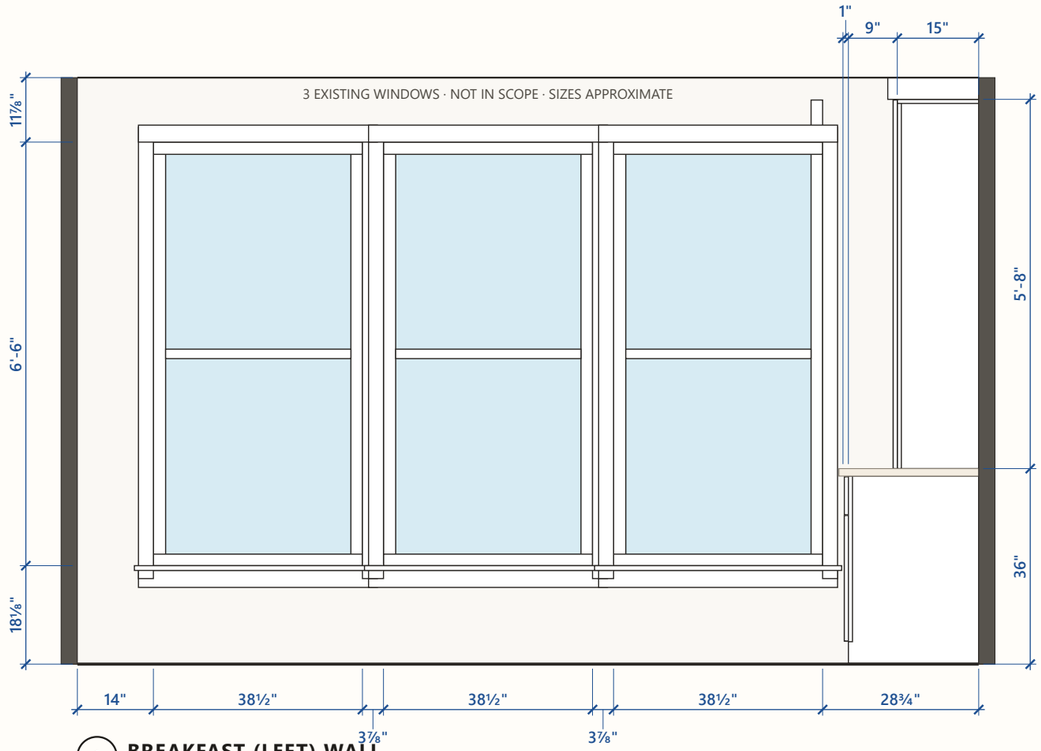

1 BREAKFAST (LEFT) WALL

≈ 1/2" = 1'-0" (reduced) · seen from the room · cabinet wall at right

Three existing windows on this wall stay as they are — sizes are approximate. The 2-panel sliding door is around the corner on the porch wall (see A-101). Hutch H1 and base B1 return against this wall — scribe to the wall.

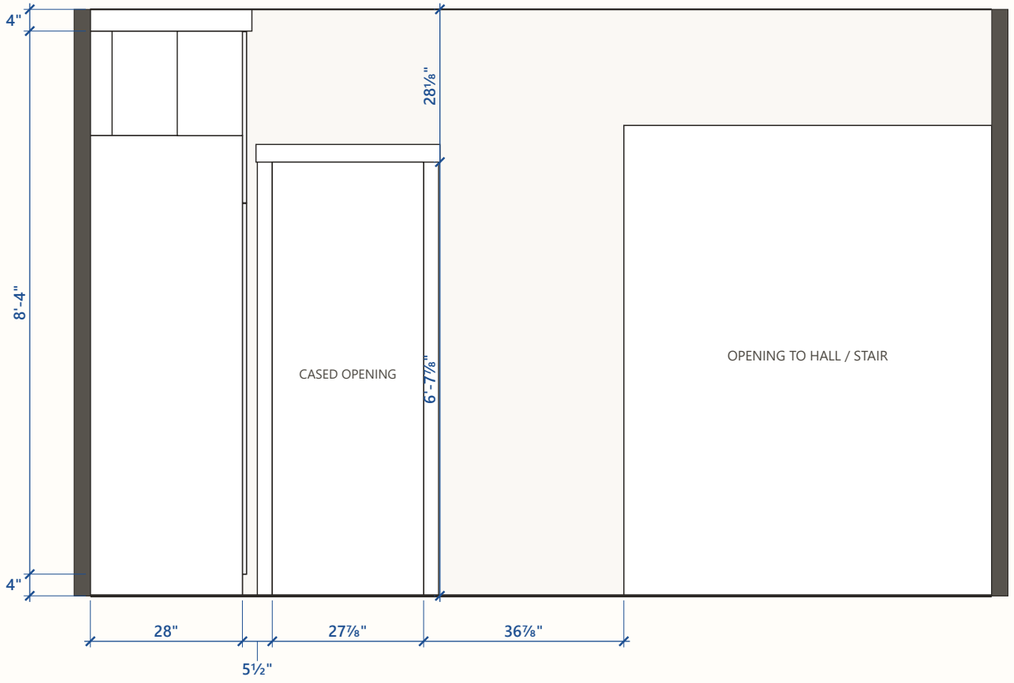

2 HALL (RIGHT) WALL

≈ 1/2" = 1'-0" (reduced) · seen from the room · cabinet wall at left

The existing swing door comes out; the doorway to the small room behind the kitchen stays a cased opening with no door (owner's choice). A pocket door doesn't fit per the owner's floor plan: the closet wall meets this wall 4–8" left of the opening, and on the right there is only ≈28" to the corner, with the bath wall teeing in and the pantry against it (likely plumbing on both sides). A surface-mounted sliding door could be added later: there is ≈32" of clear wall to the left. Verify on site.

Pantry side is closed with a 1½" filler to the wall (model). Tall cabinets and fridge panels stand 4" proud of the base cabinet faces (28" deep).

KITCHEN REMODEL

Jane's Kitchen

Cabinet & layout dimensions

Issued 2026-10-26

For coordination — not for construction


NOTES

Dimensions from the design model.
Verify all dimensions in field.
Do not scale drawings.
Heights are above finished floor.
Plan dims from inside face of
left wall / back wall.

SIDE WALL ELEVATIONS


Breakfast wall (3 windows) and hall wall (pantry end, kitchen doorway, hall opening)

A-203

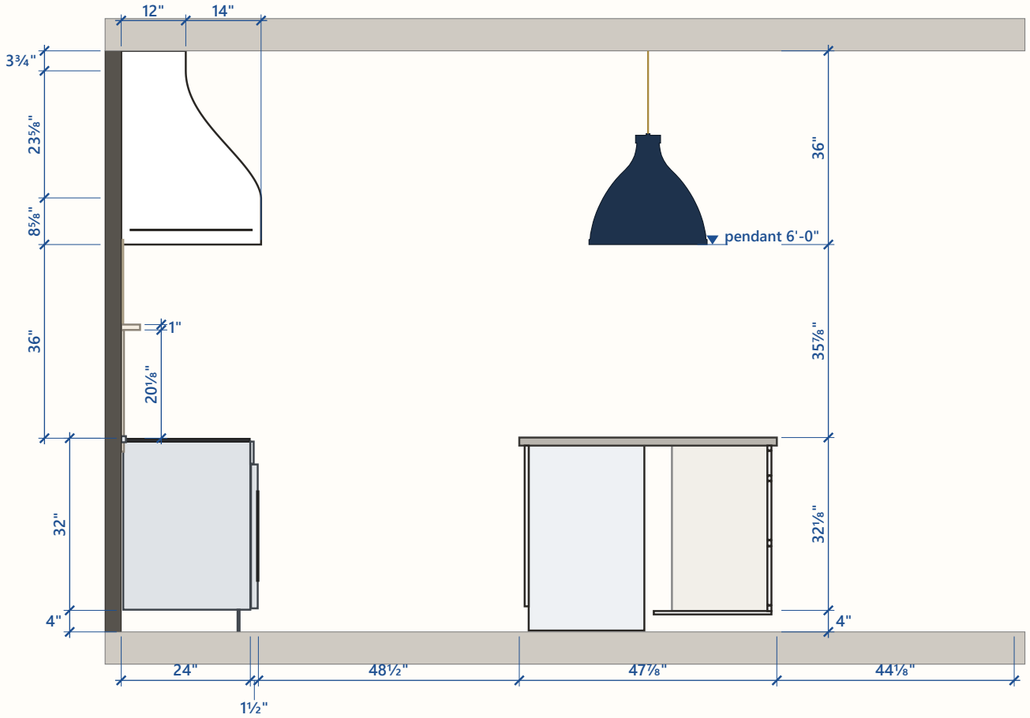

A SECTION A — THROUGH RANGE, HOOD & DISHWASHER

≈ 3/8" = 1'-0" · cut elements only

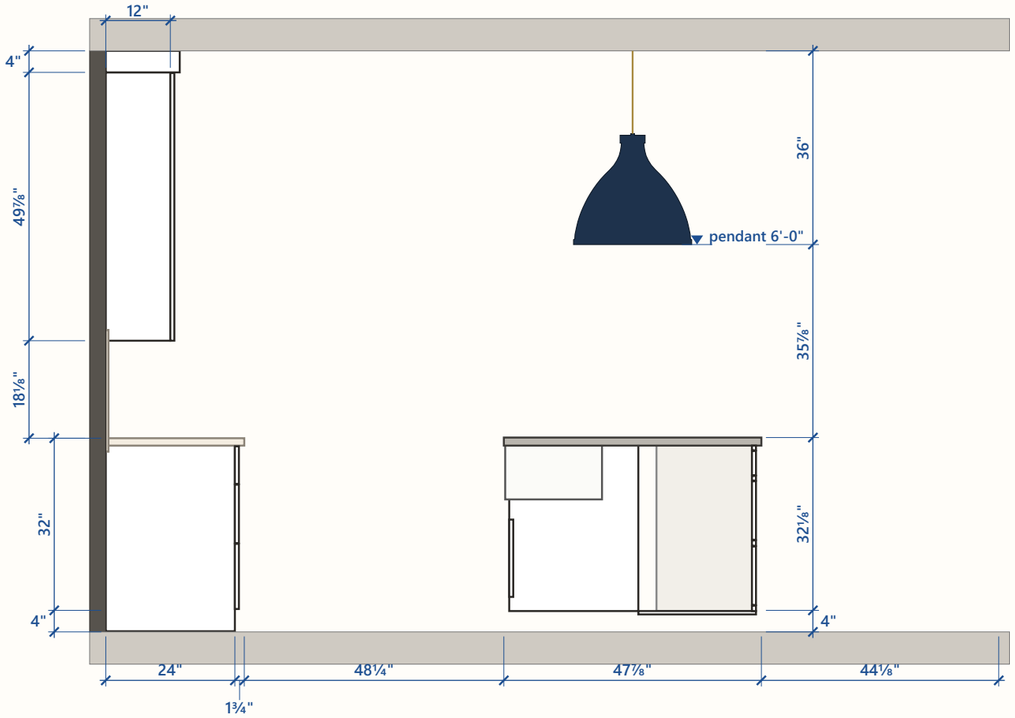

B SECTION B — THROUGH SINK BASE & 30" UPPER

≈ 3/8" = 1'-0" · cut 13" right of sink ℄ · nearest pendant shown beyond

Clearances (model):

- Aisle between back counter edge and island top: 49".
- Fridge panels to island top: 46" (fridge door swings into this aisle).
- Island seating side to Breakfast/porch wall: 44⅛" (Breakfast end).
- Island right end to hall wall: 48¼".

Pendants: Hudson Valley Painted No. 3 (MDS362-AGB/DBL), shade bottom 6'-0" AFF (level with the hood bottom), 35⅞" above the island top. Section A shows the skirt hood's side profile (apron + ogee).
Range hood: bottom 6'-0" AFF, 36⅛" above the cooktop; confirm the hood insert maker's required mounting height and duct route.

KITCHEN REMODEL

Jane's Kitchen

Cabinet & layout dimensions

Issued 2026-10-26

For coordination — not for construction


NOTES

Dimensions from the design model.
Verify all dimensions in field.
Do not scale drawings.
Heights are above finished floor.
Plan dims from inside face of left wall / back wall.

SECTIONS

Depths, clearances and heights through the range and the sink

A-301

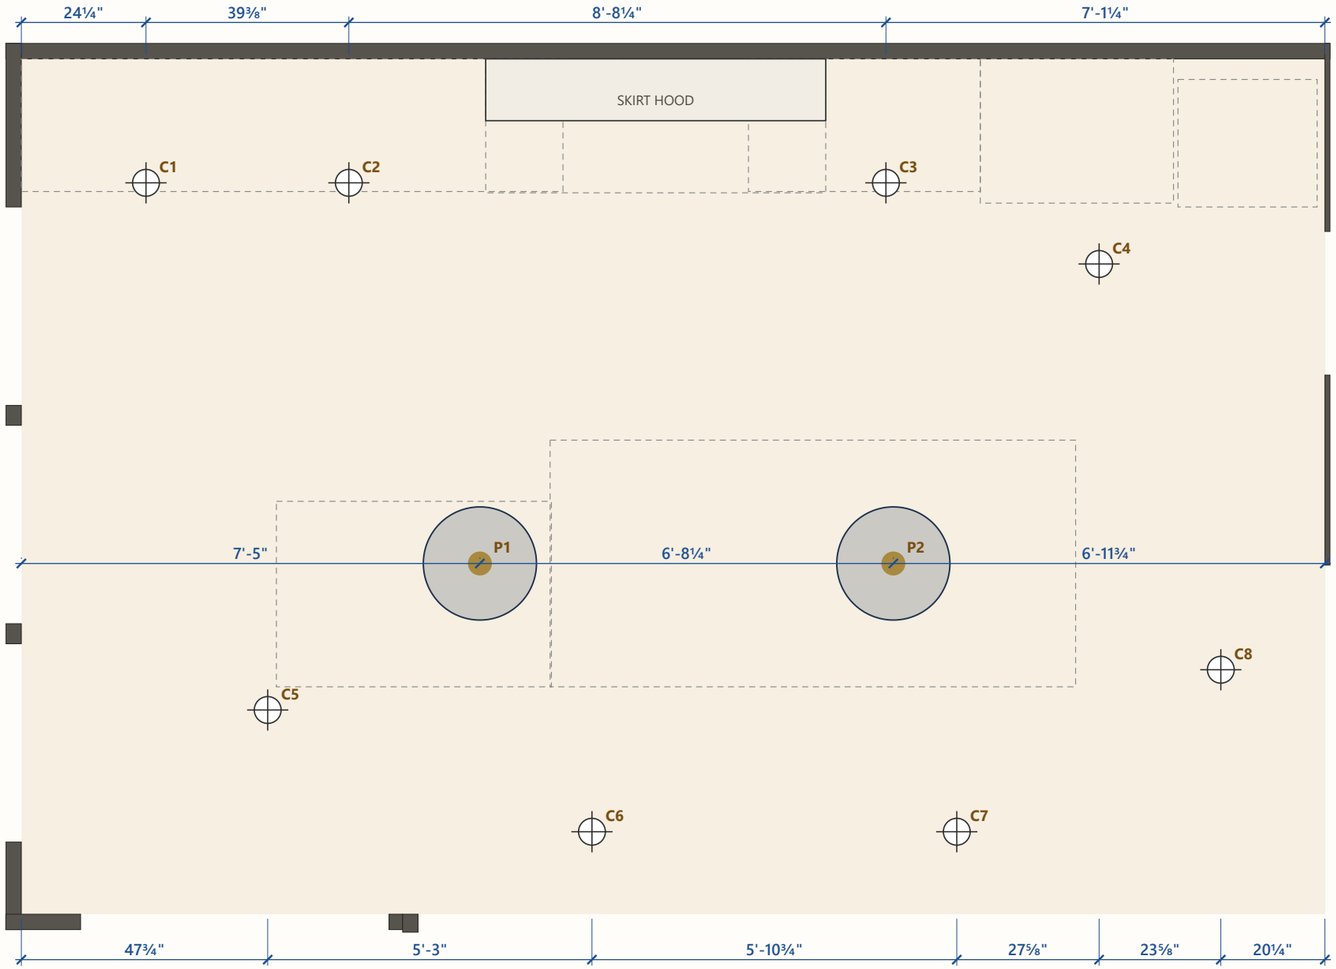

1 **REFLECTED CEILING PLAN**

≈ 3/8" = 1'-0" · ceiling 9'-0" · counters shown dashed for reference

FIXTURE LOCATIONS

Tag	Fixture	X from left wall	From back wall	Height
C1	Recessed downlight (≈5" tri…	24¼"	24"	in ceiling
C2	Recessed downlight (≈5" tri…	5'-3½"	24"	in ceiling
C3	Recessed downlight (≈5" tri…	13'-11¾"	24"	in ceiling
C4	Recessed downlight (≈5" tri…	17'-5¼"	39¾"	in ceiling
C5	Recessed downlight (≈5" tri…	47¾"	10'-6⅜"	in ceiling
C6	Recessed downlight (≈5" tri…	9'-2¾"	12'-6"	in ceiling
C7	Recessed downlight (≈5" tri…	15'-1½"	12'-6"	in ceiling
C8	Recessed downlight (≈5" tri…	19'-4¾"	9'-10½"	in ceiling
P1	Painted No. 3 pendant (HVL)	7'-5"	8'-2"	bottom 6'-0" AFF
P2	Painted No. 3 pendant (HVL)	14'-1¼"	8'-2"	bottom 6'-0" AFF

Locations are fixture centers. Downlights C1–C3 over the counters sit 24" out from the back wall; adjust to the joists. Hood insert has 2 integral lights. No wall sconces and no under-cabinet lights in the design. Pendants P1/P2: Hudson Valley Lighting Painted No. 3, MDS362-AGB/DBL (aged brass / darkest blue), 22½" dia. × 25" H shade, ring-and-bar chain to an aged-brass canopy; the model uses 3 lamps behind a white glass diffuser — verify lamping with the HVL spec sheet. Switching, outlets and circuits are not in the model — lay these out to code (GFCI/AFCI, island receptacle, 240 V range).

KITCHEN REMODEL

Jane's Kitchen

Cabinet & layout dimensions

Issued 2026-10-26

For coordination — not for construction

NOTES

Dimensions from the design model.
Verify all dimensions in field.
Do not scale drawings.
Heights are above finished floor.
Plan dims from inside face of left wall / back wall.

LIGHTING / REFLECTED CEILING PLAN

Fixture locations from the design model

A-401

CABINET SCHEDULE

Tag	Description	Location	Width	Height	Depth	Bottom AFF	Fronts / hardware
B1	Base — drawer over 2 doors	Back wall, under hutch	33"	34½"	24¾"	⅛"	MB5341 6⅜" pull (DBS) on drawer; 3624 step knobs (NB) at meeting stiles
B2	Base — 2 drawer stacks × 3 (18¾" + 18")	Back wall, left drawer run	39¾"	34½"	23¼"	⅛"	MB5341 Classic Pull 5⅛" (DBS), centered on each drawer
B3	Base — wide drawer stack × 3 (30¾")	Back wall, left of range	32¼"	34½"	23¼"	⅛"	MB5341 Classic Pull 6⅜" (DBS), centered on each drawer
B4	Base — spice pull-out, full height (1 front)	Back wall, right of range	9"	34½"	24¾"	⅛"	MB5341 Classic Pull 5⅛" (DBS), vertical near the top
B5	Base — 3 drawers	Back wall, left of fridge	36"	34½"	24¾"	⅛"	MB5341 Classic Pull 6⅜" (DBS)
H1	Countertop hutch — 2 doors, sits on counter	Back wall, Breakfast end	33"	5'-8"	15¾"	36"	3624 step knobs (NB), low at meeting stiles
U1	Wall cabinet — 2 doors	Back wall	36"	49⅞"	12¾"	54⅛"	~1" polished-brass knobs, bottom meeting corners
U2	Wall cabinet — 1 door	Back wall, left of hood	21"	49⅞"	12¾"	54⅛"	~1" polished-brass knob, bottom corner
U3	Wall cabinet — 1 door, hinged right	Back wall, right of hood	30"	49⅞"	12¾"	54⅛"	~1" polished-brass knob, bottom-left corner
U4	Wall cabinet over fridge — 2 doors	Above refrigerator	38⅞"	19¼"	12"	7'-¾"	~1" polished-brass knobs, bottom meeting corners
T1	Tall pantry / appliance garage — 2 tall doors + 2 upper doors	Back wall, hall end	27"	8'-4⅛"	24¾"	3⅞"	tall doors: polished-brass acorn-finial bar pulls; upper doors: ~1" brass knobs
I1	Island base — 1 door	Island, working side	18"	30⅞"	24"	3⅞"	3624 step knob (NB)
I2	Island sink base — 2 doors, 30" apron-front sink	Island, working side	33"	30⅞"	24¾"	3⅞"	3624 step knobs (NB), doors below apron sink
I3	Island base — double trash pull-out	Island, working side	21"	30¾"	24"	3⅞"	MB5341 Classic Pull 5⅛" (DBS)
S1	Island seating-side storage — 3 drawers (short top, 2 deep)	Island, living-room side	29¾"	30⅝"	17¾"	4"	MB5120 bin pulls (DBS): 1 on top drawer, 2 on each deep drawer
S2	Island seating-side storage — 3 drawers (short top, 2 deep)	Island, living-room side	29¾"	30⅝"	17¾"	4"	MB5120 bin pulls (DBS): 1 on top drawer, 2 on each deep drawer
S3	Island seating-side storage — 3 drawers (short top, 2 deep)	Island, living-room side	29¾"	30⅝"	17¾"	4"	MB5120 bin pulls (DBS): 1 on top drawer, 2 on each deep drawer

APPLIANCES & FIXTURES

Tag	Model	Type	Opening in model (W × H × D)	Notes for the GC
RANGE	Bosch HIS5657U	36" freestanding induction range	36" between cabinets, counter 36"	208/240 V, 40 A (50 A rec.), HARDWIRED to a junction box; ℄ 10'-3⅛" from left wall
REF	Thermador T36IB100SP	36" built-in, panel-ready, single door over freezer drawer	36" × 7'-0" × 28"	Spec cutout 84 × 36 × 25 ✓; 120 V/15 A outlet + cold water in the adjacent cabinet; ¾" panels
DW	Thermador Sapphire DWHD660EPR	24" panel-ready (fully integrated)	24" between cabinets, under 34⅝" top	Spec 24" min. ✓; 120 V/12 A, hot water, drain to sink base; push-to-open panel, NO handle
SINK	Rohl 30" fireclay apron-front	Single bowl, apron front, in 33" sink base I2	30" × 18", apron top at counter	Sink ℄ 13'-8½" from left wall; stone notched around apron
HOOD	Plaster hood + stainless insert	3 baffle filters, 2 lights	5'-6" wide skirt, wall to wall, bottom 6'-0" AFF	Plaster skirt hood, ogee side profile (A-301); select insert & blower; duct + make-up air per code / insert maker
TILE	Bedrosians Cloé 5×5 Creme	Glossy ceramic DECCLOCRE55G, range bay	5'-6" × 14⅞" visible, ledge to hood	Stacked grid, 1/16" grout, full course on the ledge, joint on hood ℄; ≈6.8 sq ft visible, order ≈8 sq ft
FAUCET	Brass gooseneck, side lever	Single hole	behind sink ℄	Hole at sink ℄, ≈1¾" behind bowl

Finishes (design intent): perimeter + island cabinets painted greige-cream, approx. Benjamin Moore Revere Pewter HC-172 (custom match ≈ #D0CABC; final color by owner sample), chevron-panel beaded shaker, flat slab top drawers, full overlay (island inset). Counters: 2cm Calacatta Macchia Vecchia marble to match the backsplash (same slab lot; honed recommended for etch resistance). Island top (ogee edge) and dining extension (waterfall): honed black stone. Backsplash: Macchia Vecchia slab + marble ledge; Bedrosians Cloé 5×5 Creme glossy ceramic tile (DECCLOCRE55G) in the hood bay, stacked grid, 1/16" grout. Smooth plaster skirt hood. Hardware: polished-brass knobs (uppers), Ashley Norton 3624 NB step knobs (lower doors), MB5341 DBS pulls (drawers), MB5120 DBS bin pulls (island), polished-brass acorn-finial bar pulls (fridge, appliance garage); brass faucet; chevron oak floor.

KITCHEN REMODEL

Jane's Kitchen

Cabinet & layout dimensions

Issued 2026-10-26

For coordination — not for construction

NOTES

Dimensions from the design model.
Verify all dimensions in field.
Do not scale drawings.
Heights are above finished floor.
Plan dims from inside face of
left wall / back wall.

CABINET & APPLIANCE SCHEDULES

Sizes from the design model — confirm
with shop drawings

A-501

APPLIANCE REQUIREMENTS

From the UAKC spec package, invoice 255075, v2.2 (Oct 20, 2026). ✓ = the design meets the spec. Always confirm against the installation guide in the box.

REF — Thermador T36IB100SP

36" built-in bottom-freezer refrigerator, panel-ready

CUTOUT & CLEARANCES	Spec	Design	
Cutout width	36"	36"	✓
Cutout height	84"	7'-0"	✓
Cutout depth	≥ 25"	28"	✓
Finished side returns	flush, ≥ 4" deep	28"	✓

POWER, WATER & DRAIN

- 120 V, 60 Hz, 15 A; 3-prong plug, 118" cord
- Outlet in an ADJACENT cabinet (preferred); behind the unit only if it can be switched off at the breaker
- Cold water line, 29–116 psi, reachable from the next cabinet
- Lines route through the recess at the base of the unit

PANELS & INSTALL

- Custom panels ¾" thick (clearances assume ¾")
- Door panel max 121 lb; drawer panels max 66 lb / 103 lb
- Door swing 115° max, 90° min to reach every drawer
- Unit height adjusts 83 9/16–85½" (83⅞" for an 84" niche)

RANGE — Bosch HIS5657U

36" 500 Series freestanding induction range

CUTOUT & CLEARANCES	Spec	Design	
Cutout width	36"	36"	✓
Counter depth	≥ 25"	25¾"	✓
Cooktop to hood bottom	≥ 30"	36"	✓
Counter to upper cabinets	≥ 18"	18⅛"	✓
Upper cabinet depth	≤ 13"	12¾"	✓

POWER, WATER & DRAIN

- 208/240 V, 60 Hz; 40 A breaker (50 A recommended), 8,400 W
- HARDWIRED — no cord: junction box, not a receptacle
- Anti-tip bracket (included) must be installed
- Zero clearance to the side cabinets below the counter

PANELS & INSTALL

- Freestanding, stainless; 35 15/16" W, 26 19/64" deep incl. bull nose
- Height adjusts 35¾–36¾" — set flush with the 36" counter

DW — Thermador Sapphire DWHD660EPR

24" custom-panel dishwasher

CUTOUT & CLEARANCES	Spec	Design	
Cutout width	24" min. (23⅝–24¼)	24"	✓
Cutout height (to underside of top)	33⅞–35"	34⅝"	✓
Cutout depth	24"	24"	✓
Toe kick height	3⅝–7½"	4"	✓

POWER, WATER & DRAIN

- 120 V, 60 Hz, 12 A; 67" cord (reaches 45" left / 56" right of the unit's corner)
- Hot water ≤ 140°F, ≥ 14 psi
- Drain hose 90½" — run to the sink base I2 (extension SGZ1010UC if needed)
- Optional install kit SMZ3IN1UC (junction box, 90° elbow, supply hose)

PANELS & INSTALL

- Custom panel 23⅛–23⅜" W (24" allowed by cabinet design) × 27½–30⅛" H × ⅝–⅞" thick, 11–18 lb
- PUSH-TO-OPEN — no handle on the panel
- Panel height measured from the underside of the countertop

DESIGN CHANGES MADE FOR THESE SPECS (Oct 21, 2026)

- Refrigerator opening reduced from 37" to 36": ¾" end panels each side, plus a ⅞" filler between the right panel and the pantry.
- Dishwasher opening widened from 23¾" to 24": the 18" door base I1 slides ¼" toward the island end (it had ⅞" spare).
- Dishwasher panel has no handle — the Sapphire opens with a push.

KITCHEN REMODEL

Jane's Kitchen

Cabinet & layout dimensions

Issued 2026-10-26

For coordination — not for construction

NOTES

Dimensions from the design model.
Verify all dimensions in field.
Do not scale drawings.
Heights are above finished floor.
Plan dims from inside face of left wall / back wall.

APPLIANCE REQUIREMENTS

Manufacturer specs checked against the design

A-502